

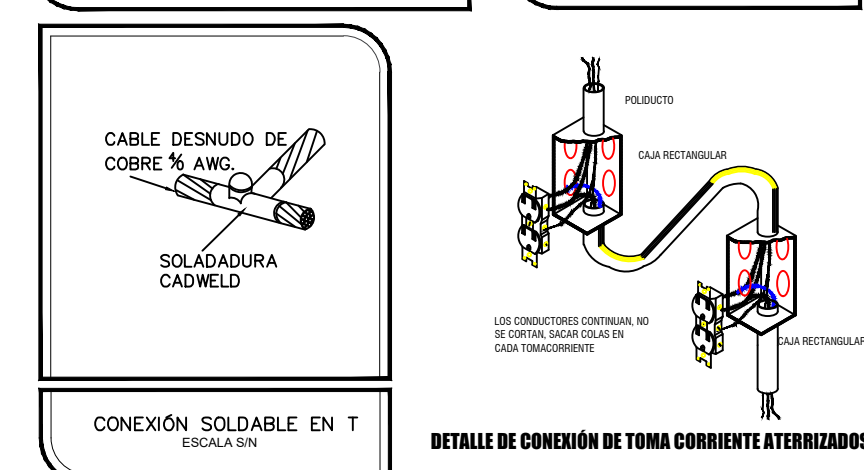
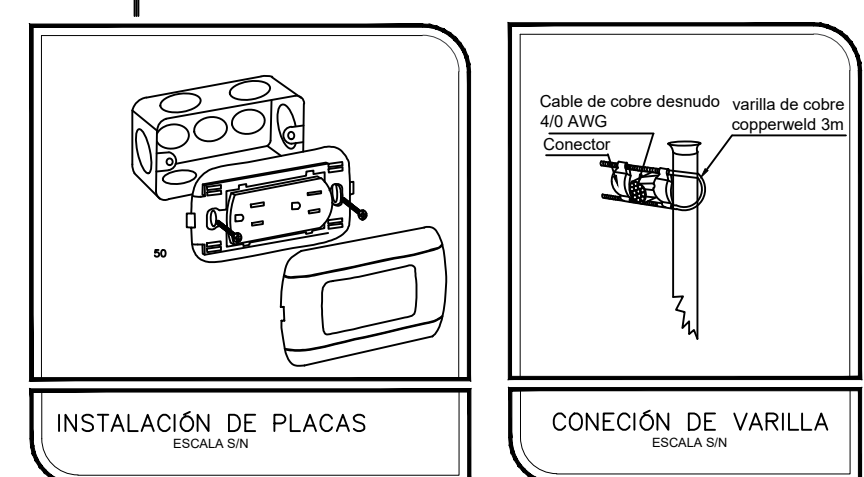
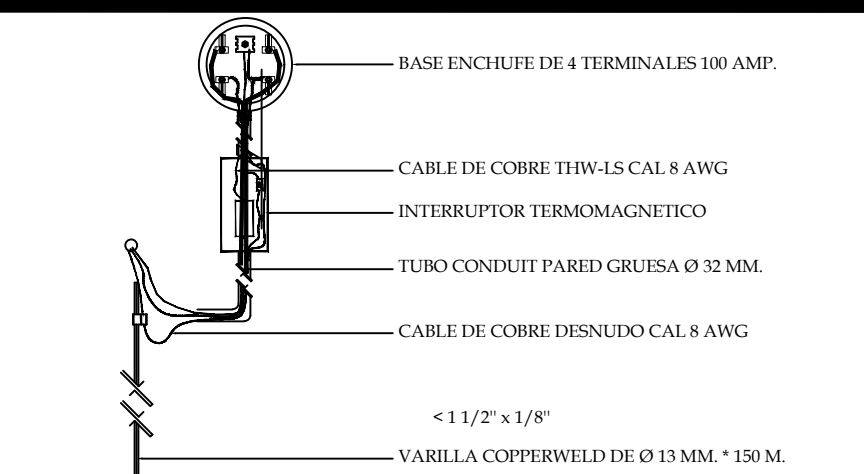
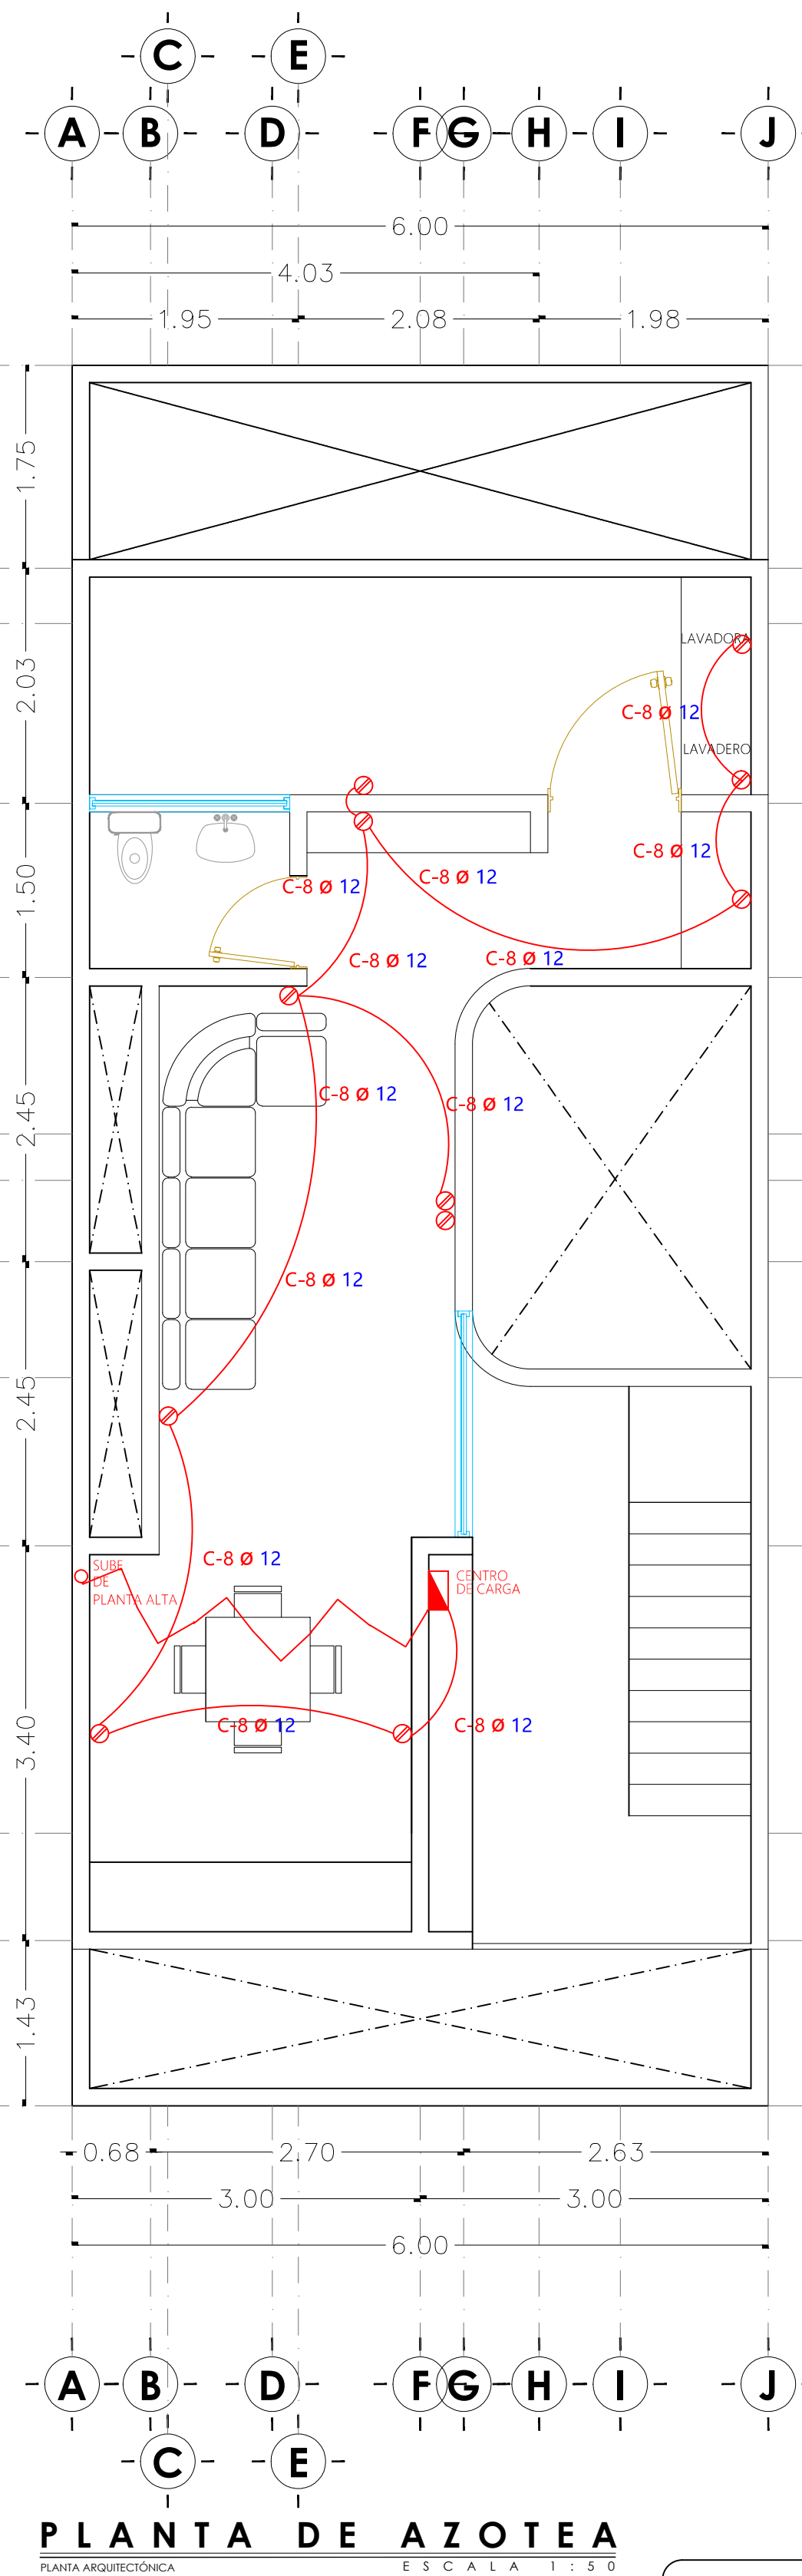
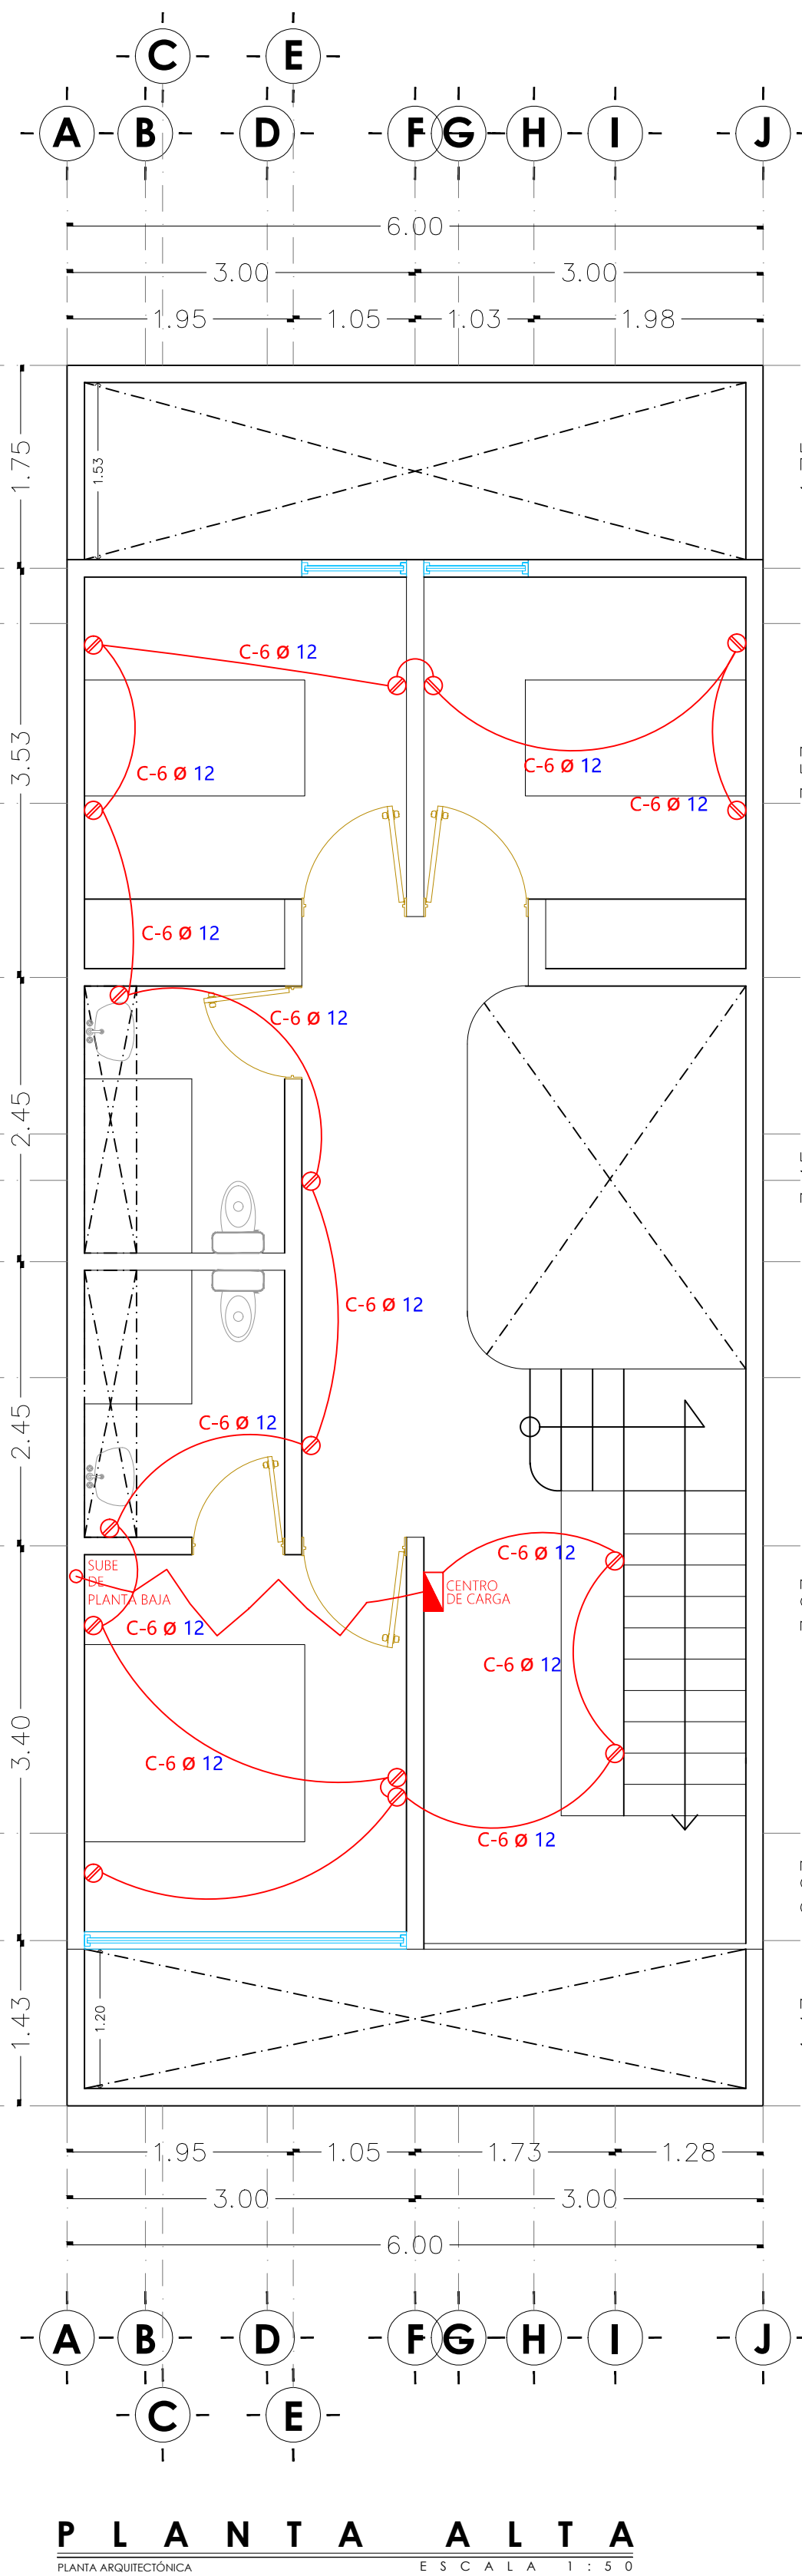
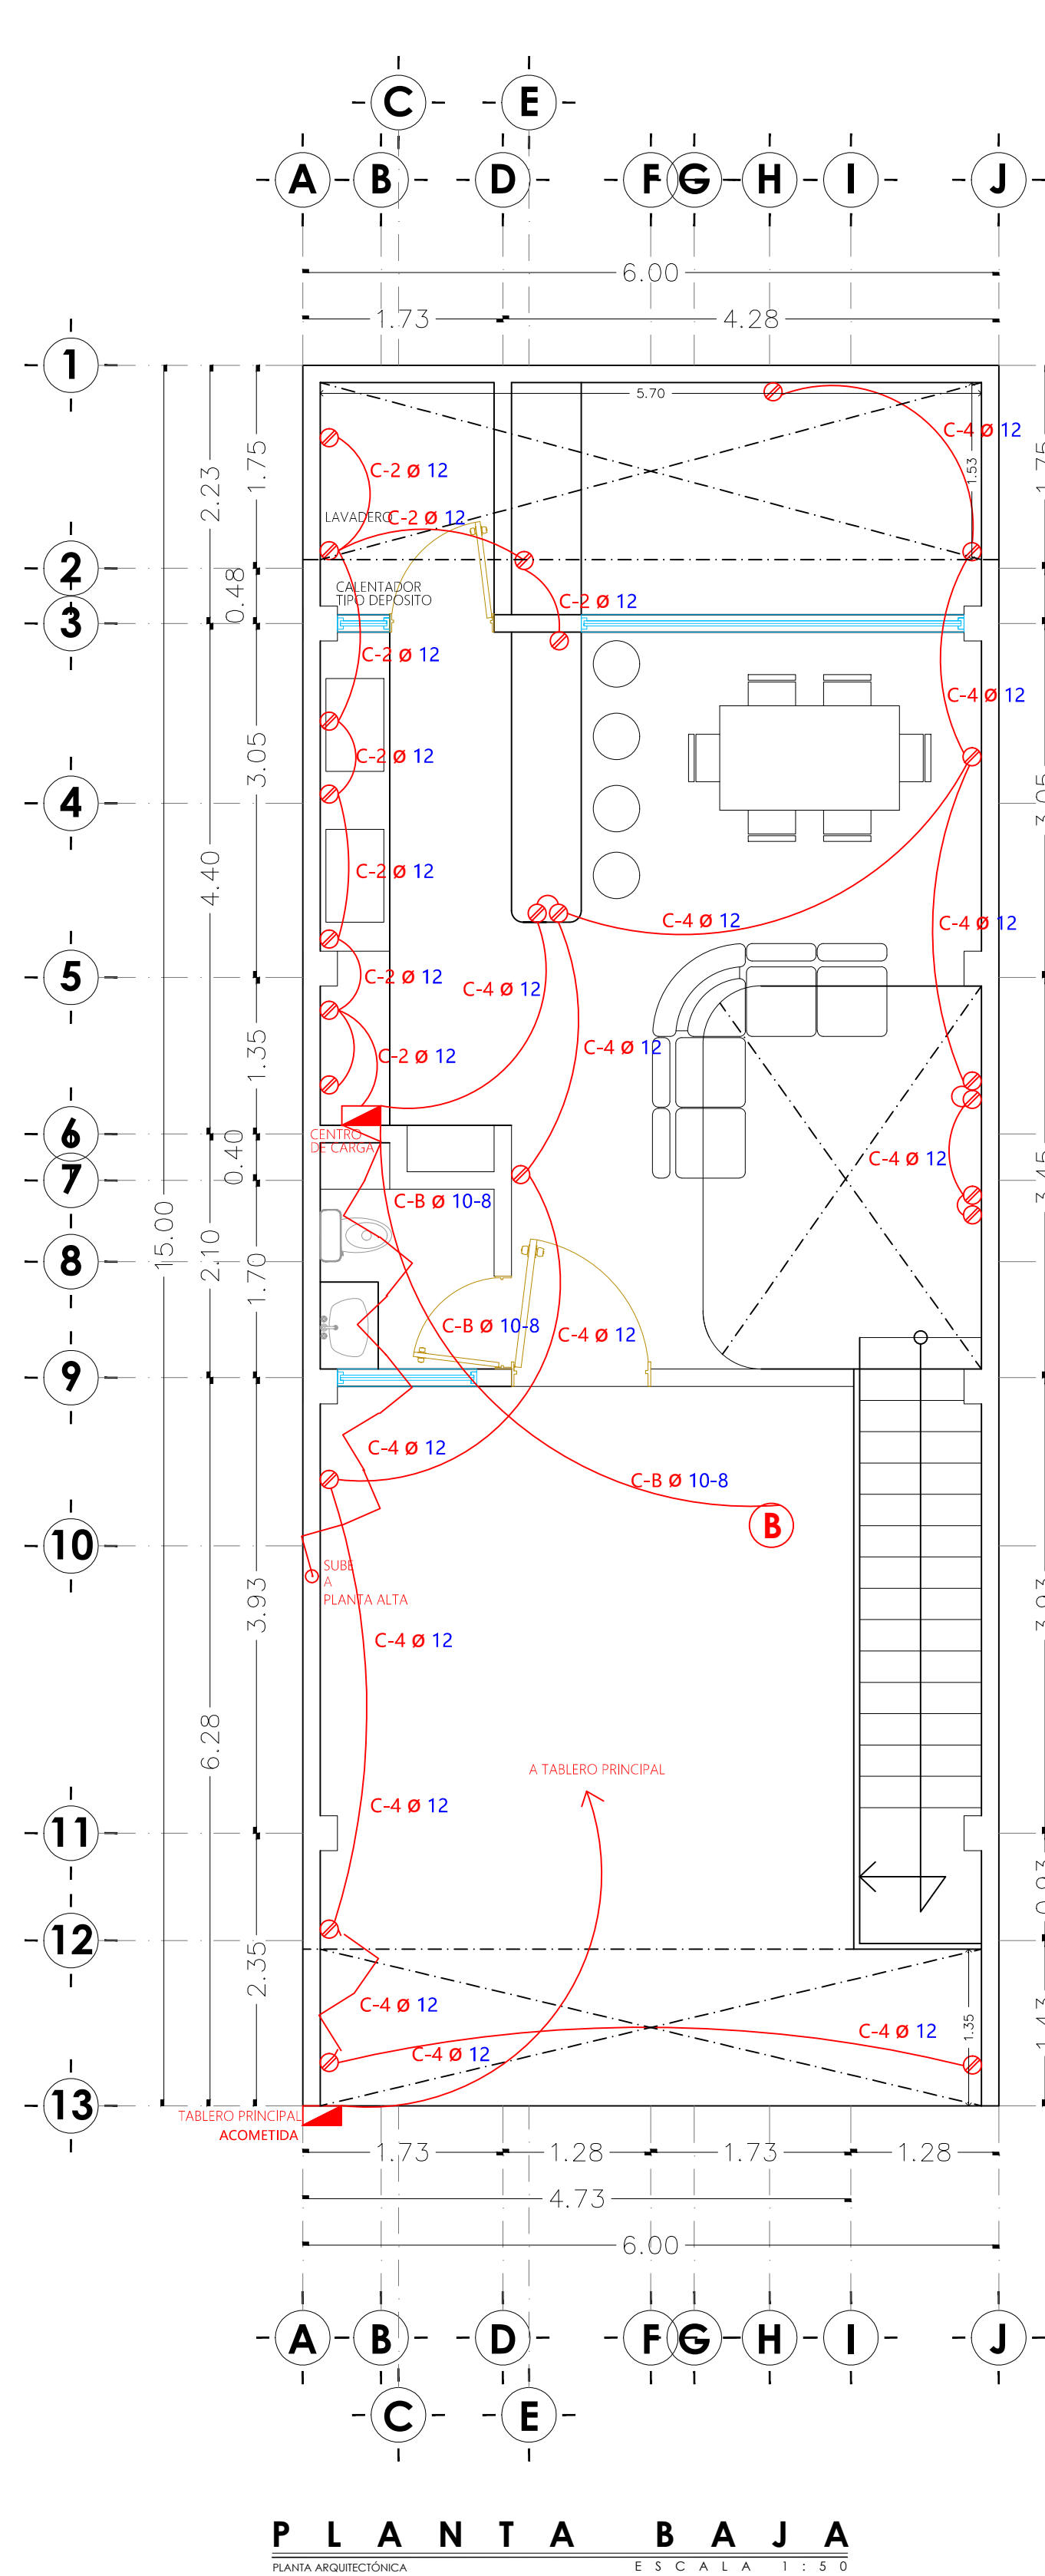
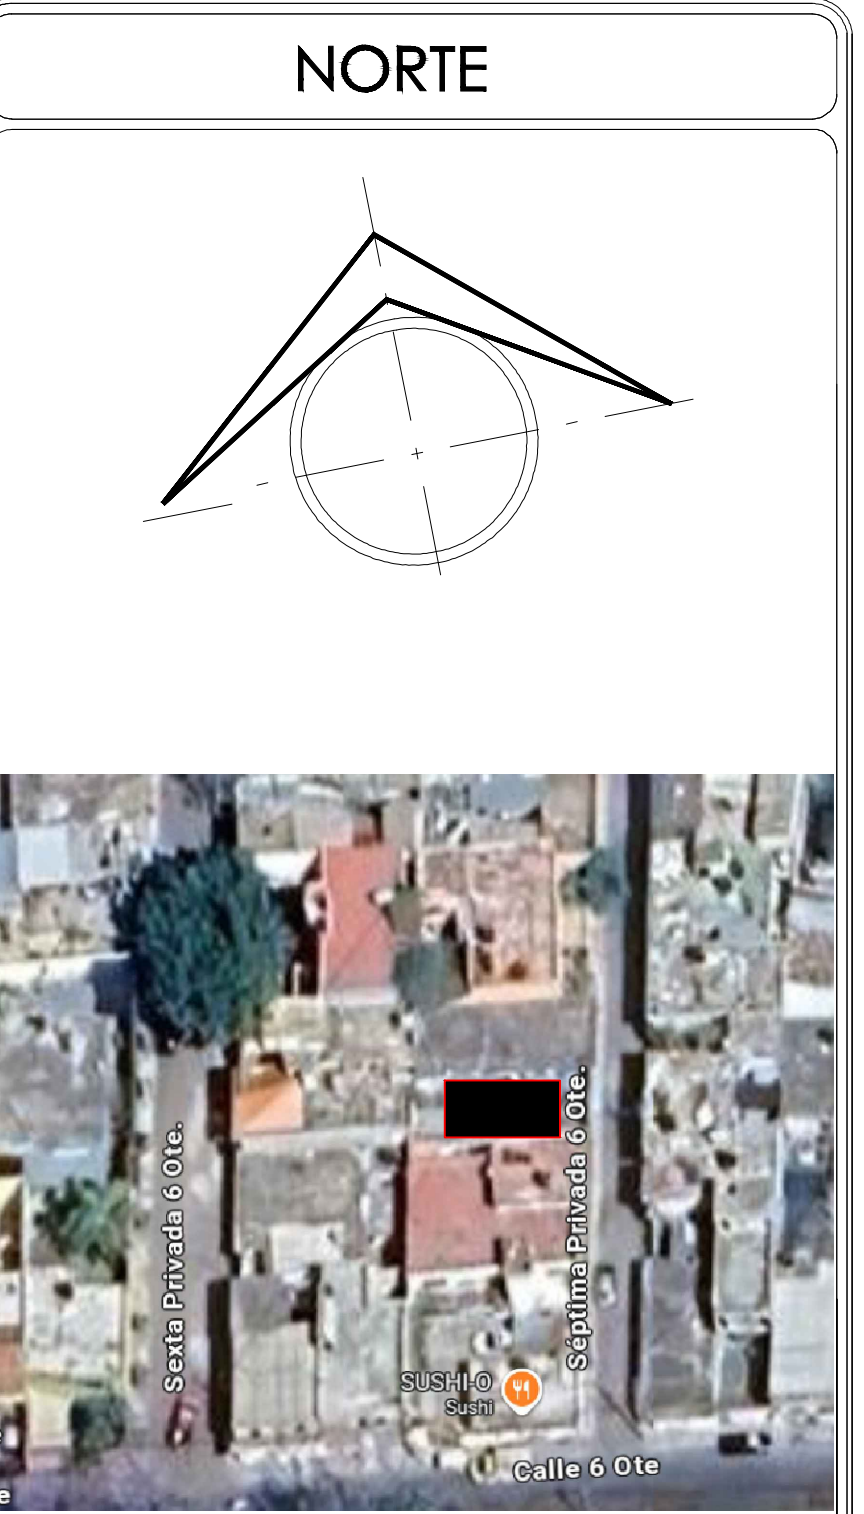


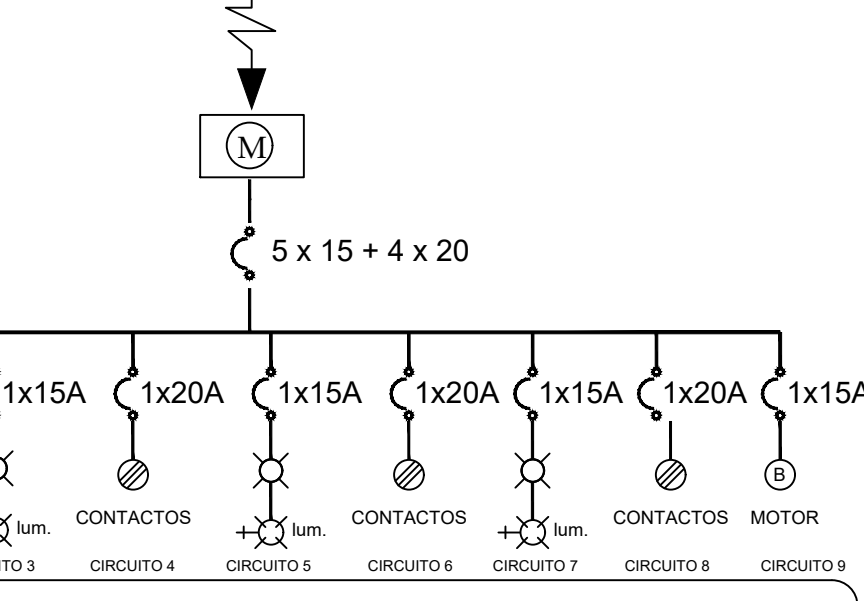

SIMBOLOGIA ELECTRICA	
	LAMPARA
	APAGADOR
	CONTACTO DUPLEX
	SAIDA T.V Y TELÉFONO
	APAGADOR DE ESCALERA
	ARBOTANTE
	FOCO SOBRE JARDINERA
	CENTRO DE CARGA
	MEDIDOR
	TIMBRE/ZUMBADOR
	ACOMETIDA
	BOMBA

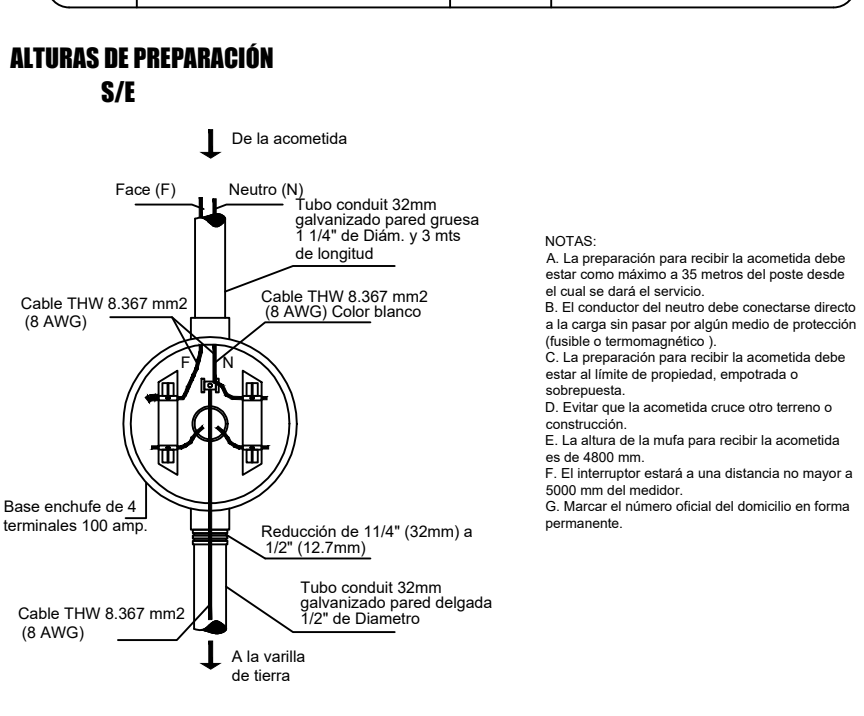

LOCALIZACION

SIMBOLOGIA:	
	ABERTURA PUERTA
	ABERTURA VENTANA
	PROYECCIONES
	SENTIDO DE ABERTURA
	CAMBIO DE NIVEL
	PROYECCIÓN DE VACIO
	LINEA DE CORTE

CUADRO DE CONSTRUCCIÓN POR NIVEL	
CONSTRUCCIÓN PLANTA BAJA	71.85 M2
CONSTRUCCIÓN PLANTA ALTA	71.85 M2
CONSTRUCCIÓN PLANTA DE AZOTEA	35.42 M2
TOTAL DE CONSTRUCCION	179.12 M2
AREA DEL TERRENO	90.00 M2

PROPIETARIO: ALEJANDRO CUEVAS VILLAGOMEZ

UBICACION: SEPTIMA PRIVADA DE LA 16 ORIENTE, NUMERO 605, LETRA A, COLONIA QUINTA GUADALUPE, TEHUACAN PUEBLA.

PROYECTO: HABITACIONAL

ESCALA: INDICADA


COTAS: METROS

PLANO: ELECTRICO CONTACTOS

FIRMA DEL D.R.O.:

FIRMA DEL PROPIETARIO:

FECHA: JUNIO 2026

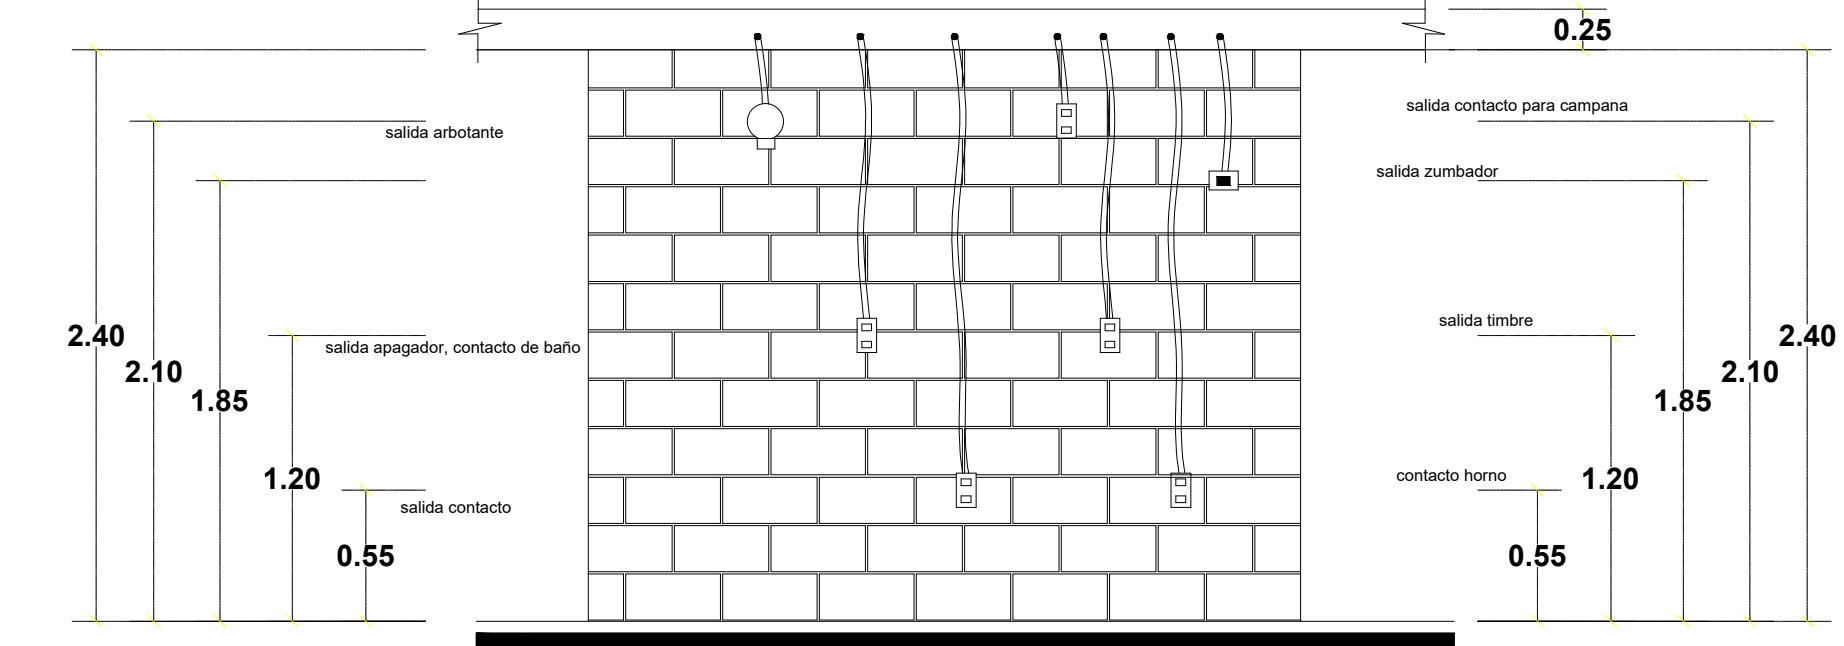

DETALLE DE ALTURA DE MONTAJES

ESPECIFICACIONES DE INSTALACIÓN ELÉCTRICA

- CONDUCTORES: SERÁN DE COBRE ELECTROLITICO (99.9 % DE CONDUCTIBILIDAD) CON AISLAMIENTO DE MATERIAL TERMOPLÁSTICO RESISTENTE A LA HUMEDAD Y RETARDANTE AL FUEGO; TIPO TW PARA CIRCUITOS DE ALUMBRADO Y DEL TIPO THW PARA TOMACORRIENTES Y ALIMENTADORES. SE UTILIZARÁ COMO MÍNIMO EL 2.5 MM. LOS CONDUCTORES TENDRÁN UN COLOR DIFERENTE PARA CADA FASE RESERVÁNDOSE EL COLOR VERDE, PARA EL SISTEMA DE TIERRA LOS CONDUCTORES SERÁN DEL TIPO CABLEADO.
- CAJAS: SERÁN DE F" "PESADO" (1.6mm DE ESPESOR DE PLANCHA MÍNIMO).
- TABLEROS: EMPOTRADOS, DE F" "PESADO, CON DISTRIBUCIÓN BIFÁSICA, CON INTERRUPTORES AUTOMÁTICOS DEL TIPO NO USE TERMOMAGNETICOS, DIMENSIONES DE CAJA SEGUN FABRICANTE.
- PUESTA DE TIERRA: SEGUN DETALLE.
- LAS ALTURAS INDICADAS EN LA LEYENDA SON REFERENCIALES, EN OBRA EL CONTRATISTA COORDINARA LAS ALTURAS DEFINITIVAS CON EL PROFESIONAL RESPONSABLE.
- LA TUBERÍA QUE ATRAVIESE EL TERRENO SIN PAVIMENTADO (JARDIN) SERA PROTEGIDA POR UN DADO DE CONCRETO DE 0.10x0.10 m. EN TODA SU LONGITUD Y A 0.40 m. DE PROFUNDIDAD.
- INTERRUPTORES DIFERENCIALES: DISPOSITIVO QUE DETECTA "CORRIENTES DE FUGA" CON EL FIN DE PROTEGER A LAS PERSONAS CONTRA LOS RIESGOS DE ELECTROCUCION(EN BAJA TENSION) COMO CONSECUENCIA DE CONTACTOS DIRECTOS O INDIRECTOS, INSTALADOS "AGUAS ABAJO DE UN INTERRUPTOR TERMOMAGNETICO", (ASEGURA EL SECCIONAMIENTO AUTOMATICO DE UN CIRCUITO EN CASO DE FALLA DE AISLAMIENTO ENTRE FASE Y TIERRA) DEBERA ESTAR PROTEGIDO CONTRA LOS DISPAROS INTENPSTIVOS DEBIDO A SOBRETENSIONES PASAJERAS (MANIOBRAS DE EQUIPAMIENTO EN LA RED) PREPARADO PARA OPERAR A UNA TENSION NOMINAL DE 220V- 25 A , CON UNA SENSIBILIDAD NO MAYOR A 30 Ma.

CUADRO DE CARGA POR CIRCUITO

CARGA	13 W	25 W	75 W	13 W	180 W	1 HP(750)	TOTAL WATTS
C-1	-	13	1	-	-	-	400
C-2	-	-	-	-	9	-	1620
C-3	-	7	2	-	-	-	325
C-4	-	-	-	-	14	-	2,520
C-5	-	15	2	-	-	-	525
C-6	-	-	-	-	16	-	2,880
C-7	-	10	5	-	-	-	625
C-8	-	-	-	-	11	-	1,980
C-9-B	-	-	-	-	-	1	750
TOTAL	-	45	10	-	50	1	11,625