
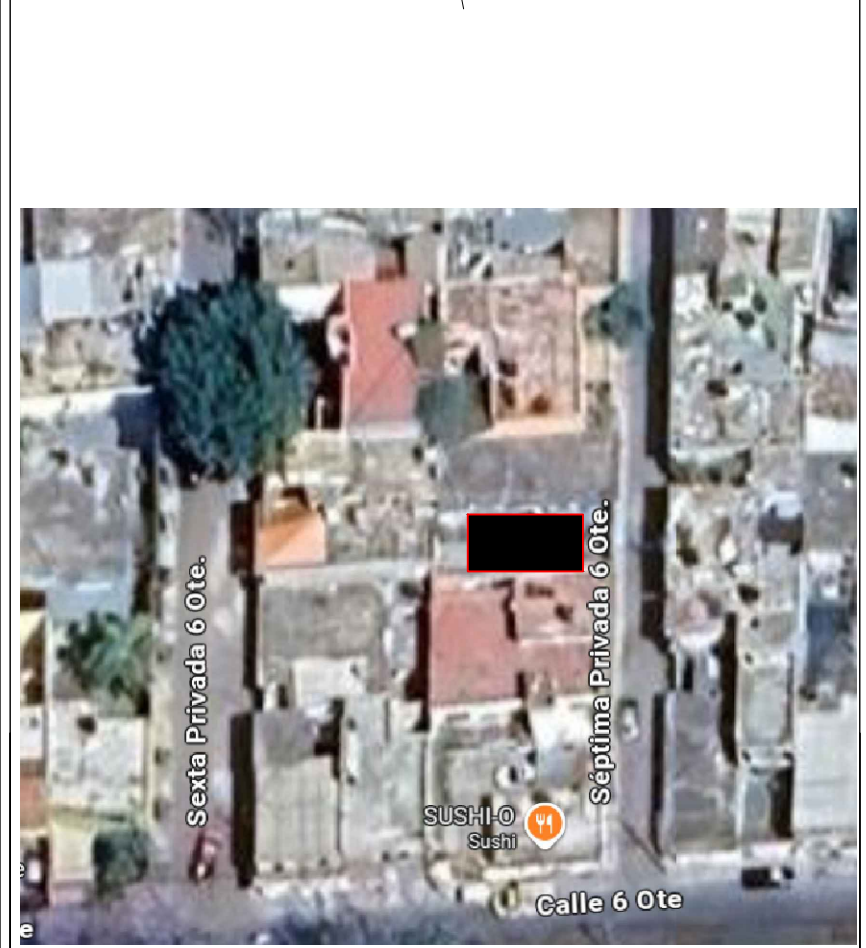
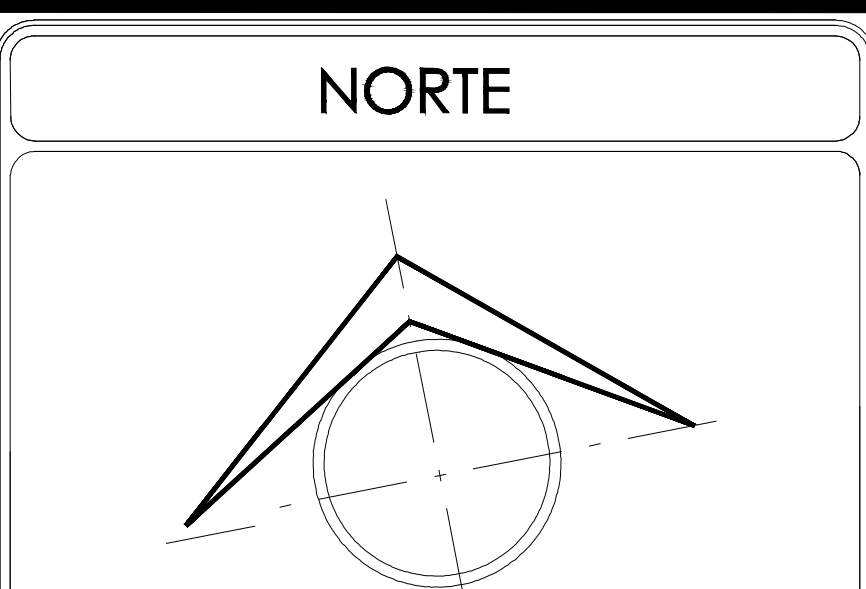
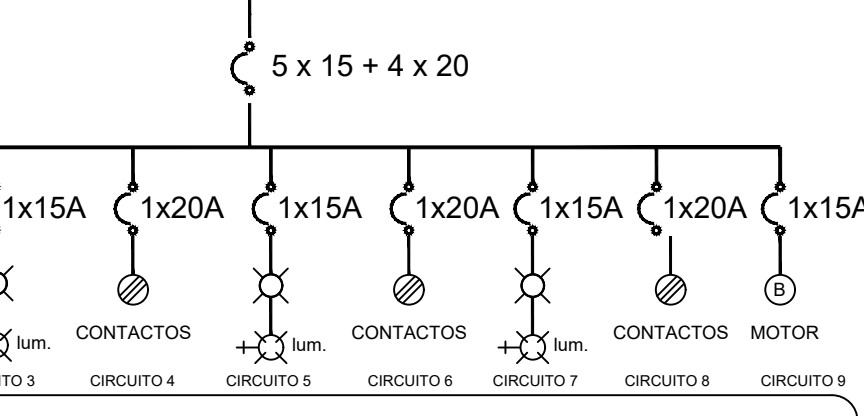
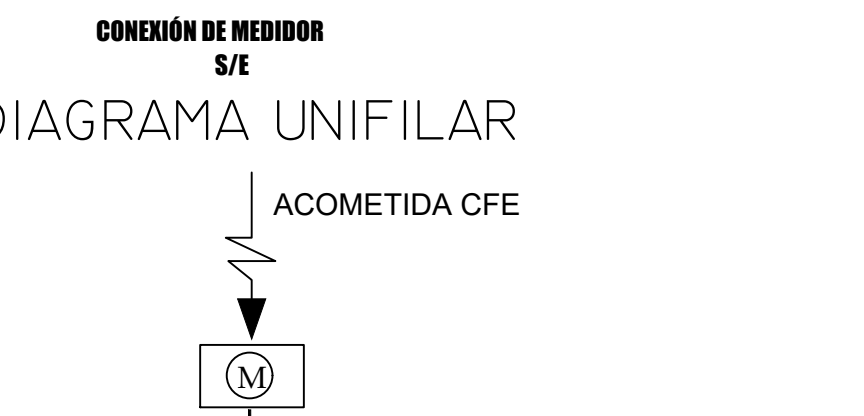
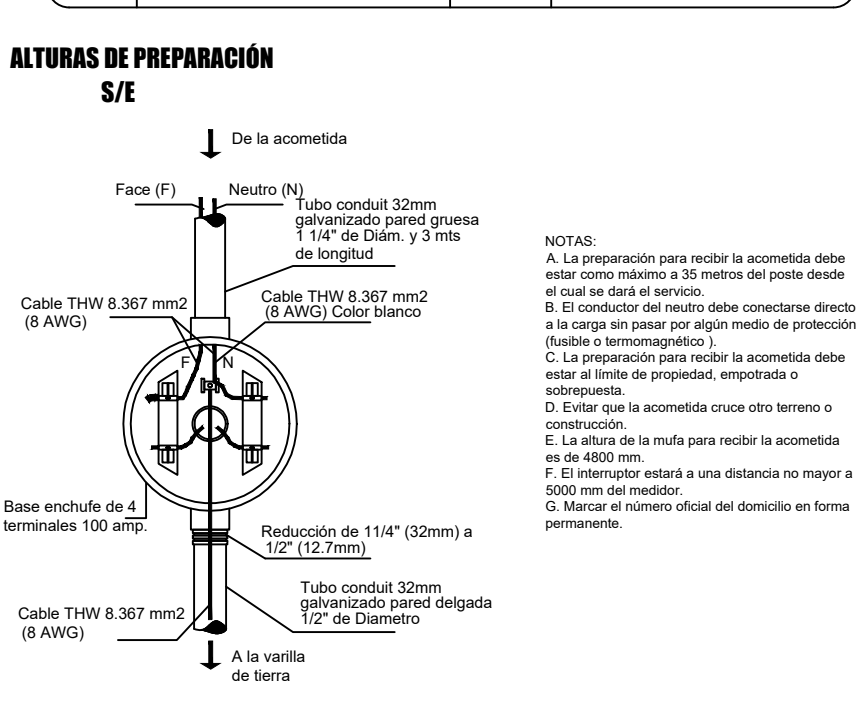
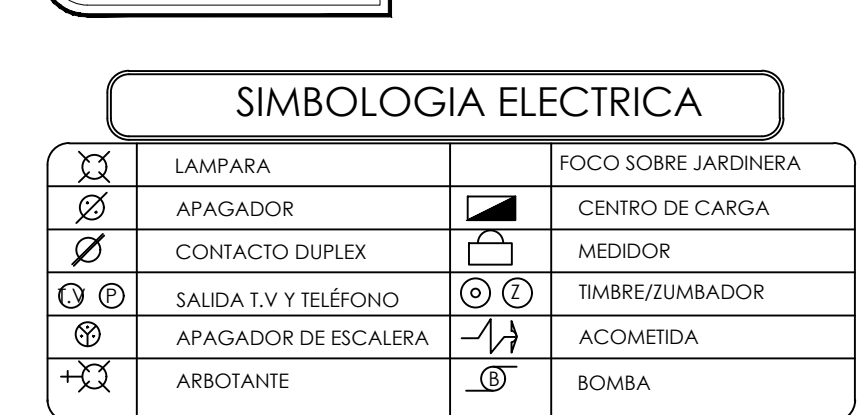
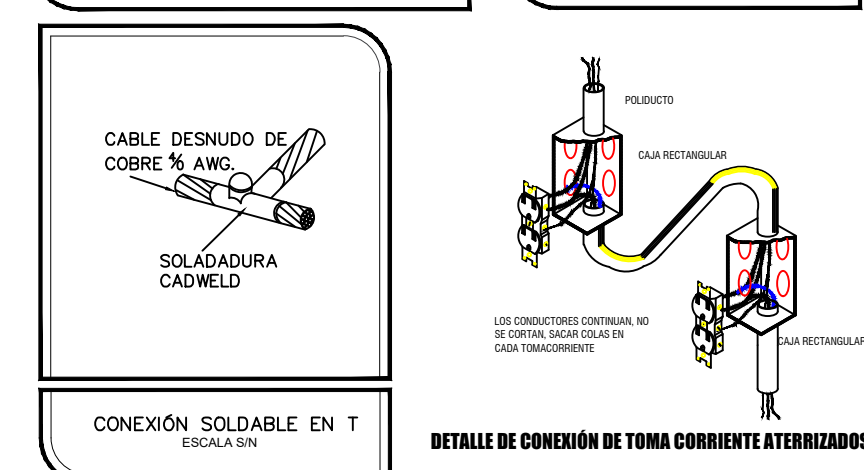
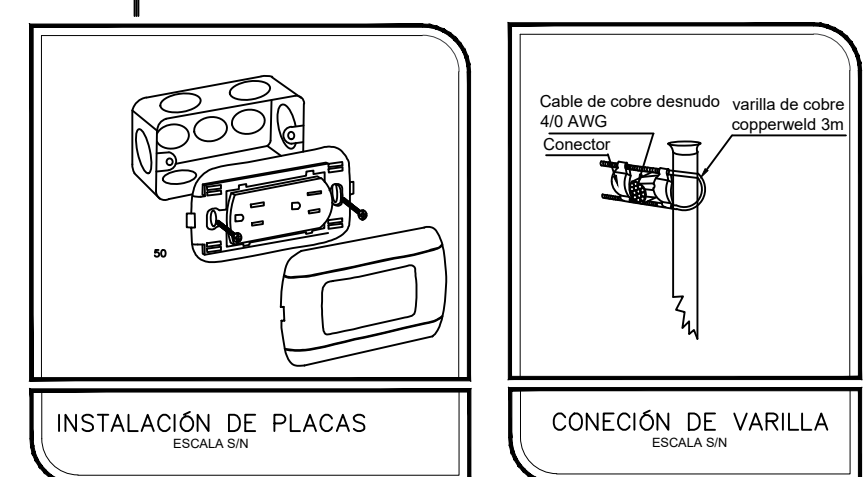
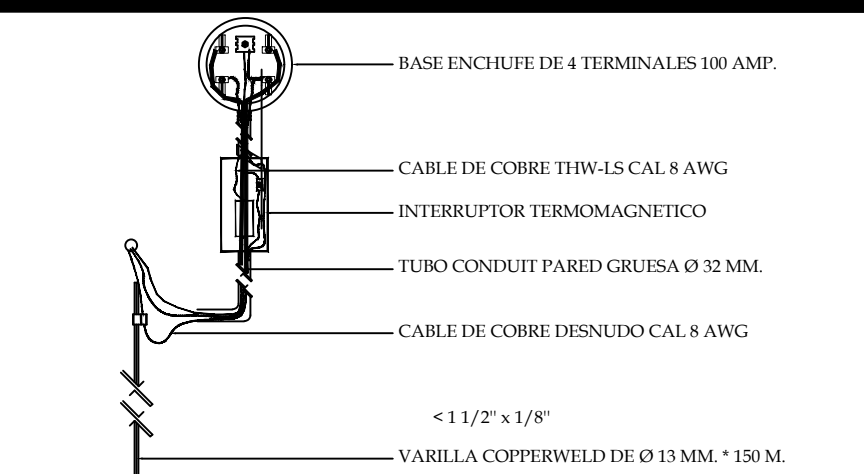
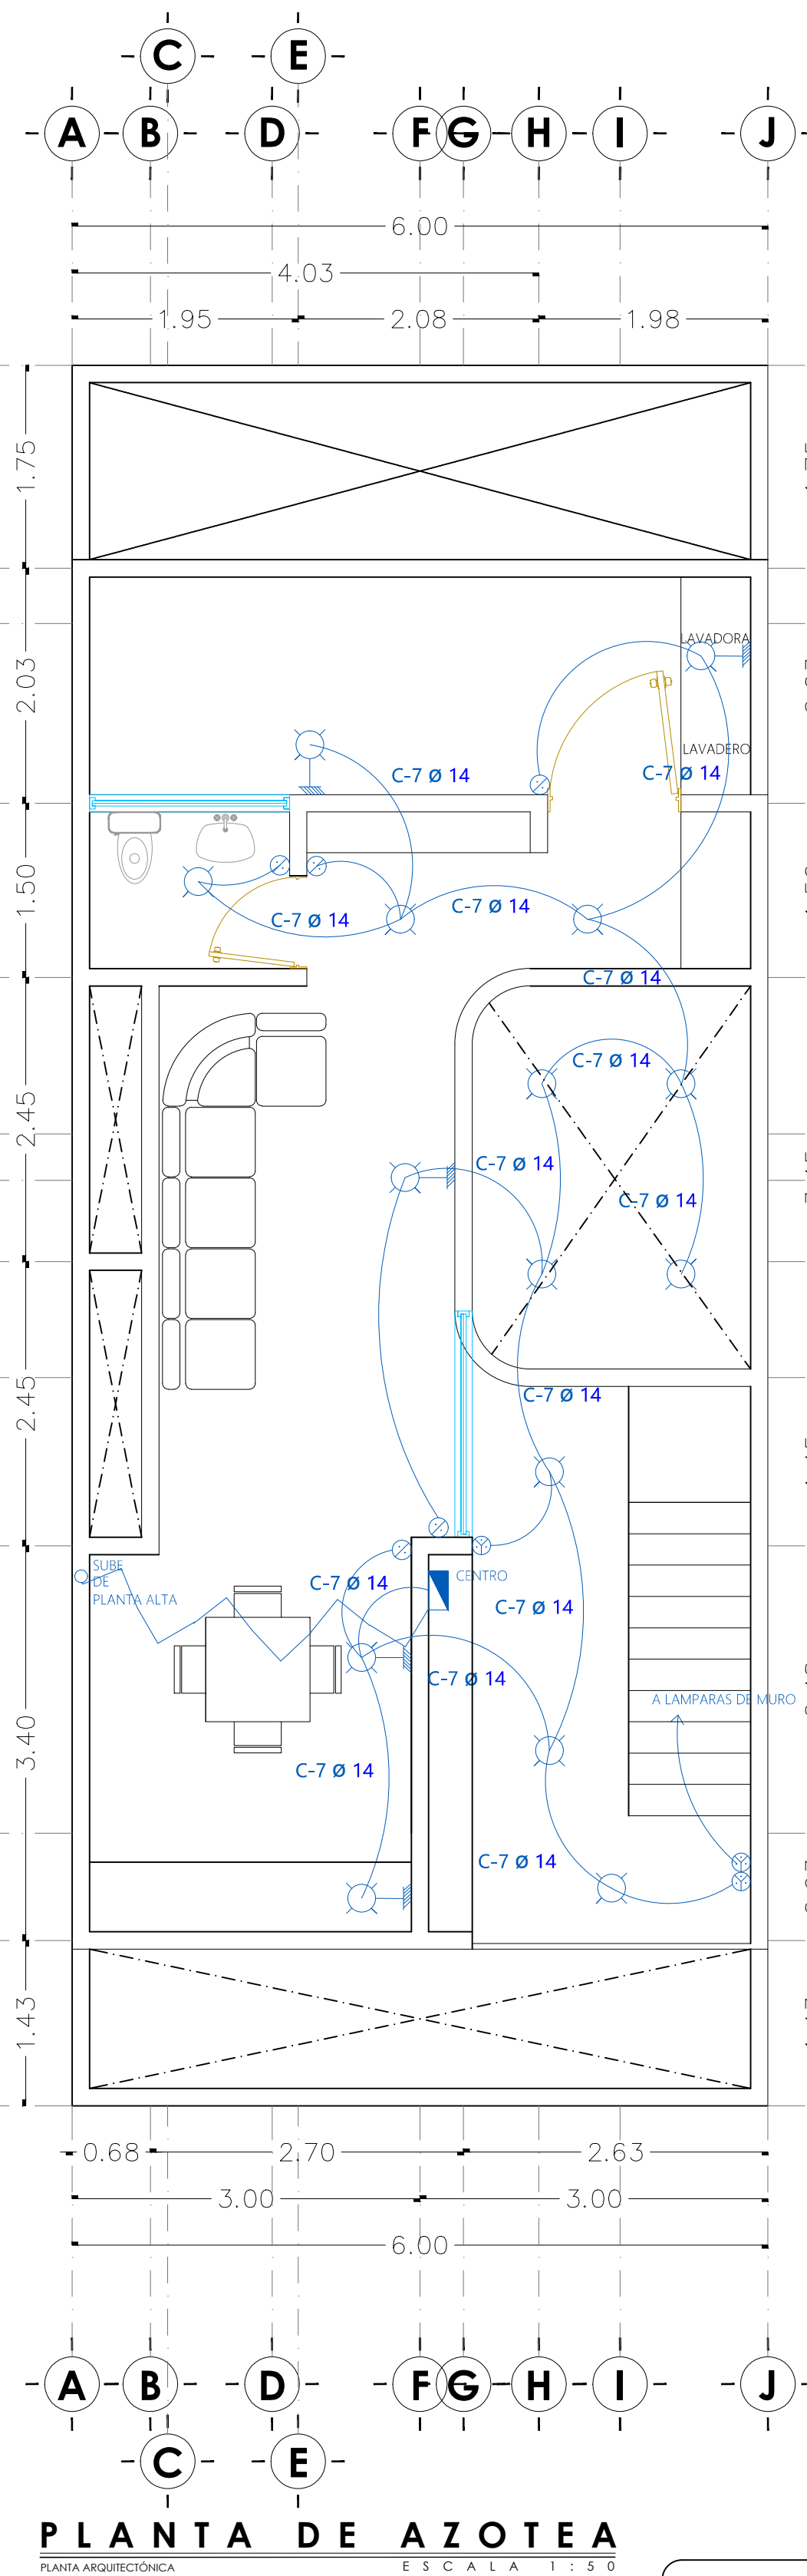
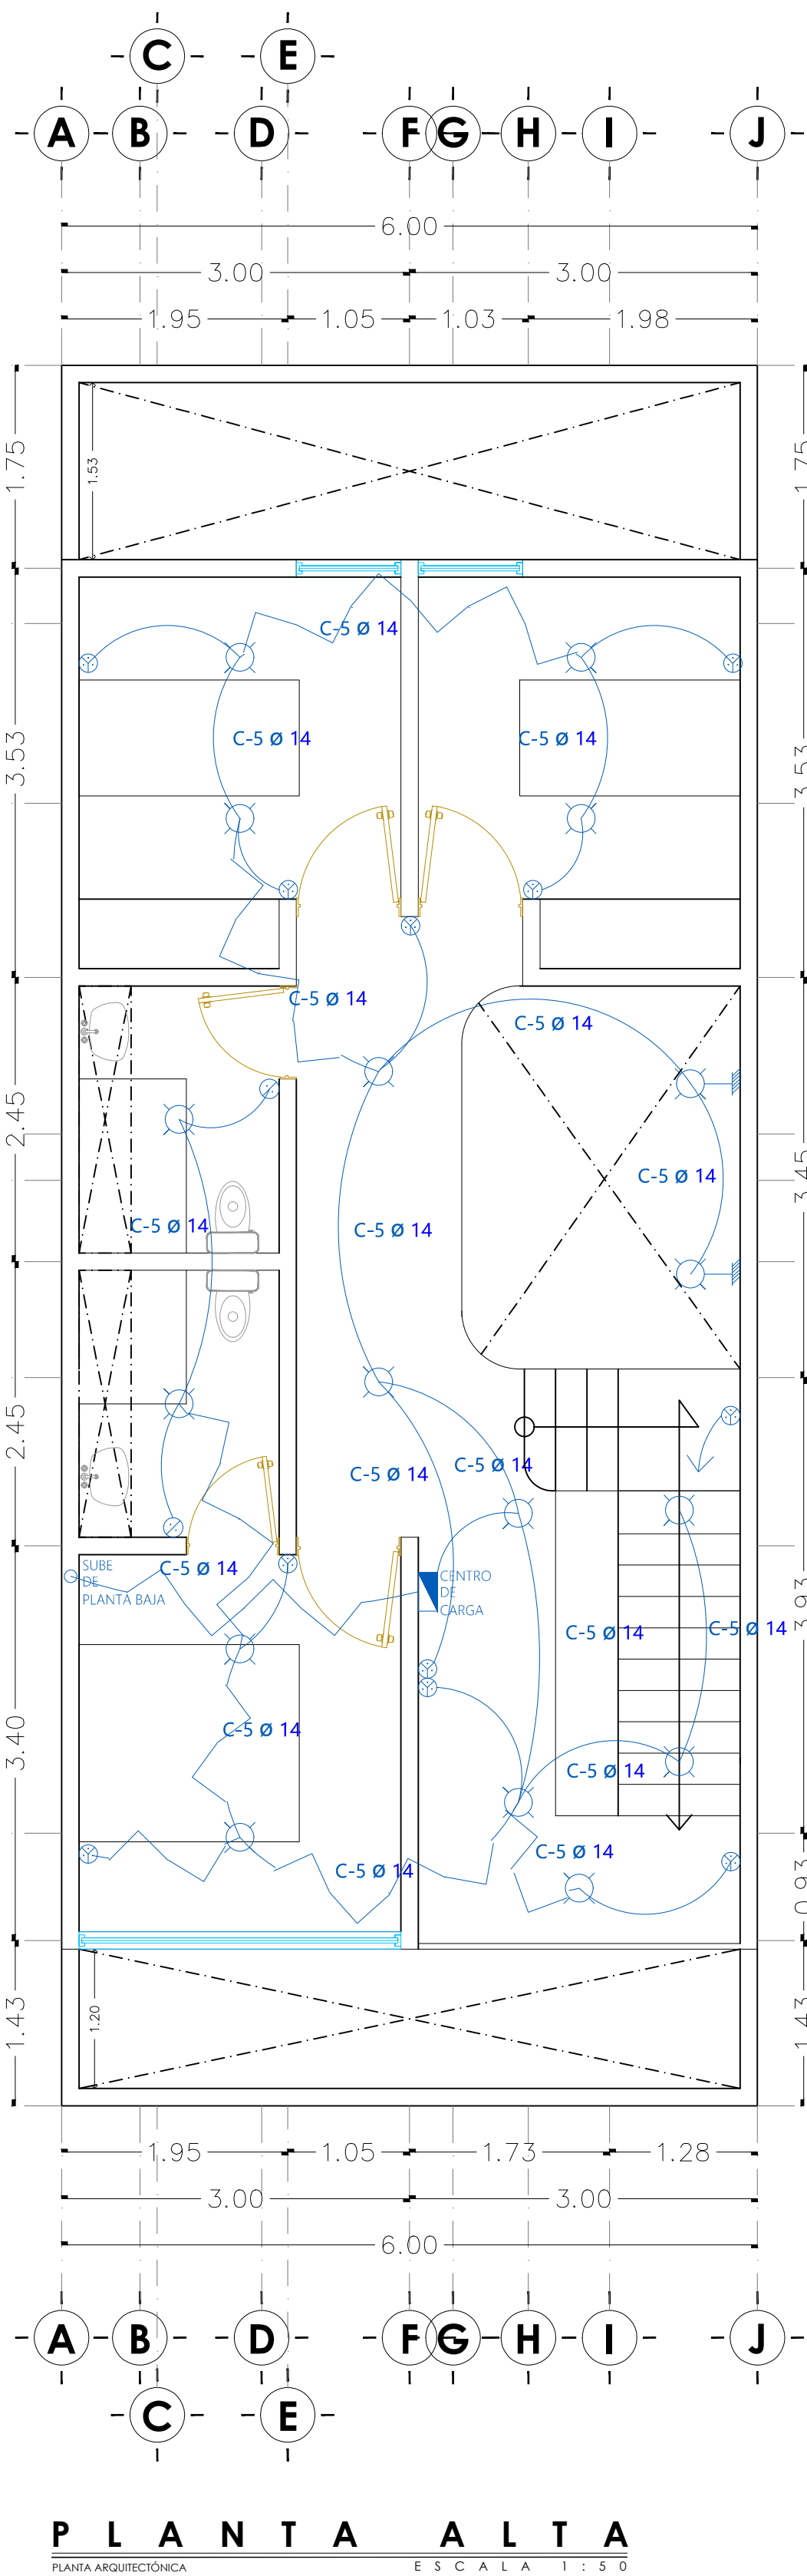


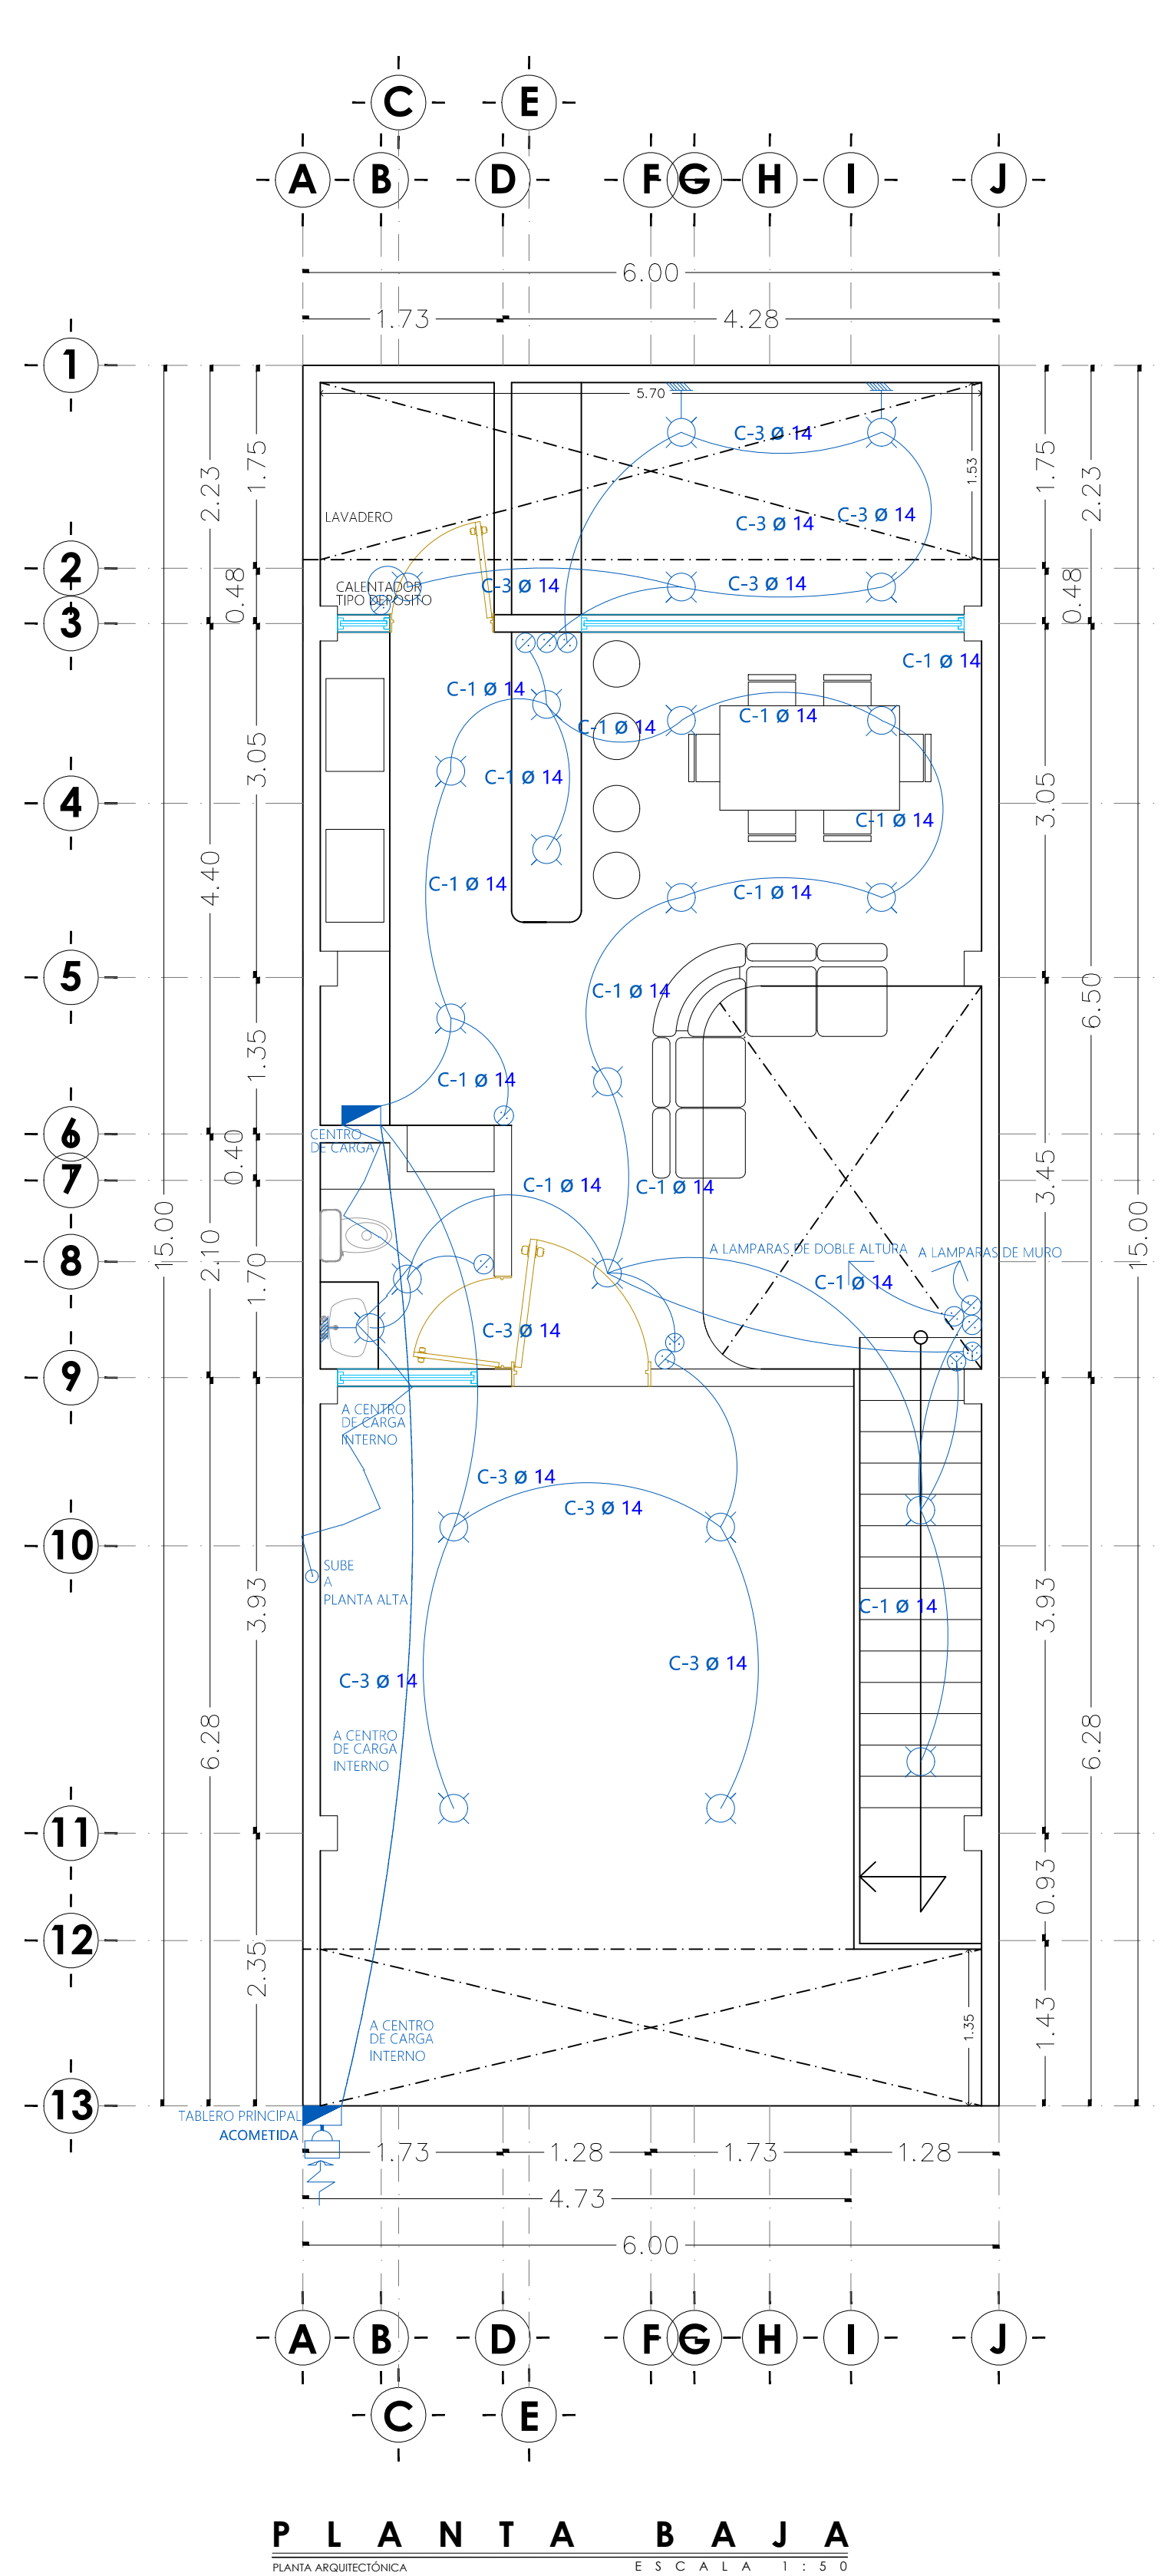

LOCALIZACIÓN

Septima Privada 606

Septima Privada 606

Calle 606

LOCALIZACIÓN

Septima Privada 606

Septima Privada 606

Calle 606

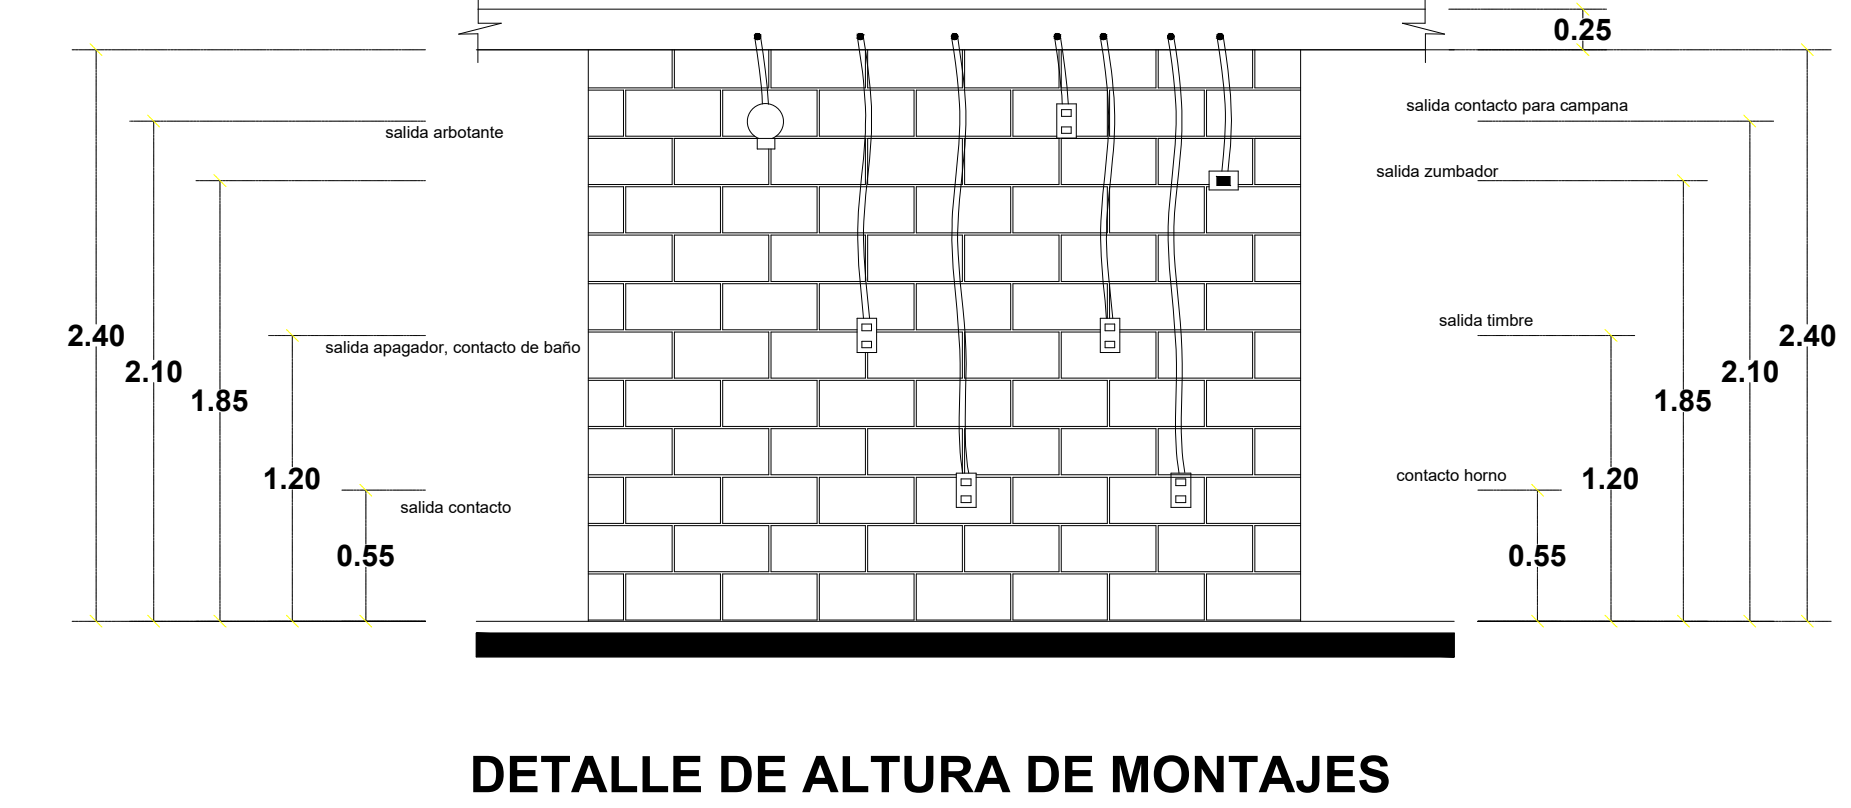

ESPECIFICACIONES DE INSTALACIÓN ELÉCTRICA

- CONDUCTORES: SERÁN DE COBRE ELECTROLÍTICO (99.9 % DE CONDUCTIBILIDAD) CON AISLAMIENTO DE MATERIAL TERMOPLÁSTICO RESISTENTE A LA HUMEDAD Y RETARDANTE AL FUEGO; TIPO TW PARA CIRCUITOS DE ALUMBRADO Y DEL TIPO THW PARA TOMACORRIENTES Y ALIMENTADORES. SE UTILIZARÁ COMO MÍNIMO EL 2.5 MM. LOS CONDUCTORES TENDRÁN UN COLOR DIFERENTE PARA CADA FASE RESERVÁNDOSE EL COLOR VERDE, PARA EL SISTEMA DE TIERRA LOS CONDUCTORES SERÁN DEL TIPO CABLEADO.
- CAJAS: SERÁN DE F" "PESADO" (1.6mm DE ESPESOR DE PLANCHA MÍNIMO).
- TABLEROS: EMPOTRADOS, DE F" "PESADO, CON DISTRIBUCIÓN BIFÁSICA, CON INTERRUPTORES AUTOMÁTICOS DEL TIPO NO USE TERMOMAGNETICOS, DIMENSIONES DE CAJA SEGUN FABRICANTE.
- PUESTA DE TIERRA: SEGUN DETALLE.
- LAS ALTURAS INDICADAS EN LA LEYENDA SON REFERENCIALES, EN OBRA EL CONTRATISTA COORDINAR LAS ALTURAS DEFINITIVAS CON EL PROFESIONAL RESPONSABLE.
- LA TUBERÍA QUE ATRAVIESE EL TERRENO SIN PAVIMENTADO (JARDIN) SERA PROTEGIDA POR UN DADO DE CONCRETO DE 0.10x0.10 m. EN TODA SU LONGITUD Y A 0.40 m. DE PROFUNDIDAD.
- INTERRUPTORES DIFERENCIALES: DISPOSITIVO QUE DETECTA "CORRIENTES DE FUGA" CON EL FIN DE PROTEGER A LAS PERSONAS CONTRA LOS RIESGOS DE ELECTROCUCIÓN(EN BAJA TENSION) COMO CONSECUENCIA DE CONTACTOS DIRECTOS O INDIRECTOS, INSTALADOS "AGUAS ABAJO DE UN INTERRUPTOR TERMOMAGNETICO", (ASEGURA EL SECCIONAMIENTO AUTOMATICO DE UN CIRCUITO EN CASO DE FALLA DE AISLAMIENTO ENTRE FASE Y TIERRA) DEBERA ESTAR PROTEGIDO CONTRA LOS DISPAROS INTENESTIVOS DEBIDO A SOBRETENSIONES PASAJERAS (MANIOBRAS DE EQUIPAMIENTO EN LA RED) PREPARADO PARA OPERAR A UNA TENSION NOMINAL DE 220V- 25 A , CON UNA SENSIBILIDAD NO MAYOR A 30 Ma.

CUADRO DE CARGA POR CIRCUITO

CARGA	13 W	25 W	75 W	13 W	180 W	1 HP(750)	TOTAL WATTS
C-1	-	13	1	-	-	-	400
C-2	-	-	-	-	9	-	1620
C-3	-	7	2	-	-	-	325
C-4	-	-	-	-	14	-	2,520
C-5	-	15	2	-	-	-	525
C-6	-	-	-	-	16	-	2,880
C-7	-	10	5	-	-	-	625
C-8	-	-	-	-	11	-	1,980
C-9-B	-	-	-	-	-	1	750
TOTAL	-	45	10	-	50	1	11,625