




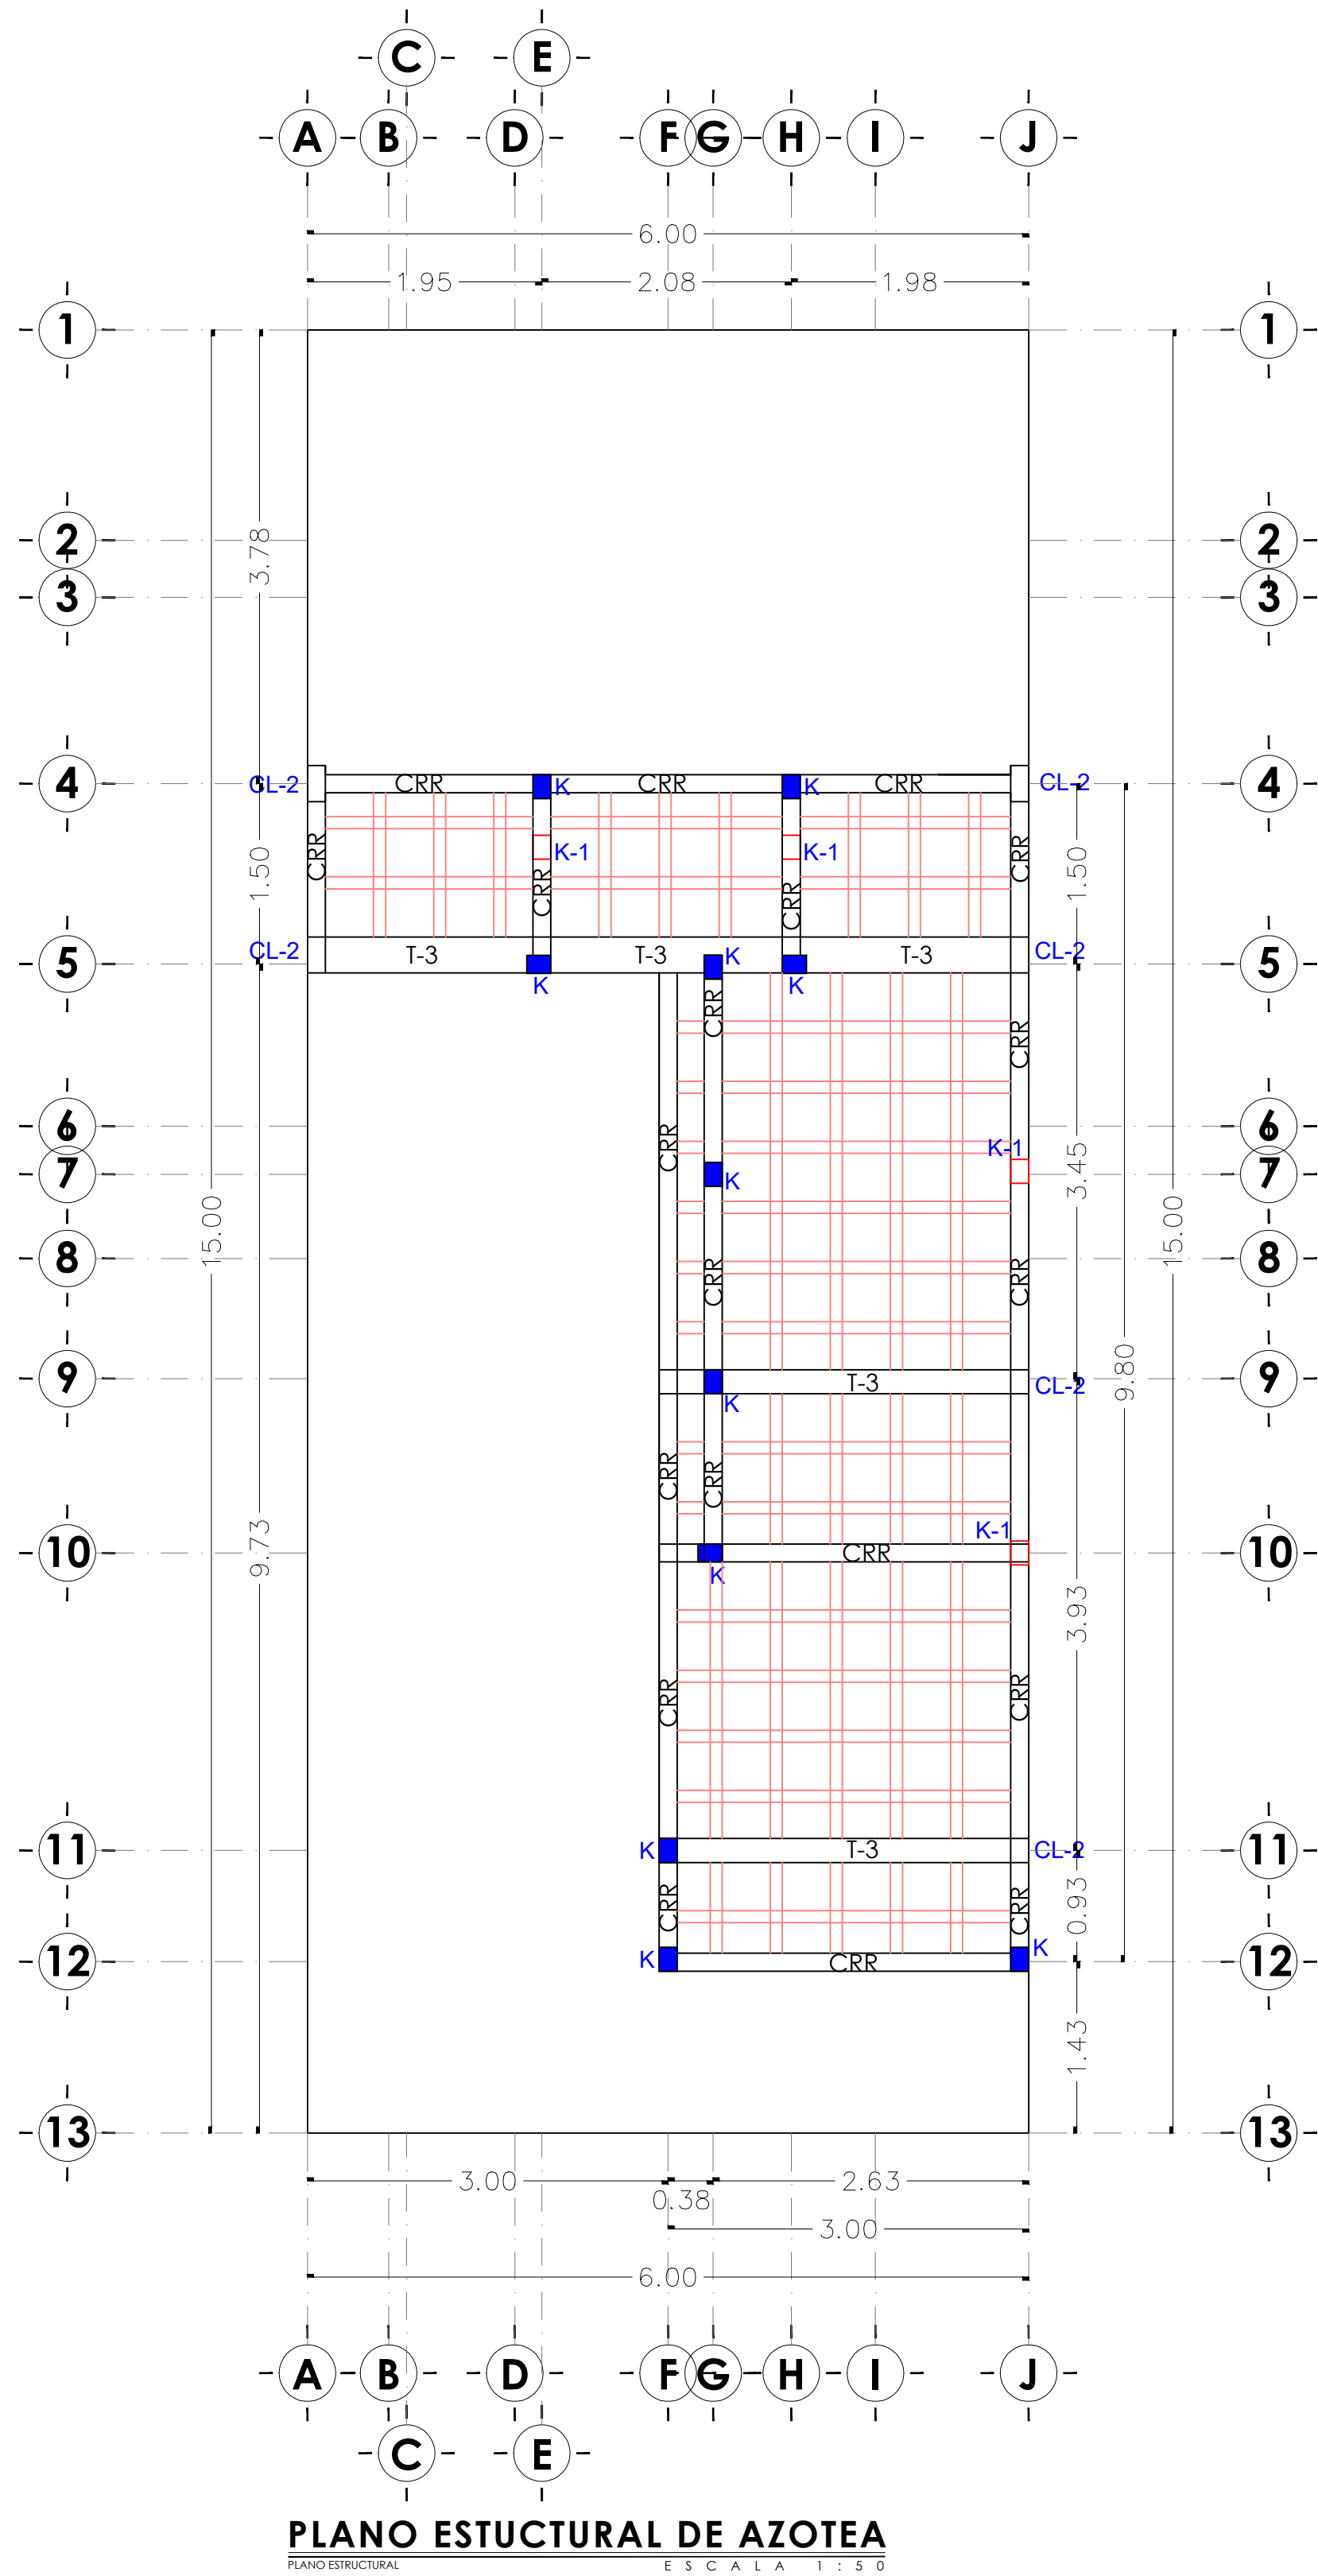


ZAPATA AISLADA Z-2

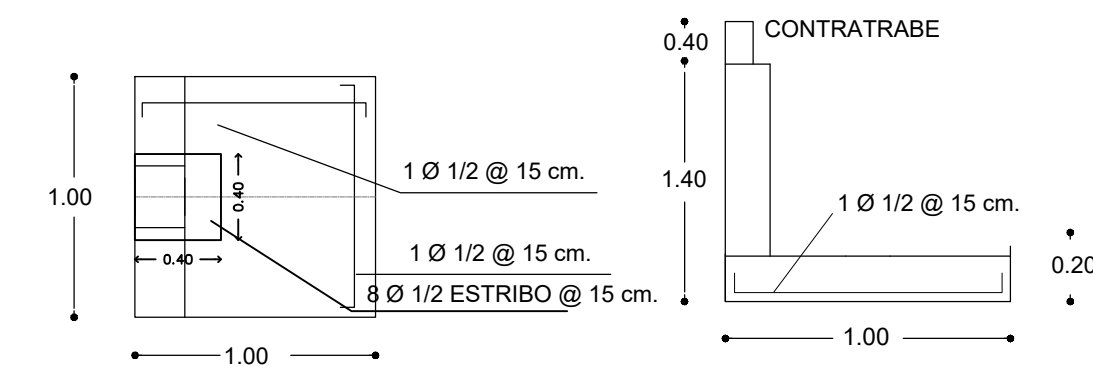


ZAPATA AISLADA Z-1

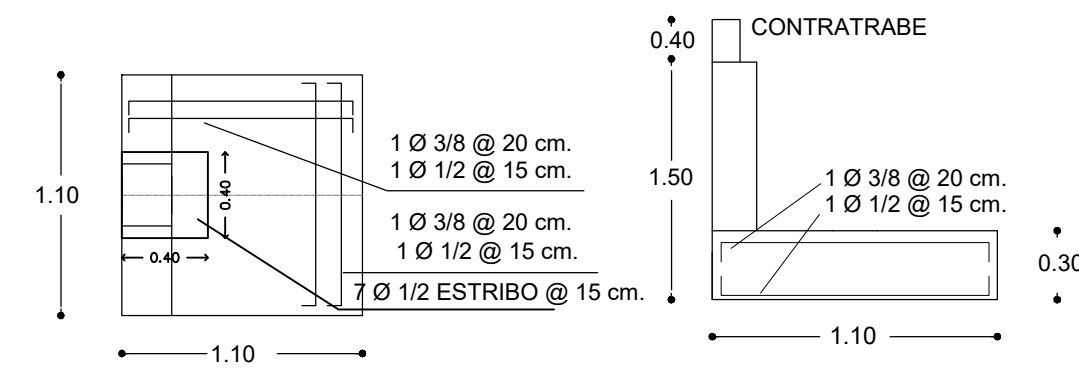


CONTRA TRABE (CT-1)

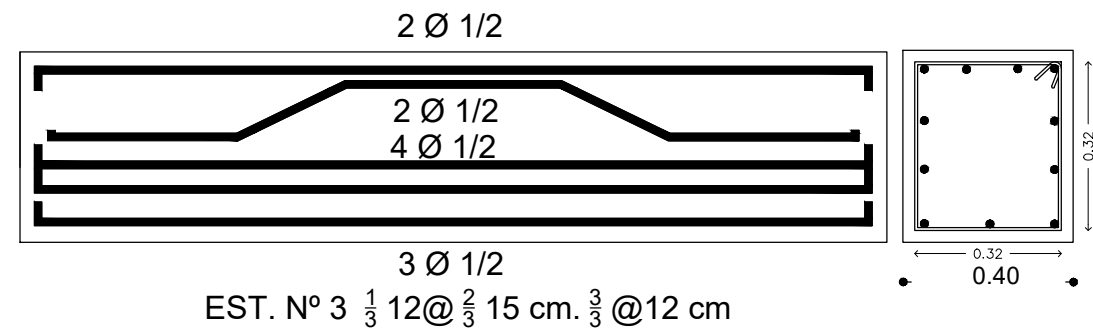


CONTRA TRABE (CT-2)

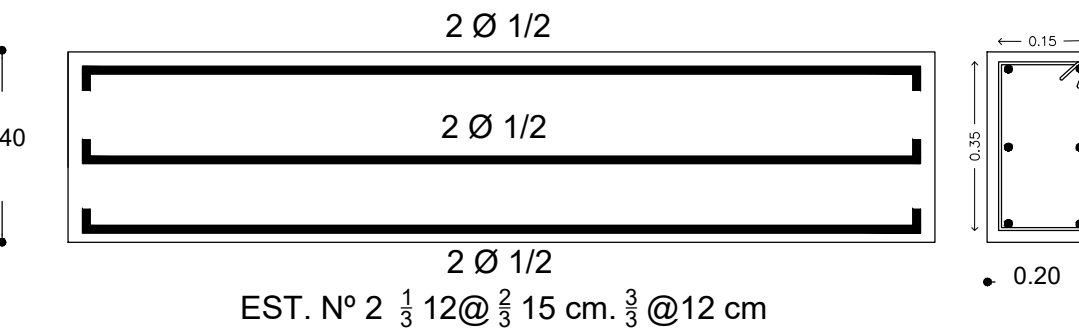


TRABE 1 (T-1)

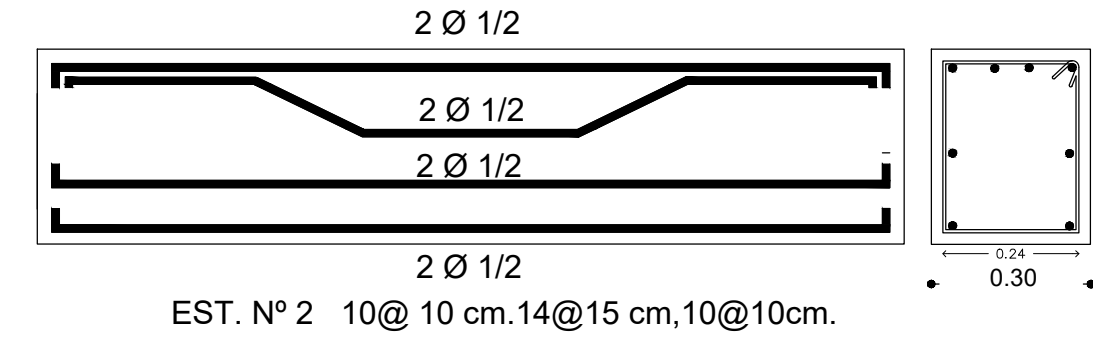


TRABE 2 (T-2)

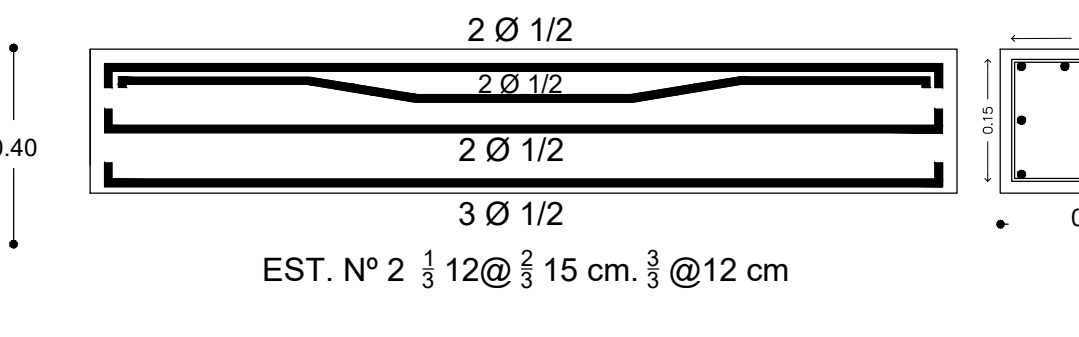


COLUMNA CL

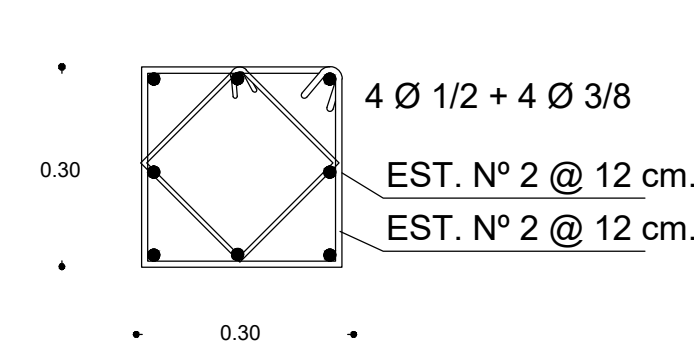


CL-2

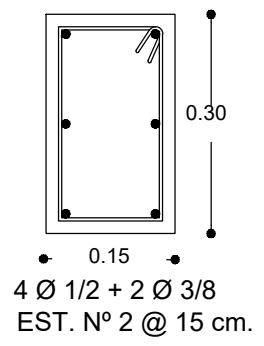


K

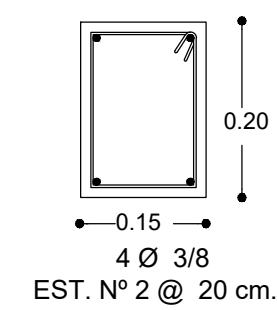


K-1

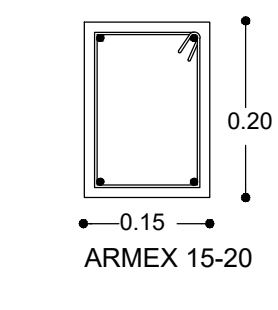

CD.

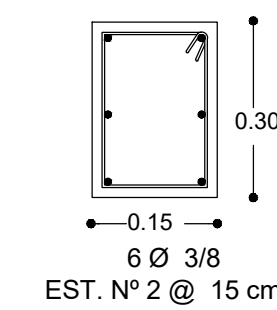

CRR

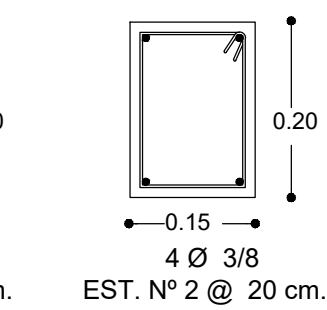


1 Ø 3/8 @ 13, AMBOS SENTIDOS
3 Ø 1/2
2 Ø 3/8
3 Ø 1/2

3 Ø 1/2
2 Ø 3/8
2 Ø 1/2
NIVEL DE PISO TERMINADO
CADENA DE ANCLADO

DETALLE DE ARMADO DE ESCALERA



TRABE 3 (T-3)

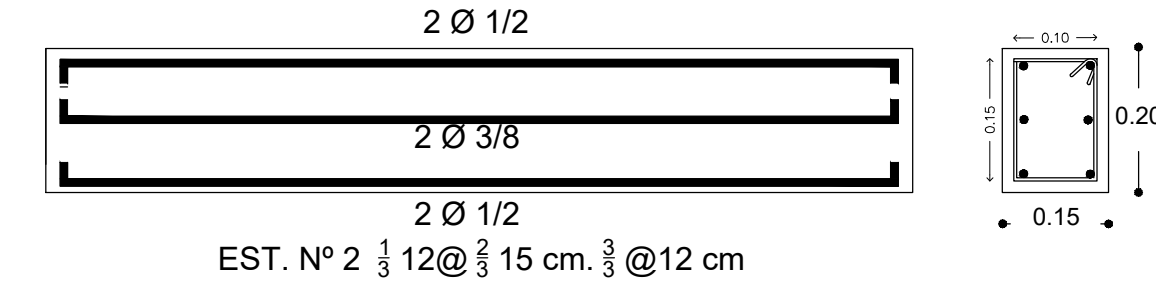

ESPECIFICACIONES

- PARA LOS DUCTOS E INSTALACIONES QUE DEBERAN QUEDAR EMBEBIDOS EN LOS ELEMENTOS ESTRUCTURALES, CONSULTAR LOS PLANOS CORRESPONDIENTES.
- LOS DETALLES QUE SE INDICAN ESTÁN FUERA DE ESCALA.
- ESPECIFICACIONES DE MATERIALES:
 - CONCRETO NORMAL DE P.V. = 2.2 ton./m³ Y T.M.A. = 1.9 cm. (" ").
 - F'C = 100 kg/cm² FIRME
F'C = 250 kg/cm² LOSAS TRABES Y CASTILLOS.
 - ACERO DE REFUERZO GRADO DURO RY = 4,200 kg/cm². EXEPTO EL DEL N°. 2 QUE SERA DE FY = 2,530 kg/cm².
- LA SEPARACION DE LOS ESTRIBOS VERTICALES SE EMPESARA A CONTAR A PARTIR DEL PAÑO O APOYO, COLOCANDOSE EL PRIMERO A LA MITAD DE LA SEPARACION INDICADA.
- TODOS LOS CASTILLOS DEBERAN CONTINUARSE EN LAS CADENAS INTERMEDIAS Y DEBERAN ANCLARSE EN LAS CADENAS DE REMATE.
- EL CURADO DEBE INICIAR INMEDIATAMENTE DEL FRAGUADO INICIAL.
- AL MOMENTO DE COLOCAR EL ACERO DE REFUERZO ESTE DEBERA DE ESTAR LIBRE DE IMPUREZAS ACEITE, OXIDO etc. QUE PUDIERA AFECTAR LA ADHERENCIA

NORTE

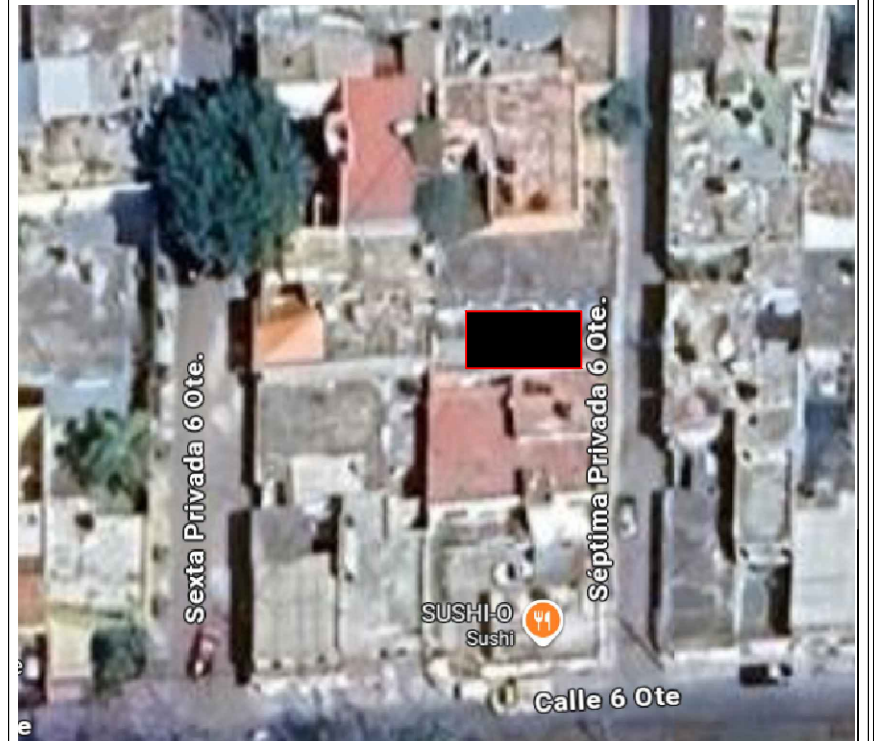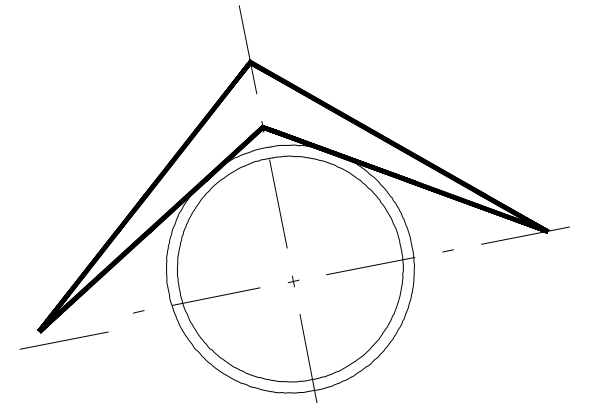

LOCALIZACION

SIMBOLOGIA:	
	ABERTURA PUERTA
	ABERTURA VENTANA
	PROYECCIONES
	SENTIDO DE ABERTURA
	CAMBIO DE NIVEL
	PROYECCIÓN DE VACIO
	LINEA DE CORTE

CUADRO DE CONSTRUCCIÓN POR NIVEL

CONSTRUCCIÓN PLANTA BAJA	71.85 M2
CONSTRUCCIÓN PLANTA ALTA	71.85 M2
CONSTRUCCIÓN PLANTA DE AZOTEA	35.42 M2
TOTAL DE CONTRUCCION	179.12 M2
AREA DEL TERRENO	90.00 M2

PROPIETARIO:	ALEJANDRO CUEVAS VILLAGOMEZ	
UBICACION:	SEPTIMA PRIVADA DE LA 16 ORIENTE, NUMERO 605, LETRA A, COLONIA QUINTA GUADALUPE, TEHUACAN PUEBLA.	
PROYECTO:	HABITACIONAL	ESCALA: INDICADA
		COTAS: METROS
PLANO:	ESTRUCTURAL	
FIRMA DEL D.R.O.:	FIRMA DEL PROPIETARIO:	
FECHA: JUNIO 2026		