




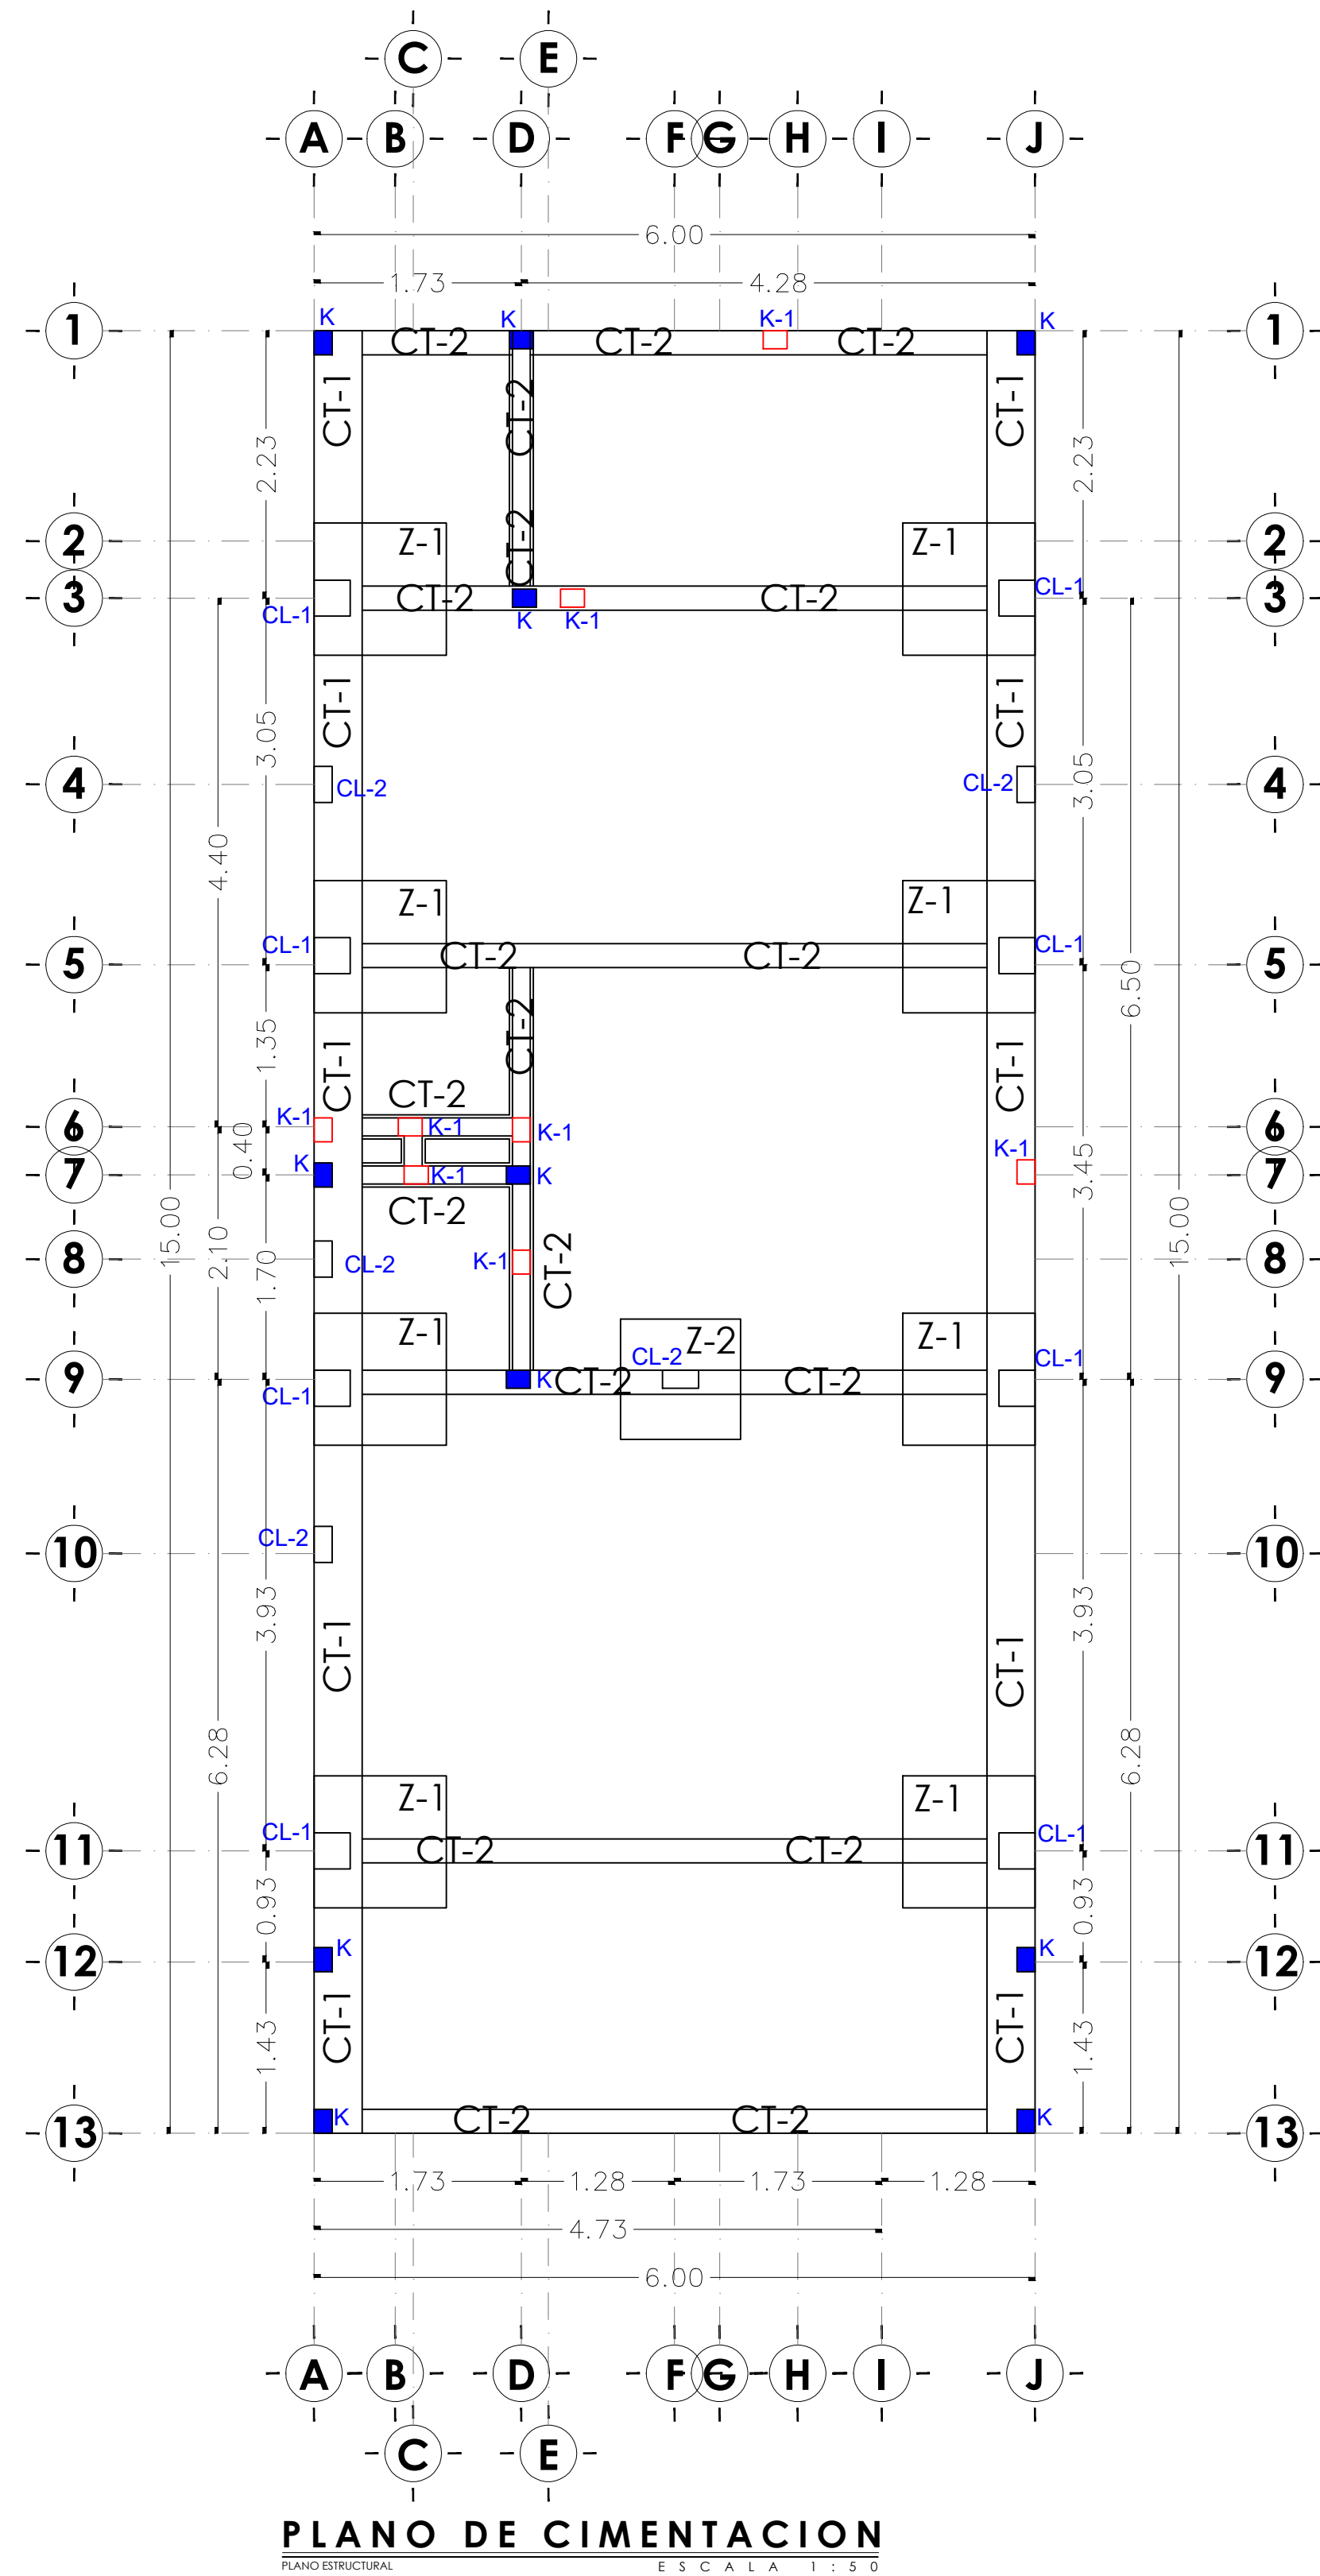

PLANO DE CIMENTACION
Escala 1:50

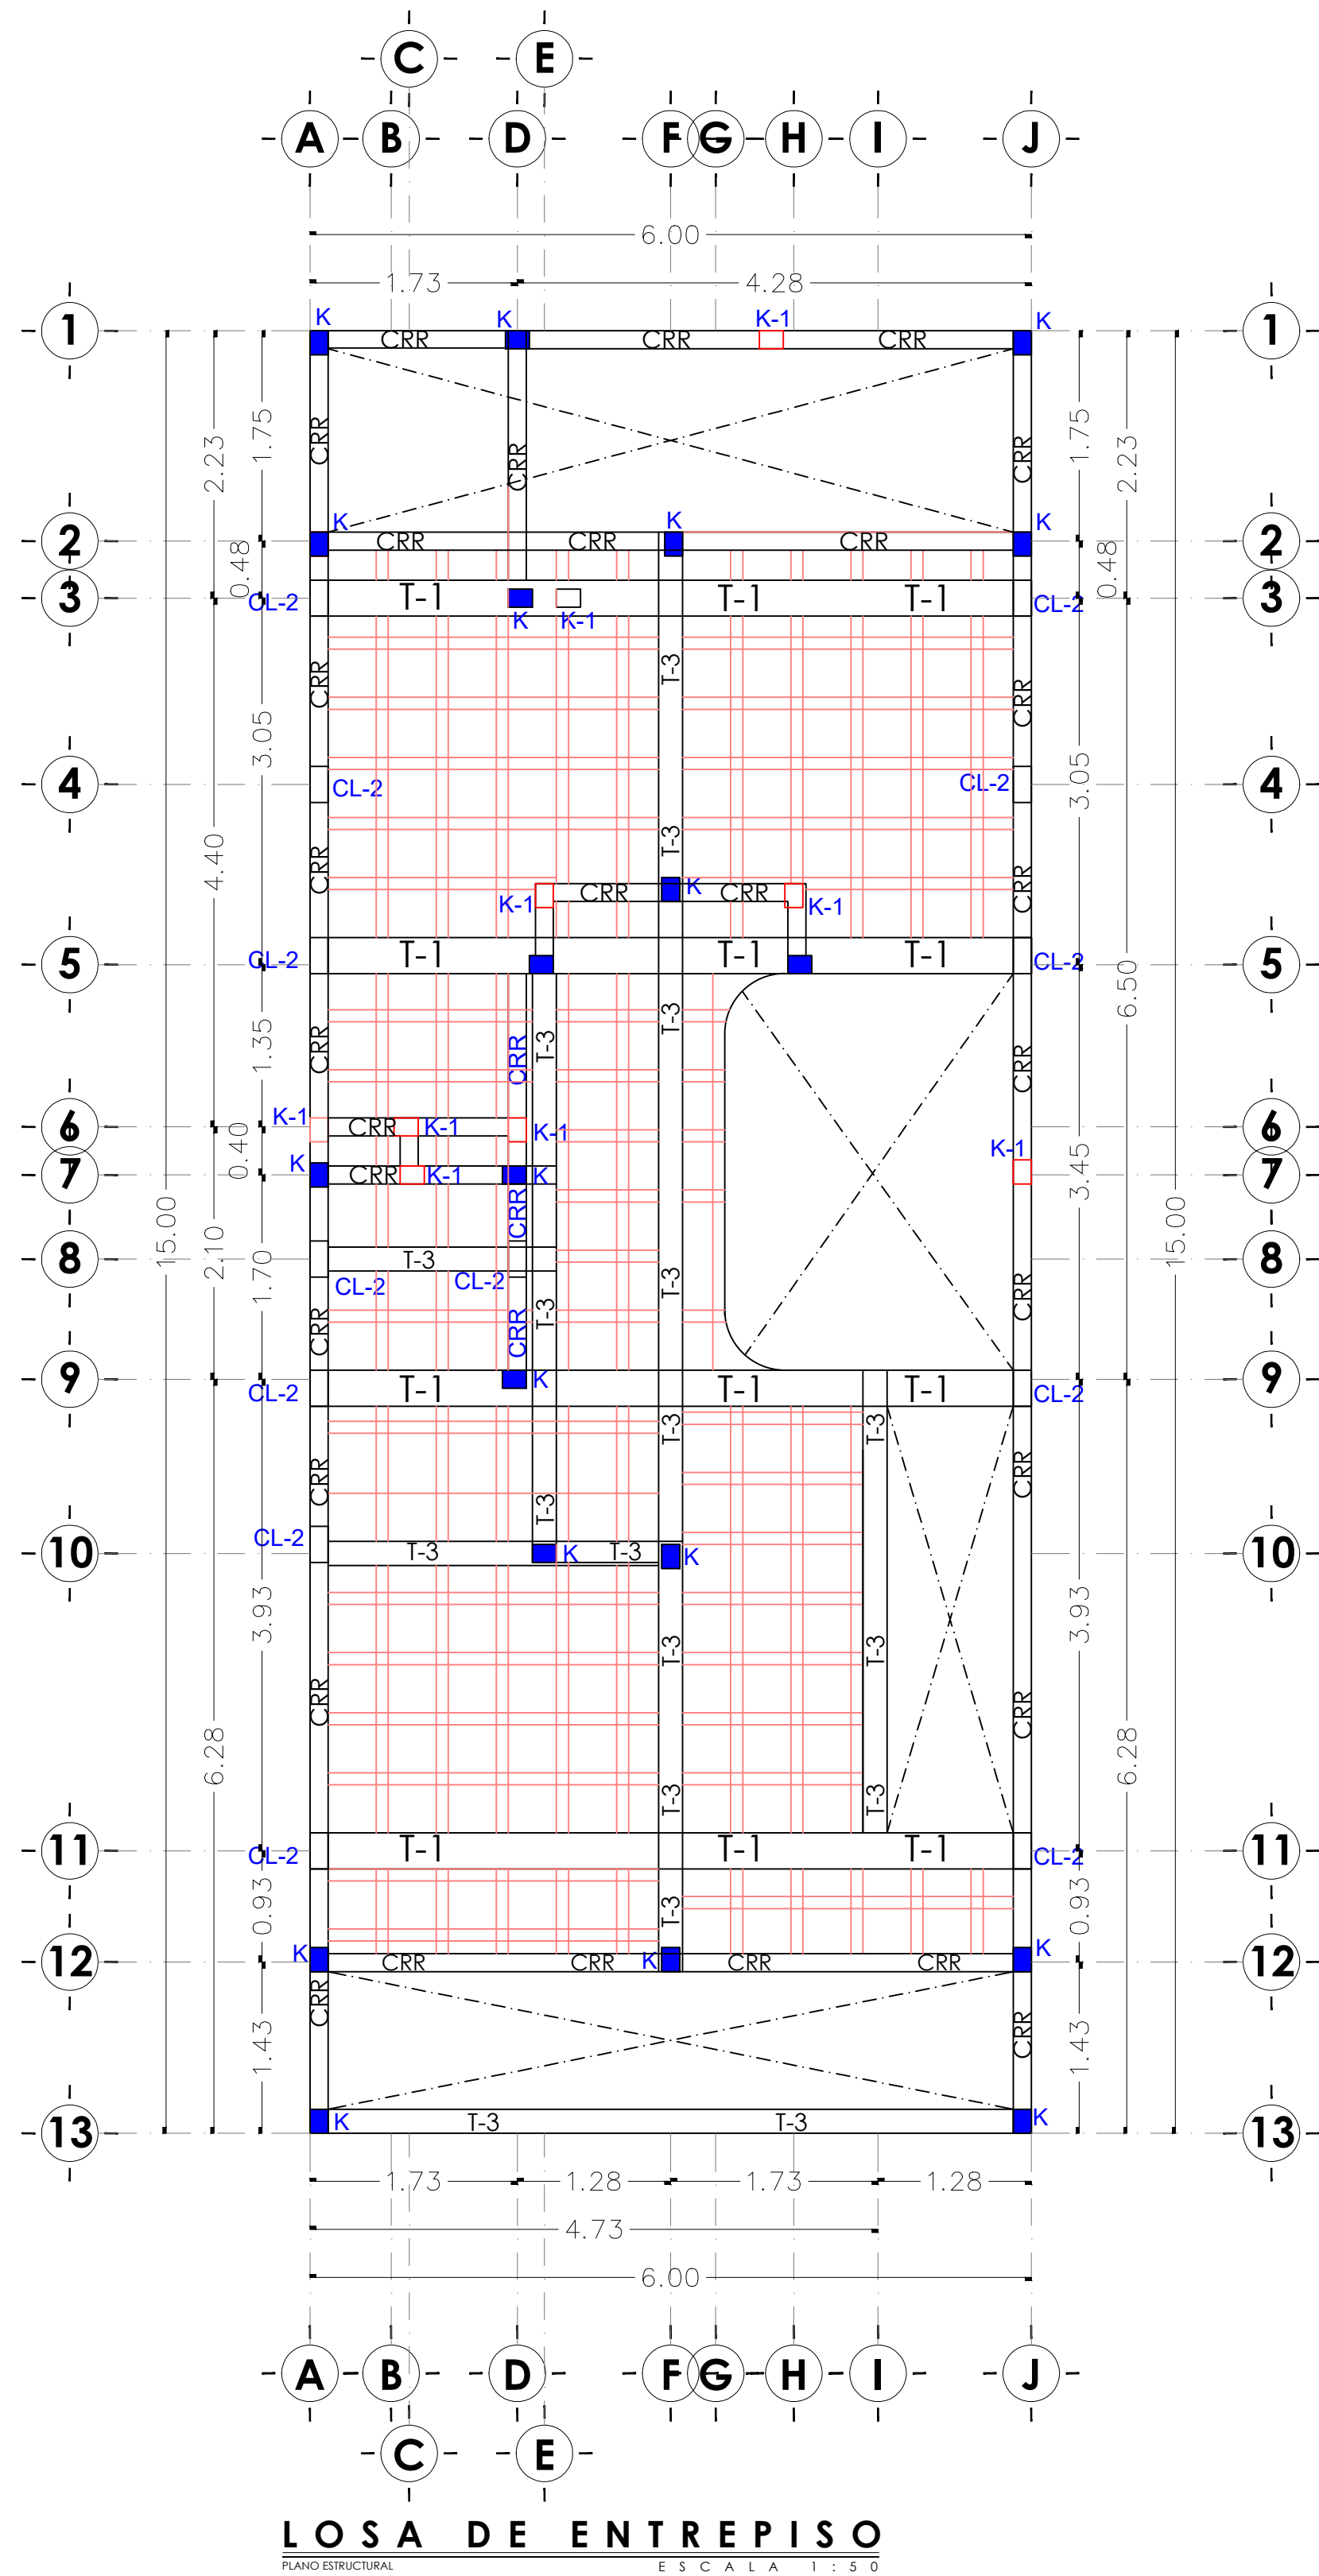

LOSA DE ENTREPISO
Escala 1:50

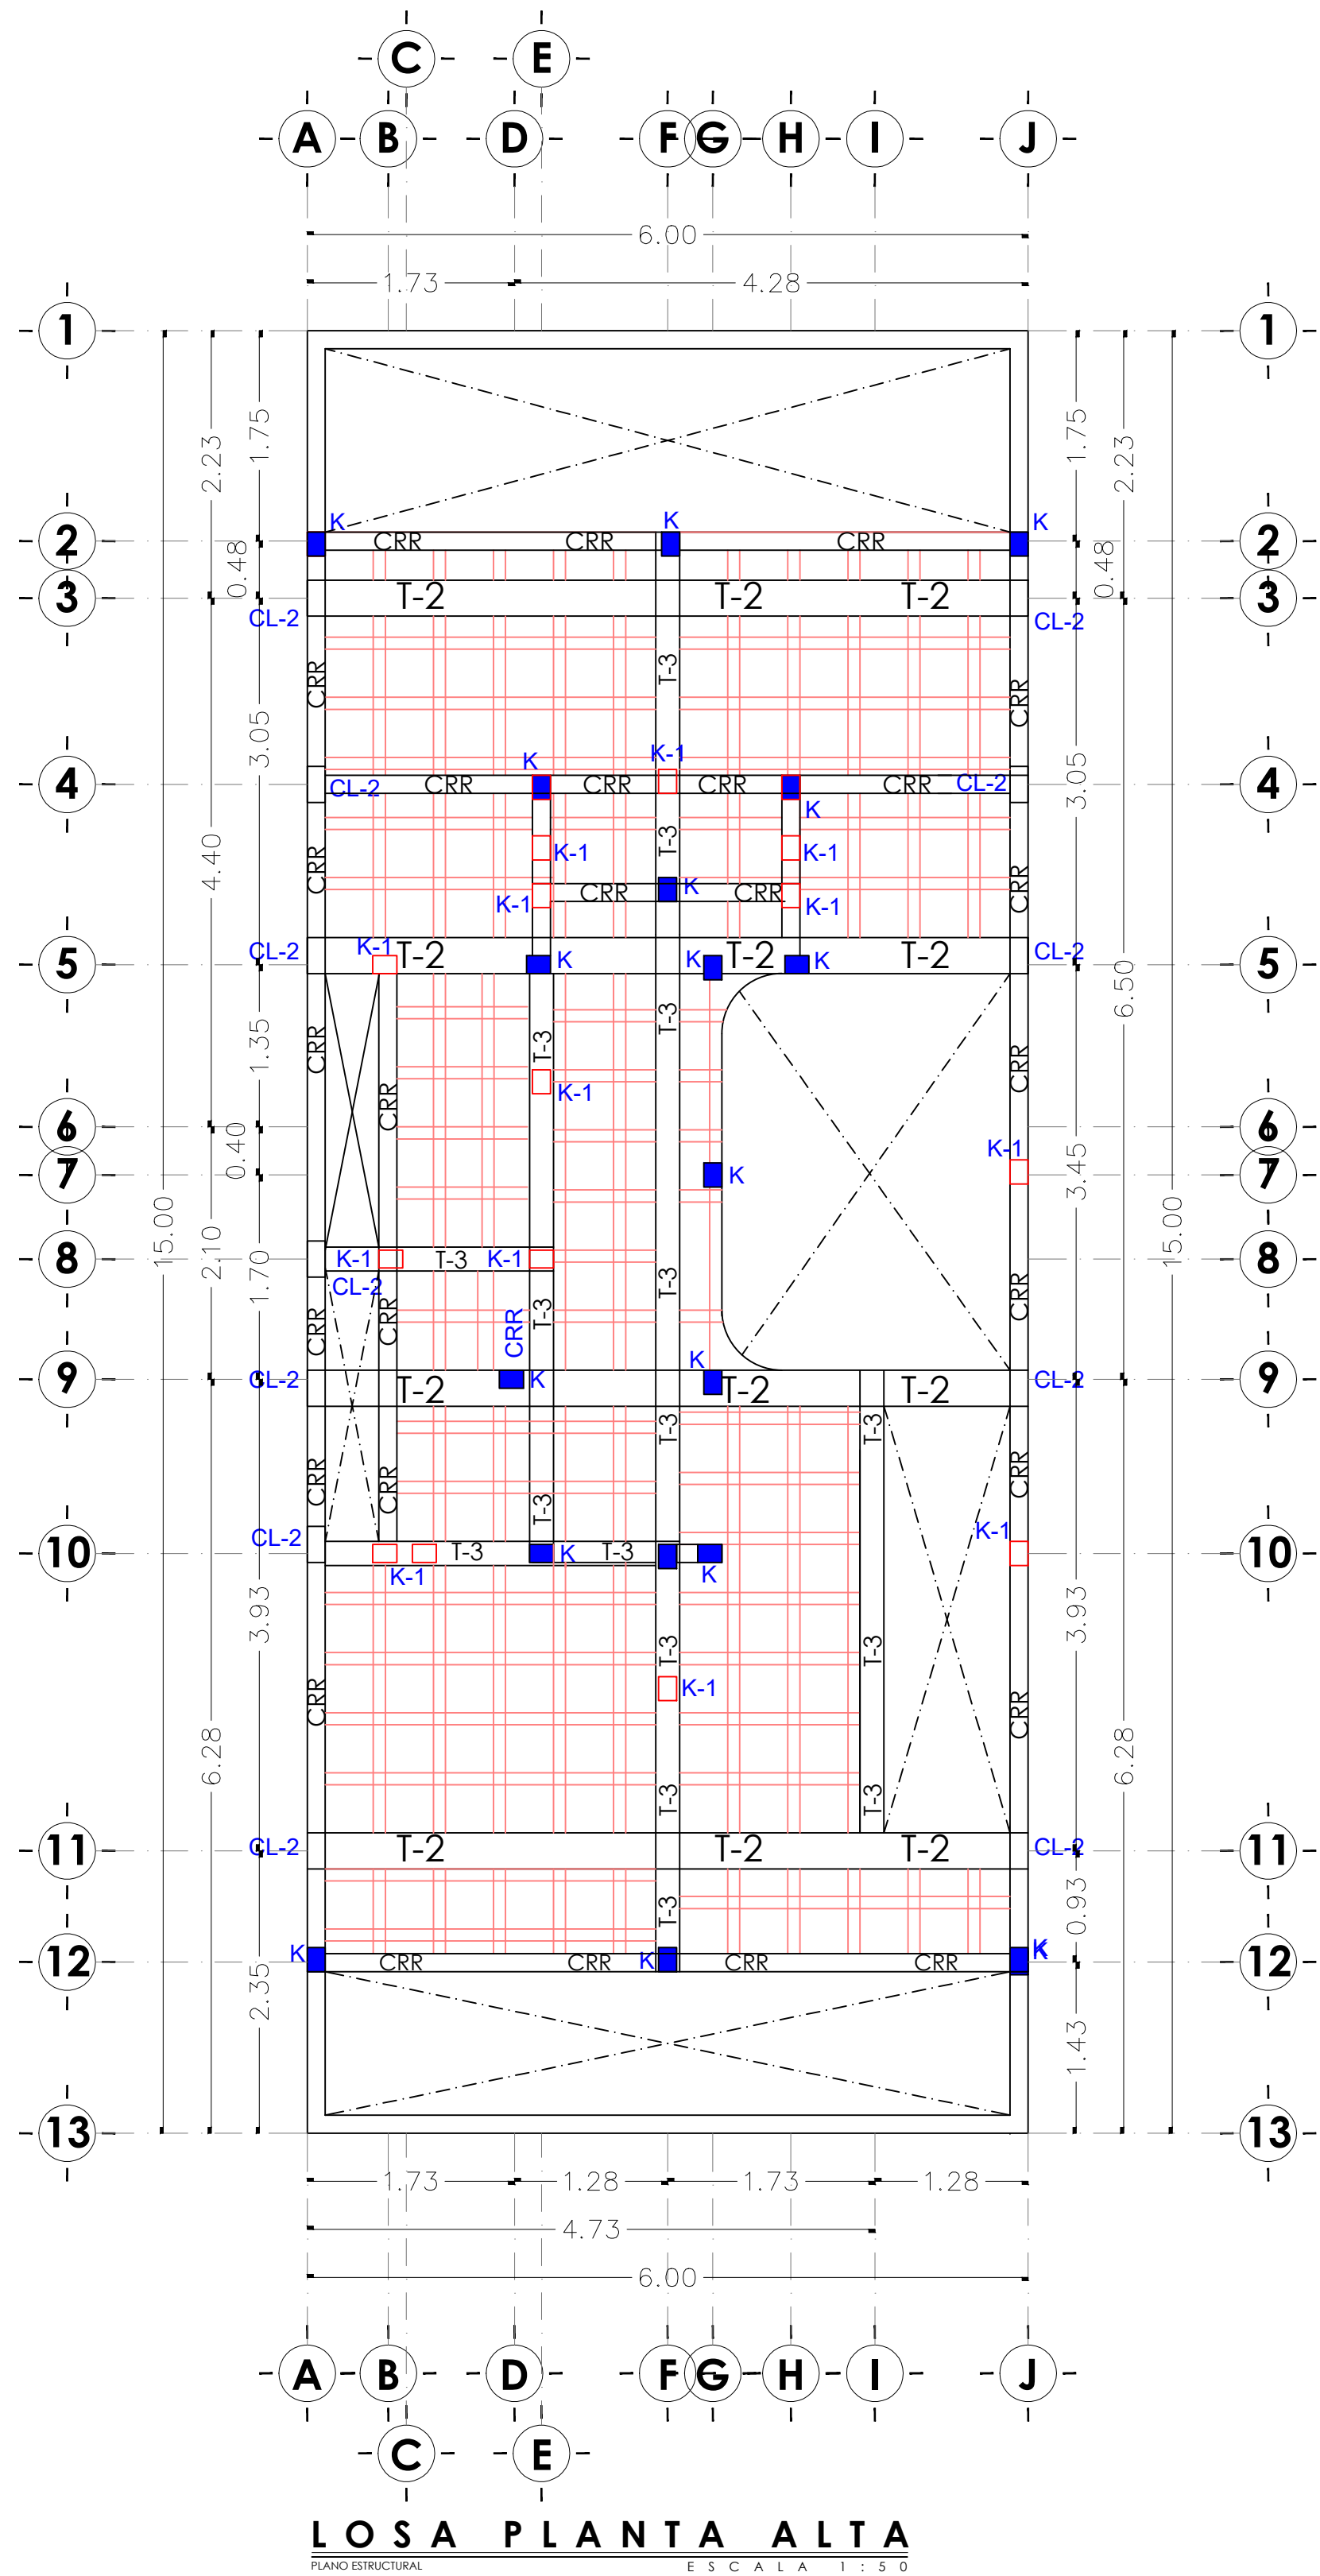

LOSA PLANTA ALTA
Escala 1:50

NORTE

LOCALIZACION

SIMBOLOGIA:

- ABERTURA PUERTA
- ABERTURA VENTANA
- PROYECCIONES
- SENTIDO DE ABERTURA
- CAMBIO DE NIVEL
- PROYECCIÓN DE VACIO
- LINEA DE CORTE

CUADRO DE CONSTRUCCIÓN POR NIVEL

CONSTRUCCIÓN	AREA (M2)
CONSTRUCCIÓN PLANTA BAJA	71.85 M2
CONSTRUCCIÓN PLANTA ALTA	71.85 M2
CONSTRUCCIÓN PLANTA DE AZOTEA	35.42 M2
TOTAL DE CONSTRUCCION	179.12 M2
AREA DEL TERRENO	90.00 M2

PROPIETARIO: ALEJANDRO CUEVAS VILLAGOMEZ

UBICACION: SEPTIMA PRIVADA DE LA 16 ORIENTE, NUMERO 605, LETRA A, COLONIA QUINTA GUADALUPE, TEHUACAN PUEBLA.

PROYECTO: HABITACIONAL

ESCALA: INDICADA

COTAS: METROS

PLANO: ESTRUCTURAL

FIRMA DEL D.R.O.: FIRMA DEL PROPIETARIO:

FECHA: JUNIO 2026