

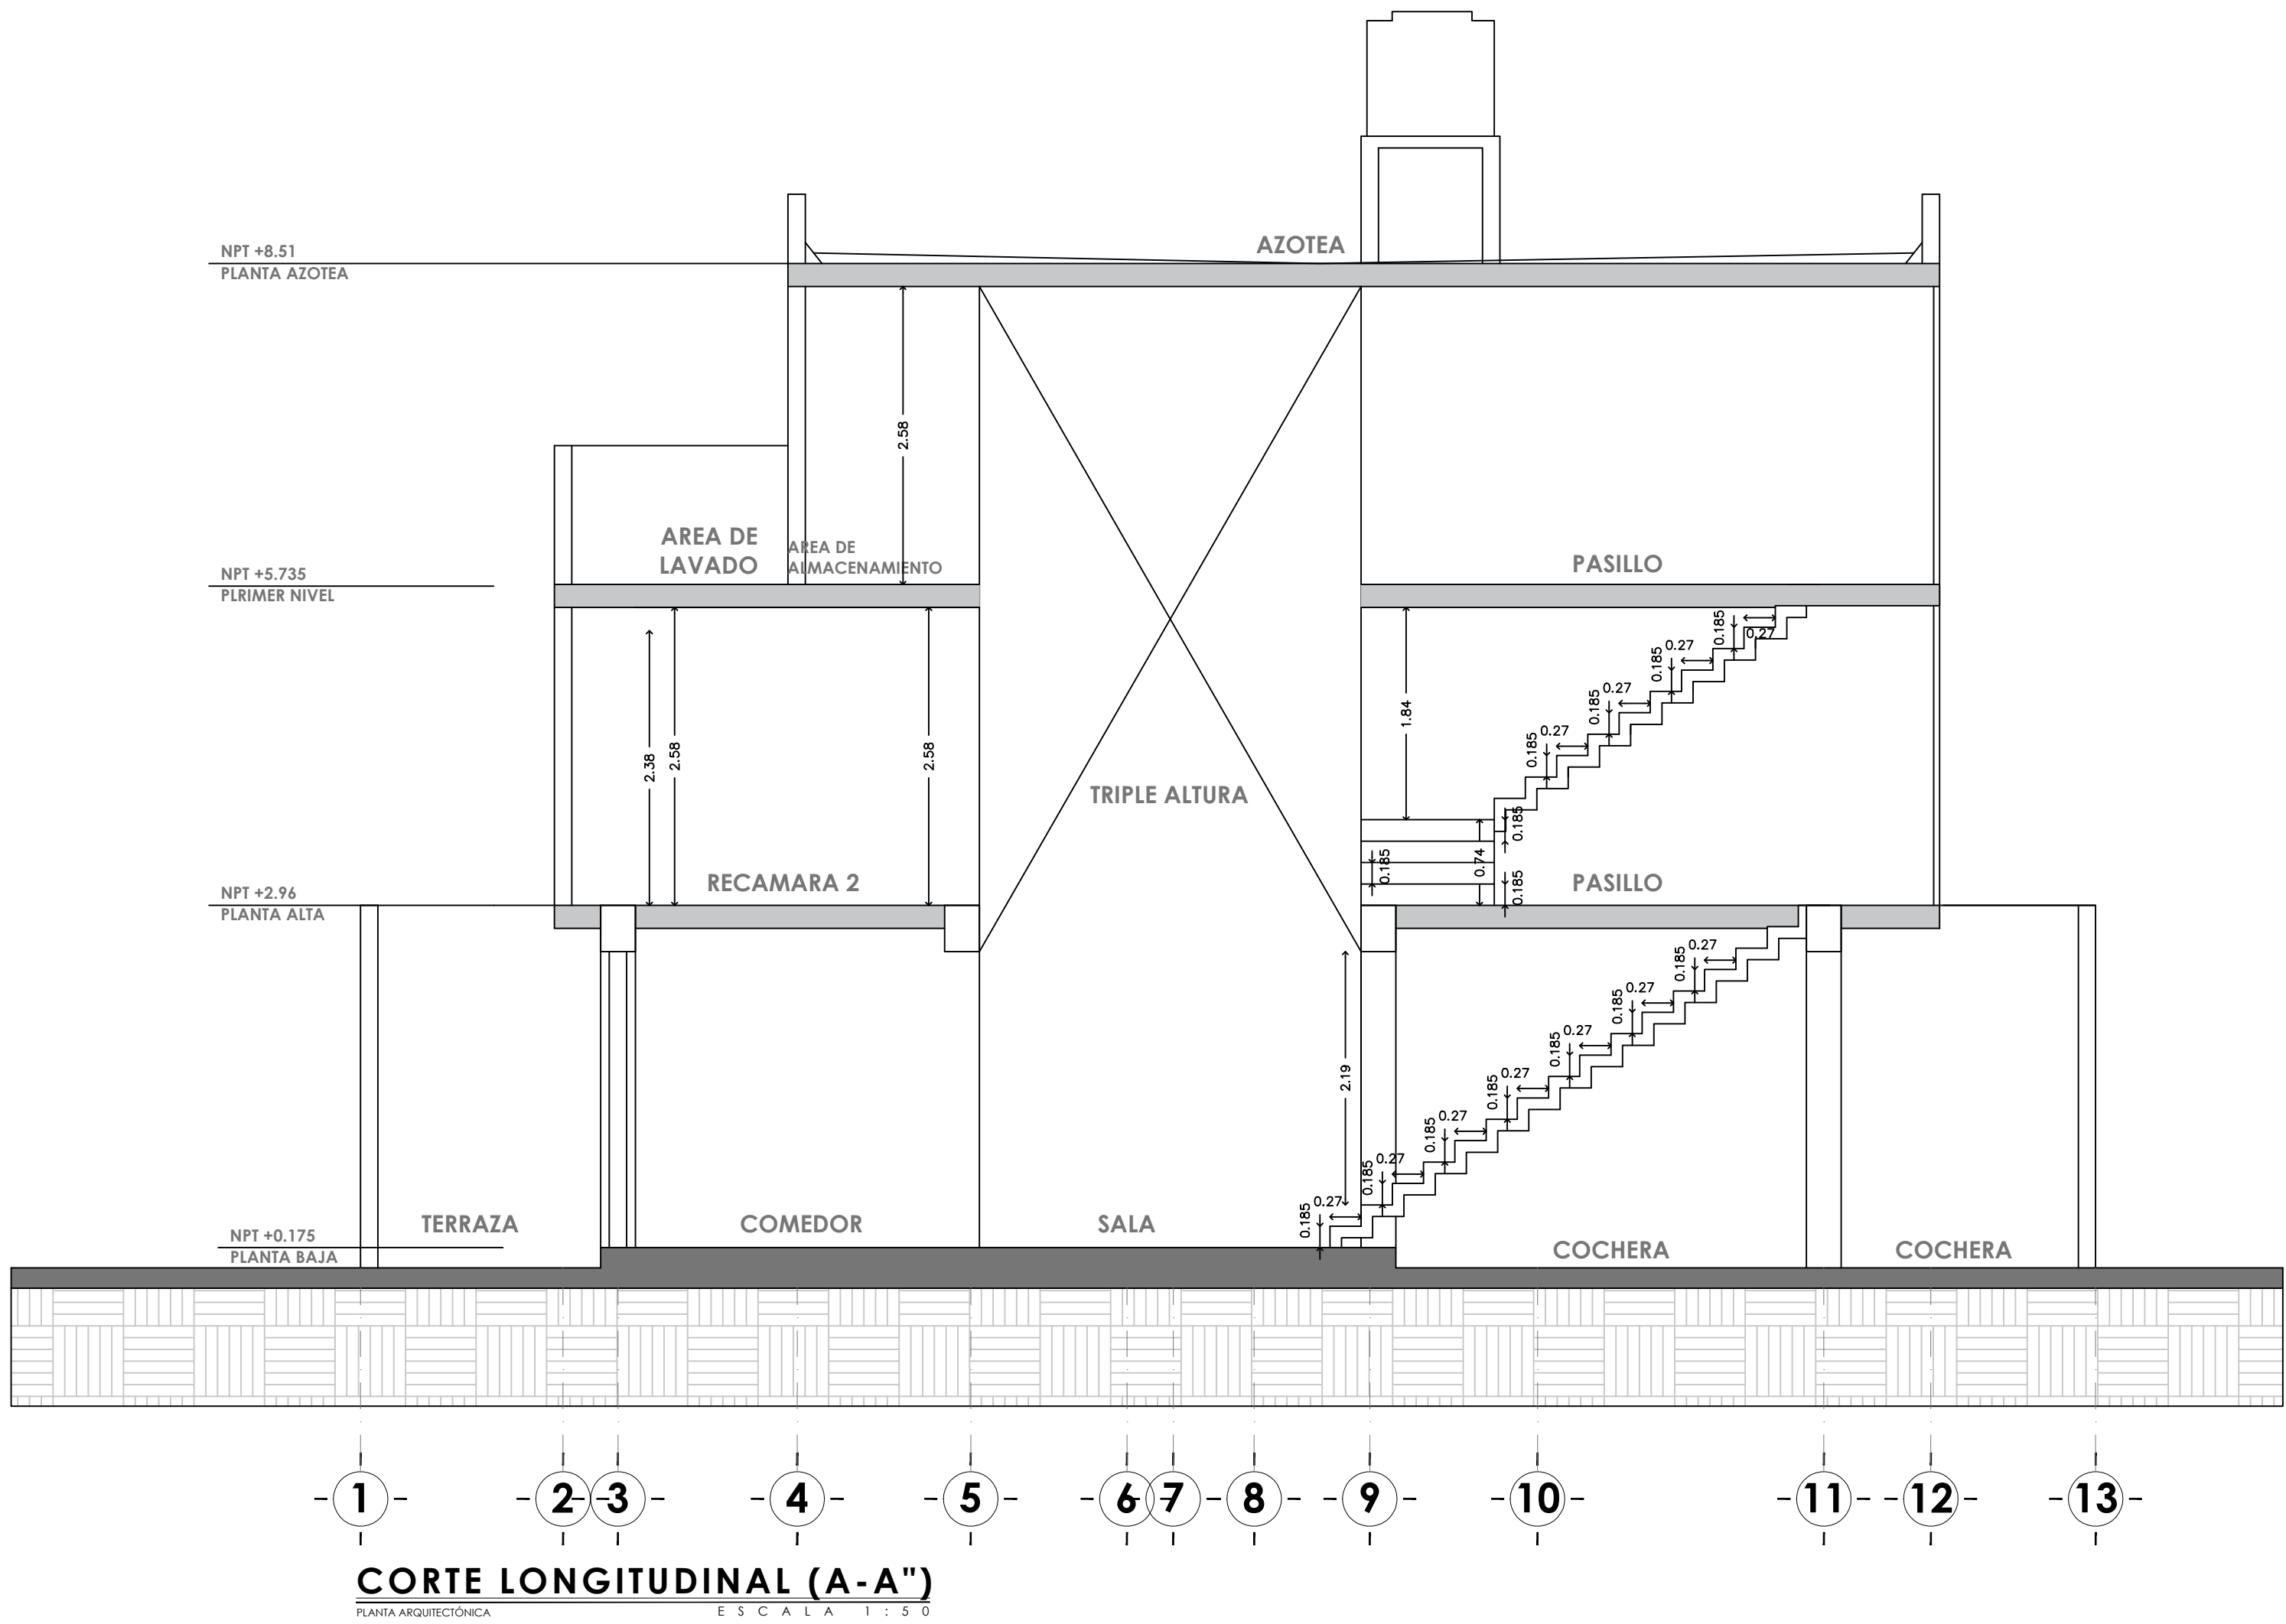
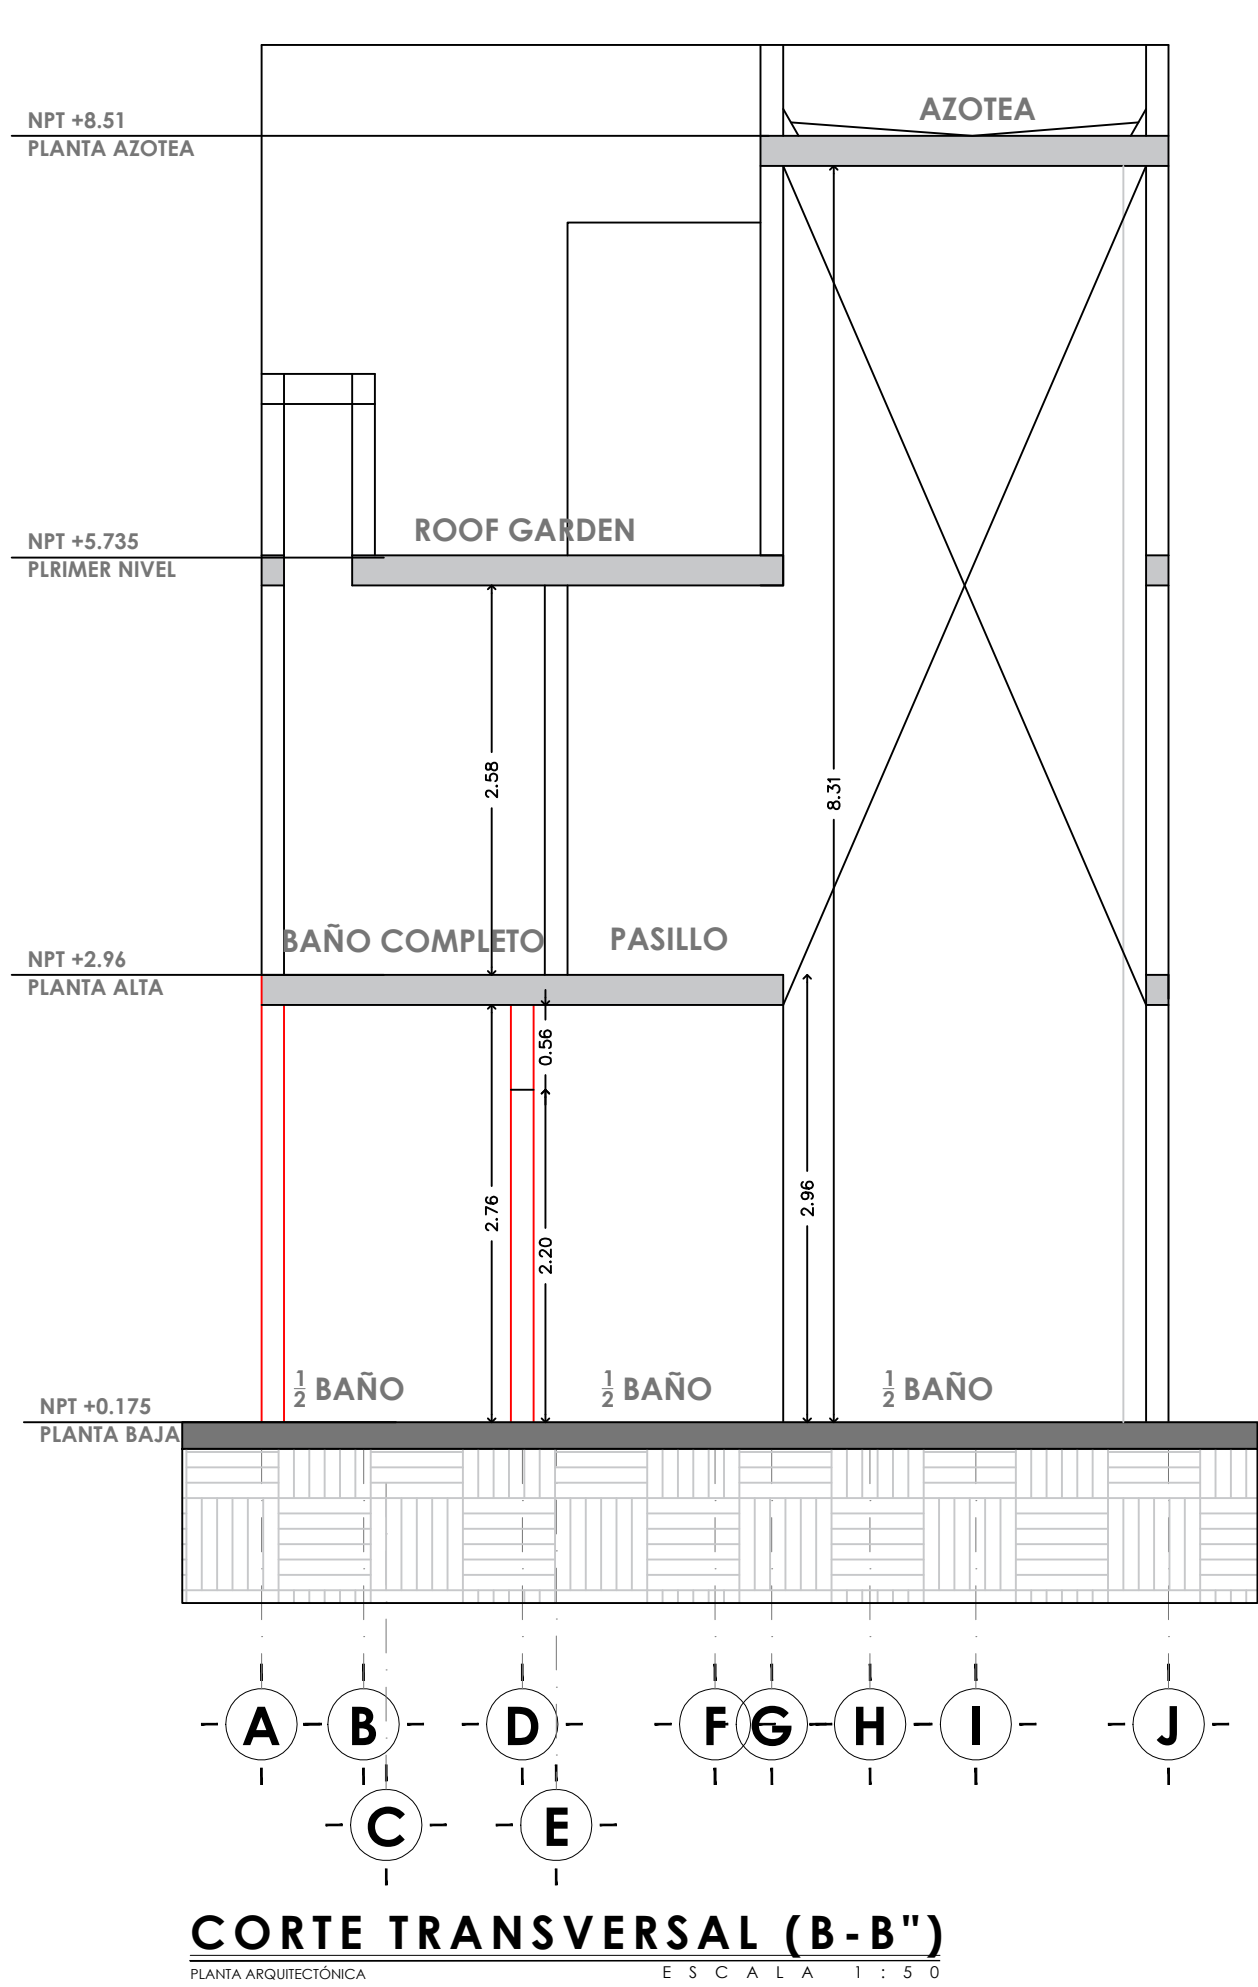
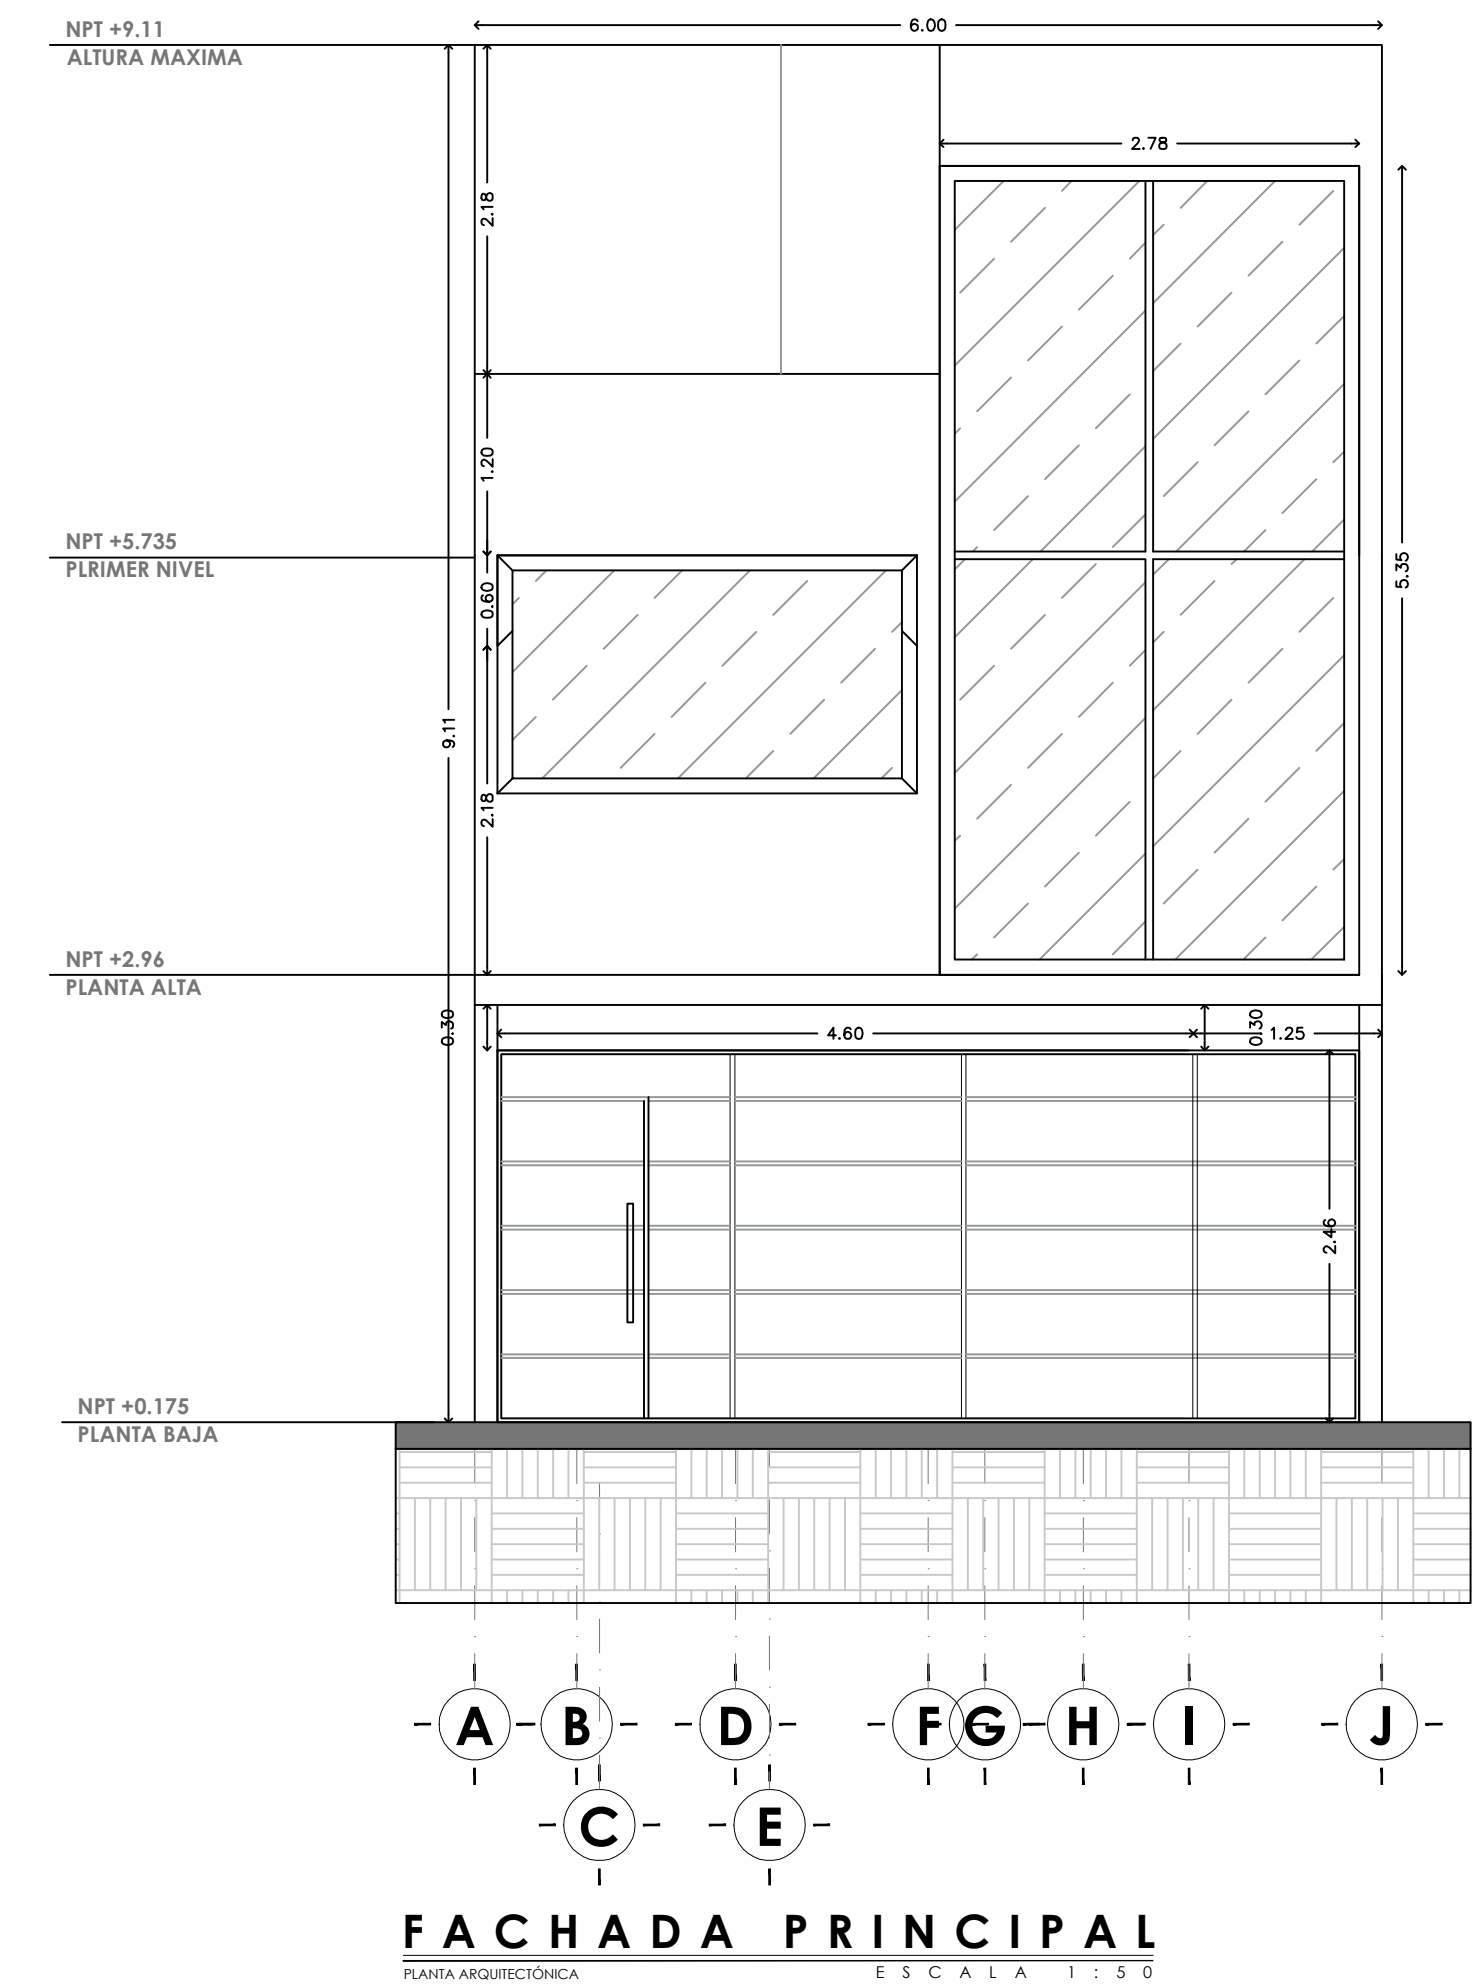


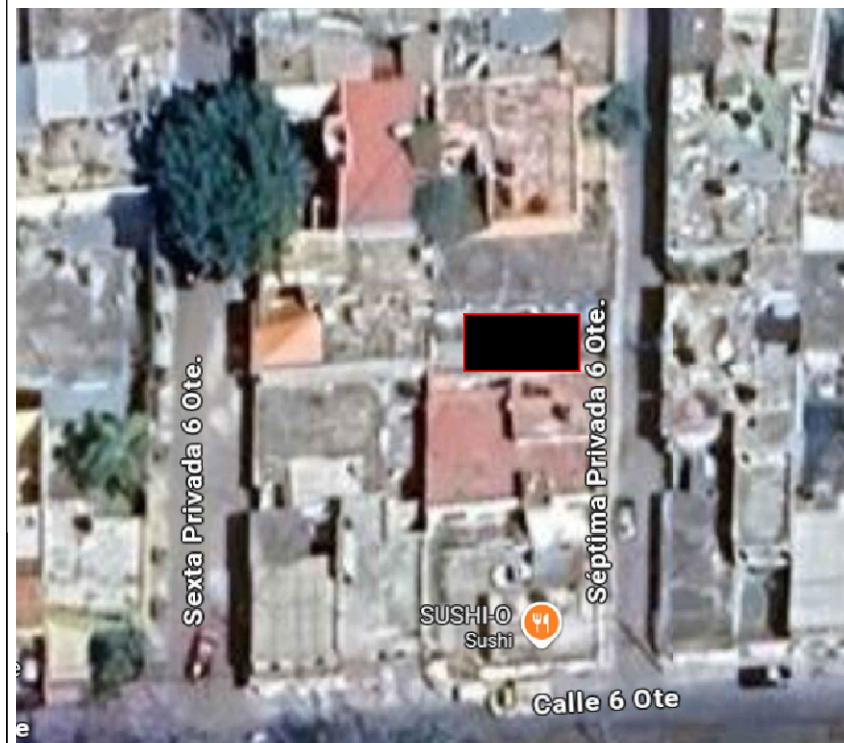

NORTE

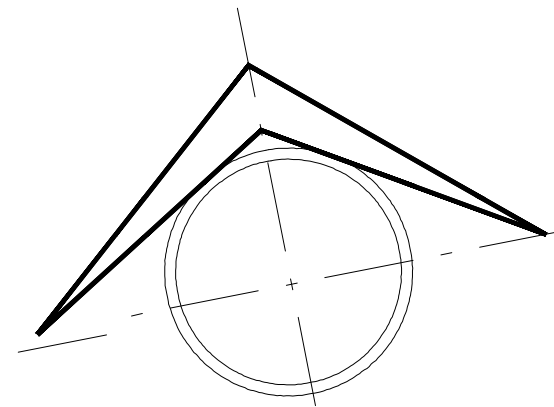

LOCALIZACION

SIMBOLOGIA:

	ABERTURA PUERTA		CAMBIO DE NIVEL
	ABERTURA VENTANA		PROYECCIÓN DE VACÍO
	PROYECCIONES		LÍNEA DE CORTE
	SENTIDO DE ABERTURA		

CUADRO DE CONSTRUCCIÓN POR NIVEL	
CONSTRUCCIÓN PLANTA BAJA	71.85 M2
CONSTRUCCIÓN PLANTA ALTA	71.85 M2
CONSTRUCCIÓN PLANTA DE AZOTEA	35.42 M2
TOTAL DE CONTRUCCION	179.12 M2
AREA DEL TERRENO	90.00 M2

PROPIETARIO:	ALEJANDRO CUEVAS VILLAGOMEZ		
UBICACION:	SEPTIMA PRIVADA DE LA 16 ORIENTE, NUMERO 605, LETRA A, COLONIA QUINTA GUADALUPE, TEHUACAN PUEBLA.		
PROYECTO	HABITACIONAL	ESCALA	INDICADA
		COTAS	METROS
PLANO:	ARQUITECTONICO		
FACHADAS Y CORTES			
FIRMA DEL D.R.O.:	FIRMA DEL PROPIETARIO:		
	FECHA: JUNIO 2026		