
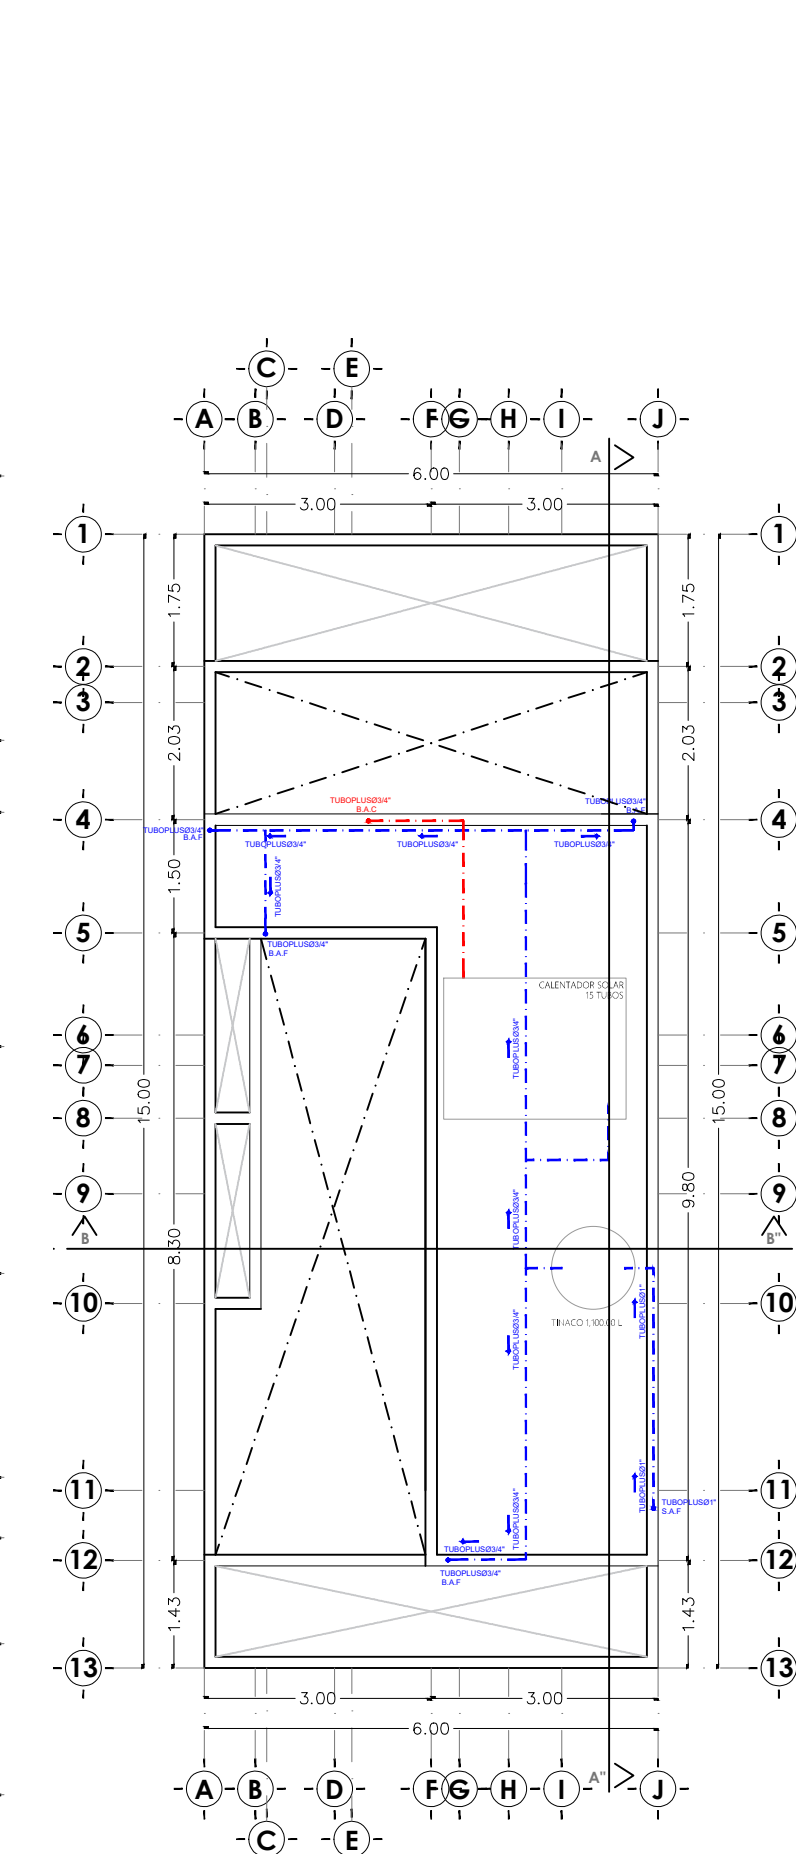


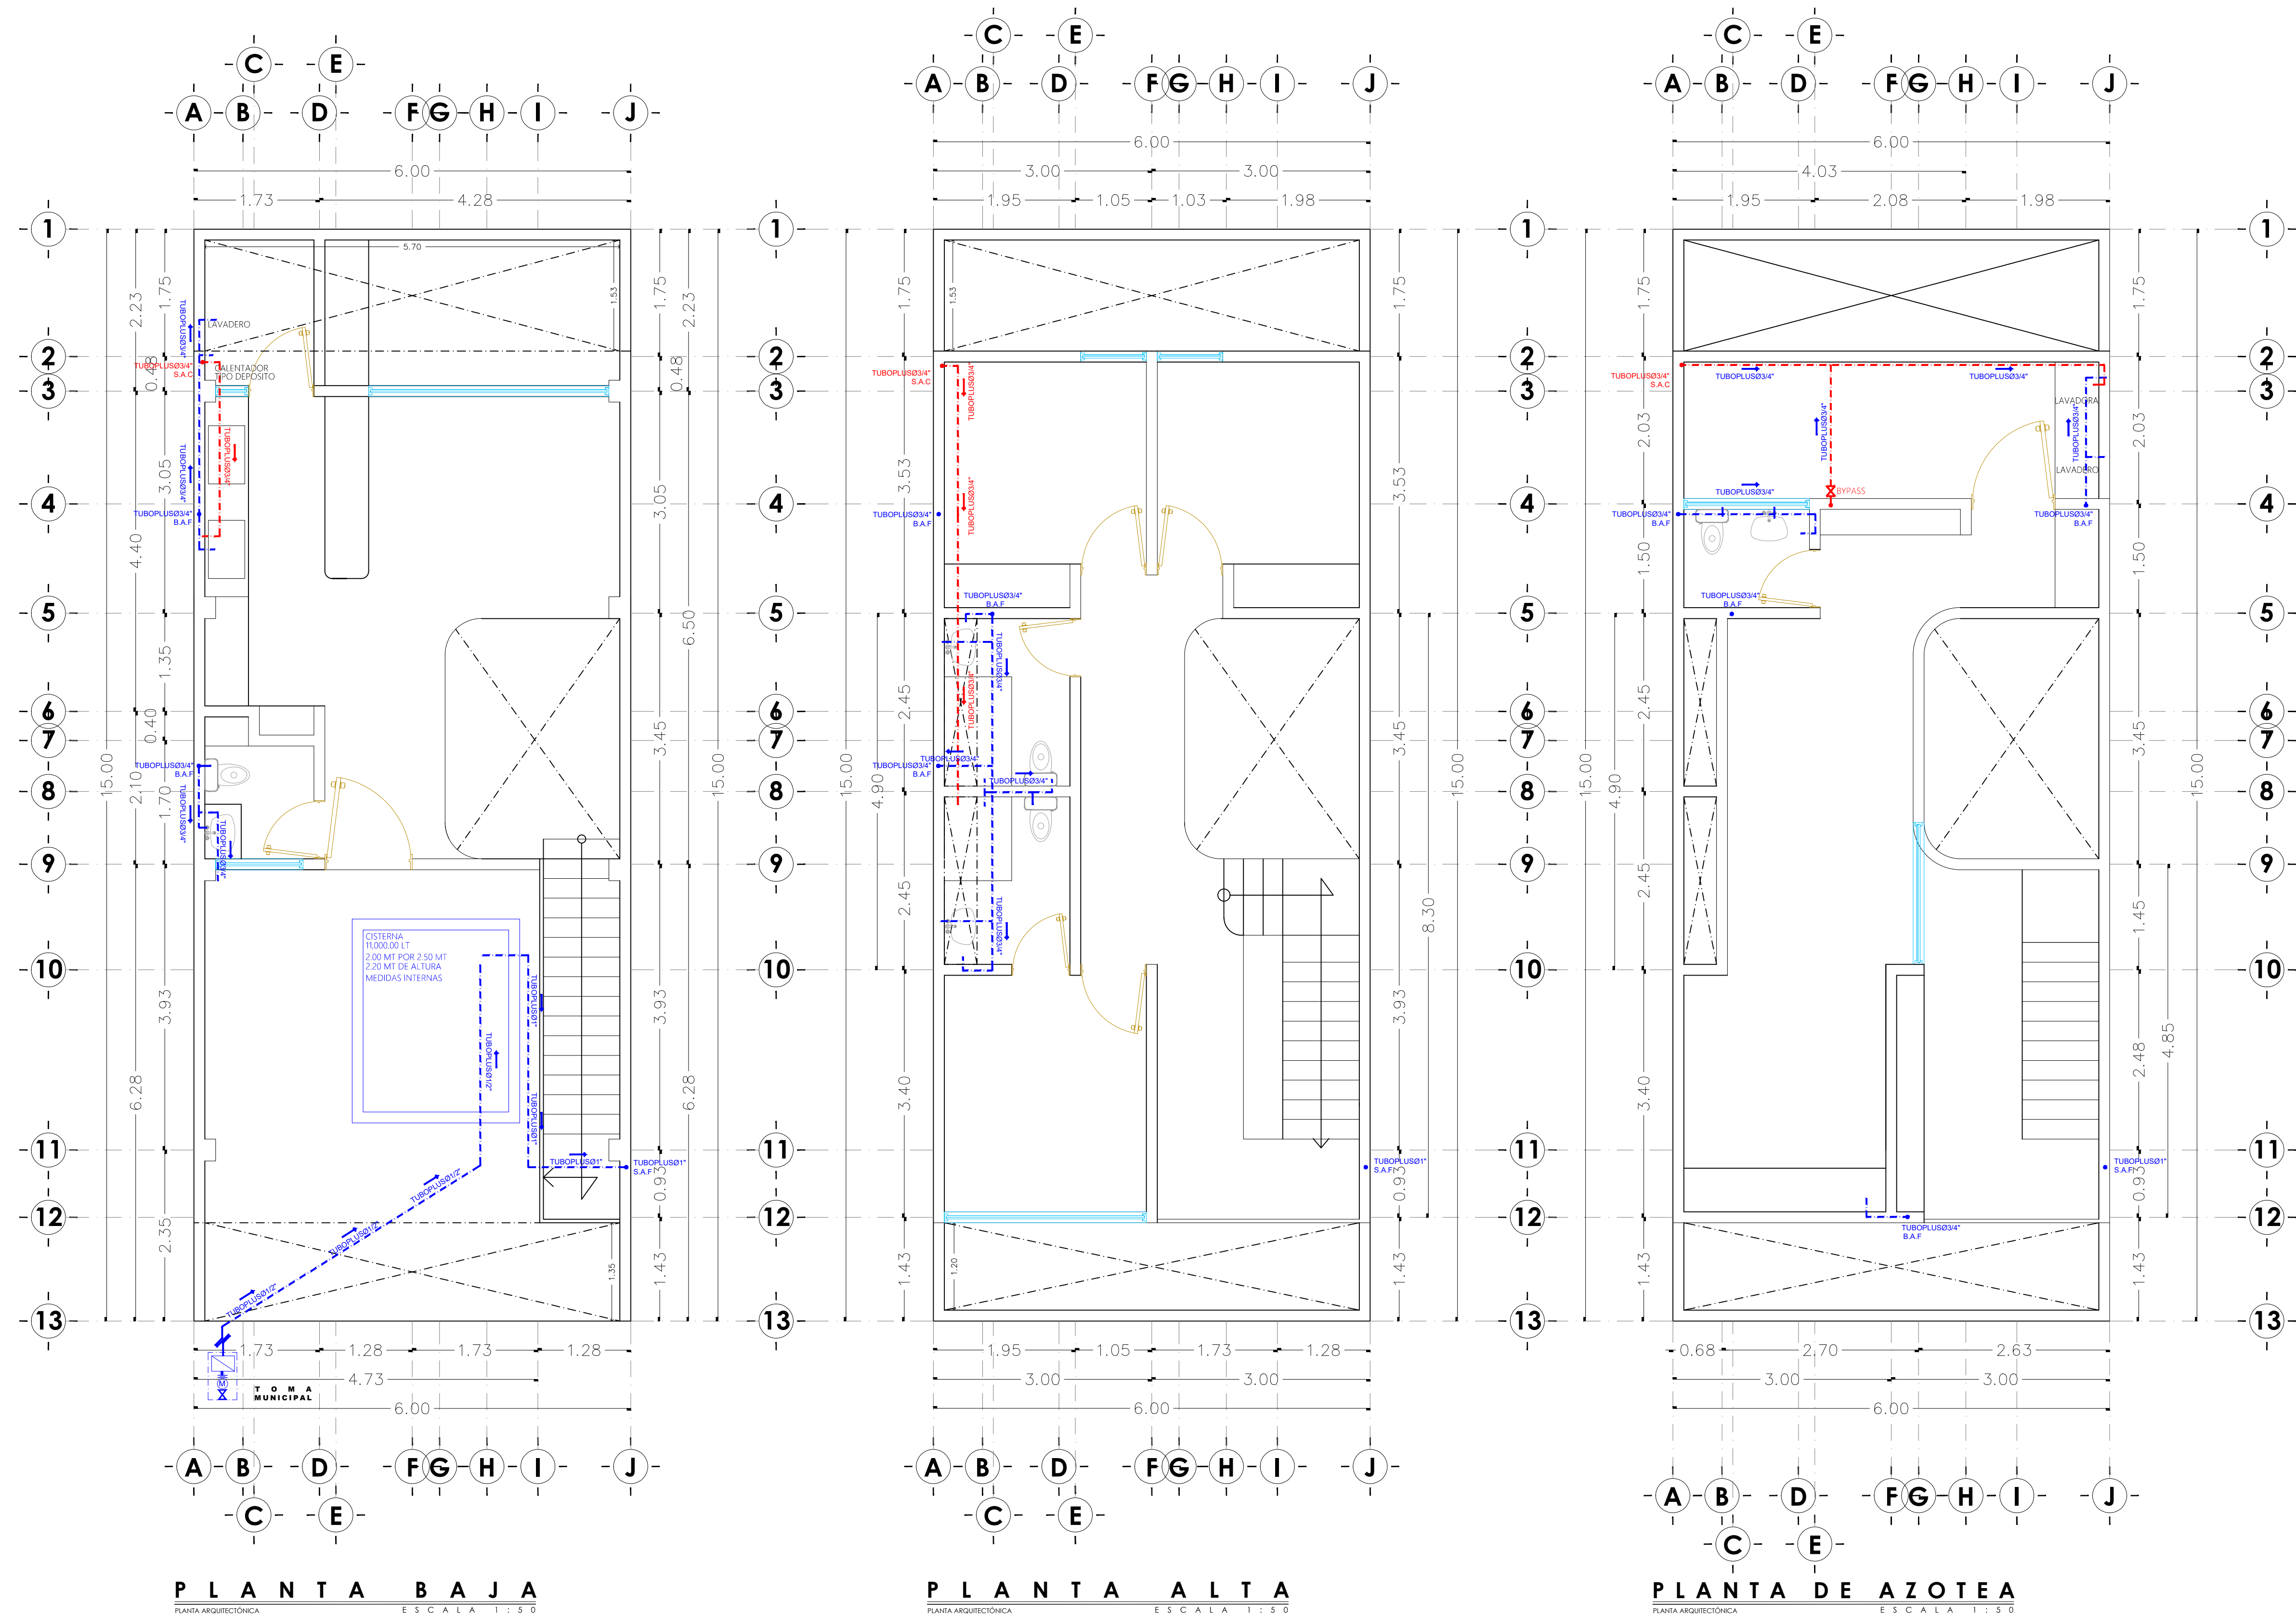


SIMBOLOGIA HIDRAULICA	
	MEDIDOR
	TUBERIA DE AGUA CALIENTE
	TUBERIA DE AGUA FRIA
	S.A.F. SUBE AGUA FRIA, CALIENTE
	B.A.F. BAJA AGUA FRIA, CALIENTE
	CISTERNA 10,800 LTS.
	TINACO 1100 LTS.
	TUBERIA DE GAS.

DATOS HIDRAULICOS	
NUMERO DE PERSONAS.	6
CONSUMO POR PERSONA.	150 LT/HAB.
TOTAL DE AGUA NECESARIA/DIA.	900 LTS.
TOTAL DE AGUA ALMACENADA.	12,100. LTS.
DIAMETRO DE LA TOMA.	12.70 MM.
CAPACIDAD DEL TINACO.	1100 LTS.
MONTANTES.	19.050 MM.
BAJANTES.	19.050 MM.

ESPECIFICACIONES DE INSTALACIÓN HIDRAULICA

- LA TUBERIA ANTES DE SER COBERTA, TENDRA QUE SER PROBADA A UNA PRESION DE 5 KG/CM2 DURANTE UN MINIMO DE 4 HORAS.
- LA TUBERIA NO SERA COBERTA HASTA LA OBTENCION DEL V.O.B. DE LA RESIDENCIA DE OBRA.
- DEBERA EVITARSE QUE EL PESO DE LA TUBERIA ACTUE DIRECTAMENTE EN CONEXIONES O MUJERES.
- EL W.C. TENDRA UNA DESCARGA MAXIMA DE 6 LITROS EN CADA SERVICIO.
- EL DIAMETRO DE LAS TUBERIAS ESTA DADO EN PULGADAS
- LAS CONEXIONES O TRAMOS DE TUBERIAS QUE PRESENTEN FISURAS DURANTE LA PRUEBA DE CARGA HIDROSTATICA SERAN REMEDIADAS POR PIEZAS NUEVAS Y EN BUEN ESTADO, UNA VEZ ACEPTADA LA TUBERIA DEBERA PROTEGERSE CONTRA ATAQUES FISICOS, QUE PUEDAN AFECTAR EL FUNCIONAMIENTO.
- EL TENDIDO DE LA TUBERIA SERA EXCLUSIVAMENTE A TRAVEZ DE TRAMOS RECTOS, SIN DOBLECES PARA CUALQUIER CAMBIO DE DIRECCION SE UTILIZA LA CONEXION ADICIONA.
- ANTES DE RECIBIR CON MEZCLA LA TUBERIA SE DEBERA DE DEJAR LIBRE DE CONTACTO DIRECTO CON ALAMBRES O CLAVOS AHORADOS EN EL MORTERO.
- LAS SALIDAS DE W.C. Y LAVABO DEBERAN TENER AJUSTOS ECONOMIZADORES (MAX 10 LTS / MIN.

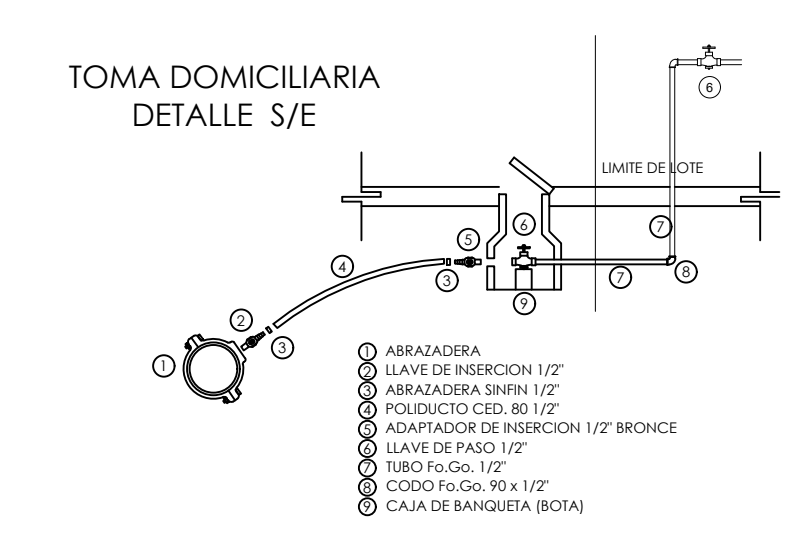

NORTE

LOCALIZACION

SIMBOLOGIA:

- ABERTURA PUERTA
- ABERTURA VENTANA
- PROYECCIONES
- SENTIDO DE ABERTURA
- CAMBIO DE NIVEL
- PROYECCIÓN DE VACIO
- LINEA DE CORTE

CUADRO DE CONSTRUCCIÓN POR NIVEL

CONSTRUCCIÓN PLANTA BAJA	71.85 M2
CONSTRUCCIÓN PLANTA ALTA	71.85 M2
CONSTRUCCIÓN PLANTA DE AZOTEA	35.42 M2
TOTAL DE CONSTRUCCION	179.12 M2
AREA DEL TERRENO	90.00 M2

PROPIETARIO: ALEJANDRO CUEVAS VILLAGOMEZ

UBICACION: SEPTIMA PRIVADA DE LA 16 ORIENTE, NUMERO 605, LETRA A, COLONIA QUINTA GUADALUPE, TEHUACAN PUEBLA.

PROYECTO: HABITACIONAL

ESCALA: INDICADA

COTAS: METROS

PLANO: HIDRAULICO

FIRMA DEL D.R.O.: FIRMA DEL PROPIETARIO:

FECHA: JUNIO 2026