
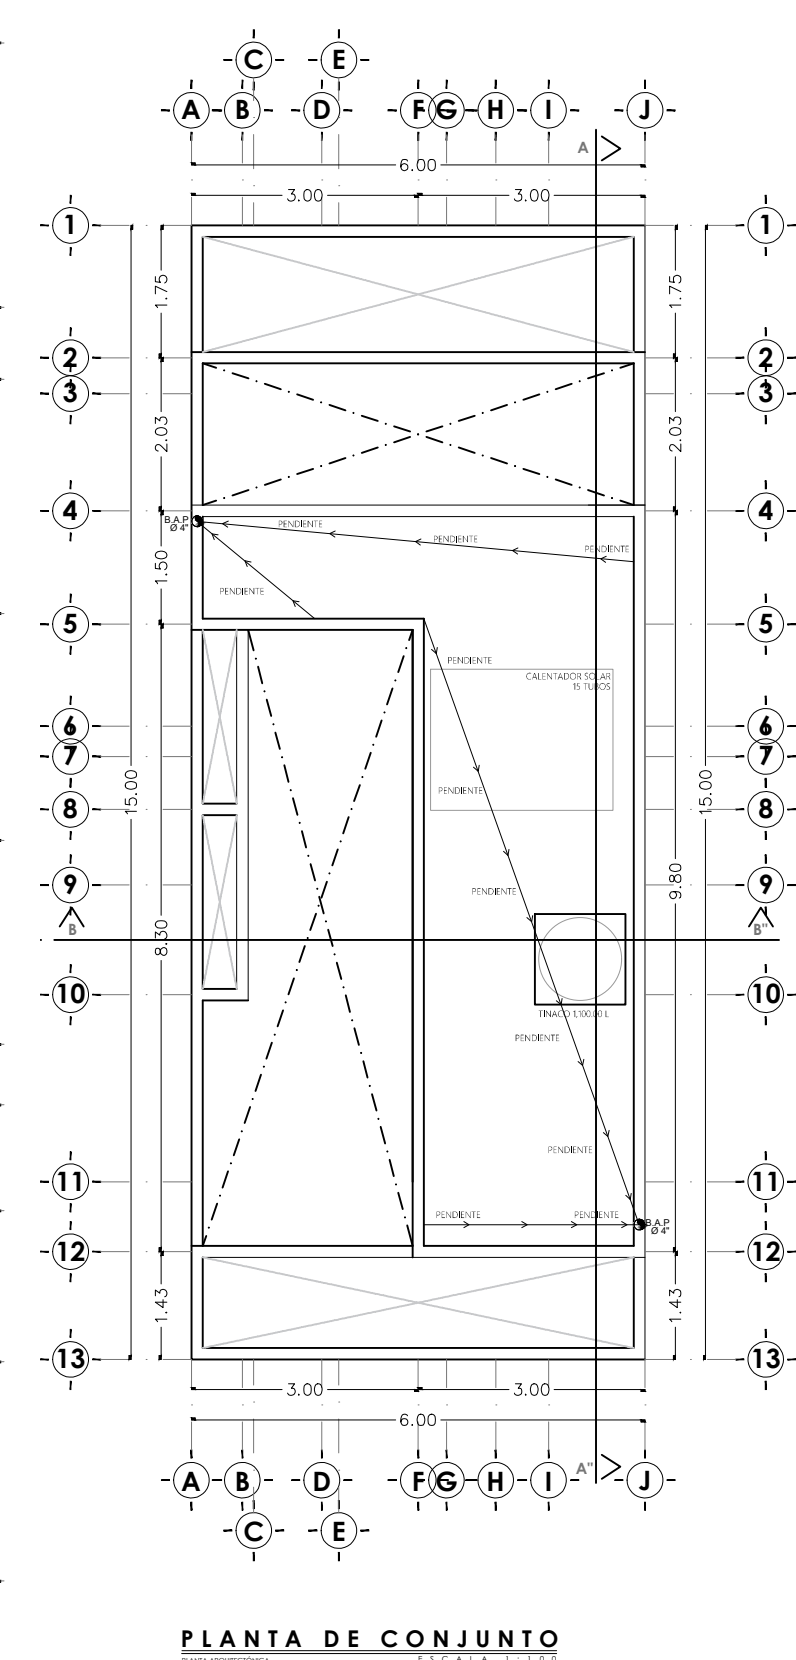
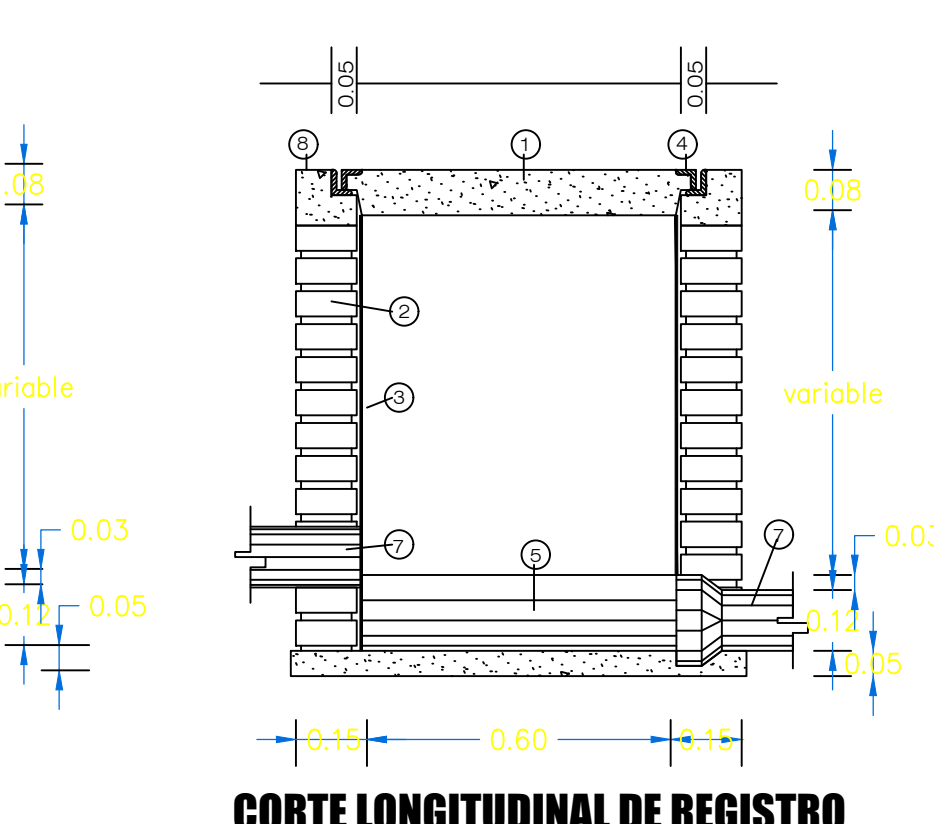
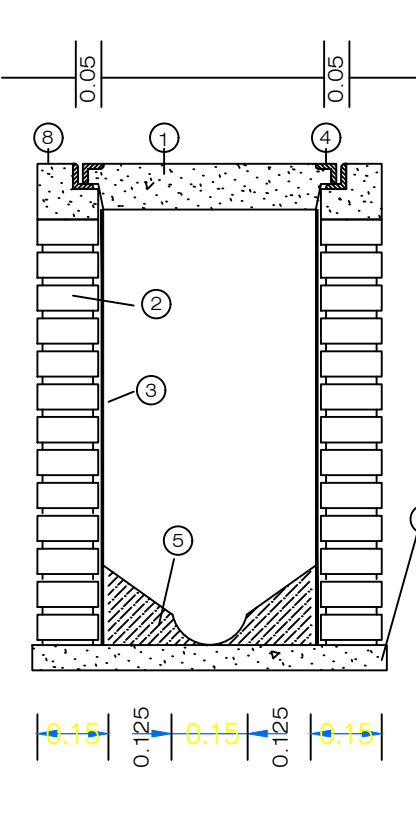
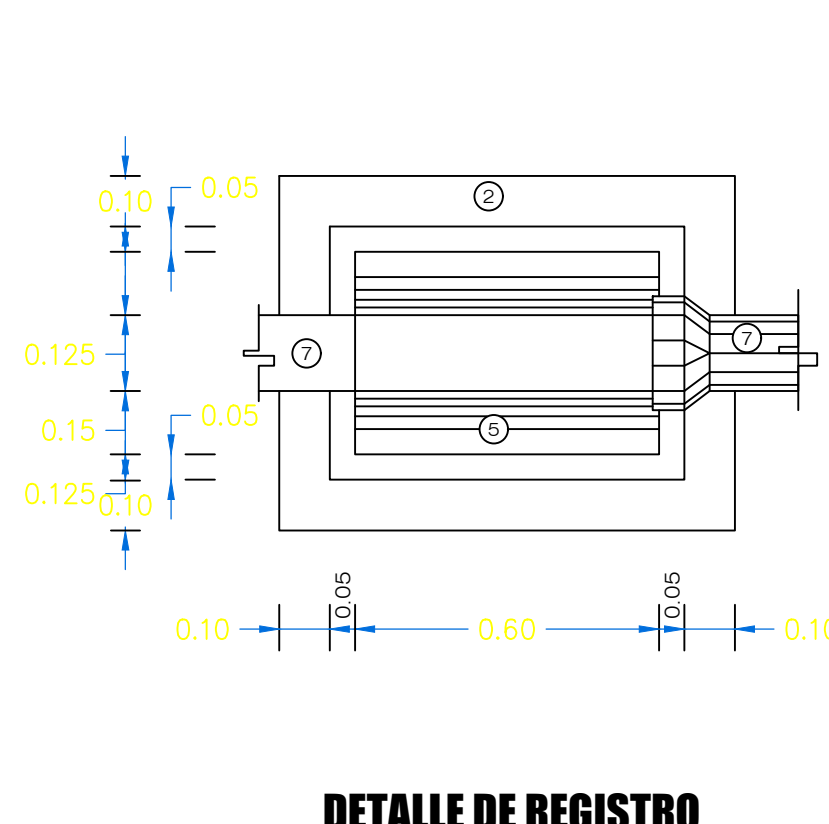
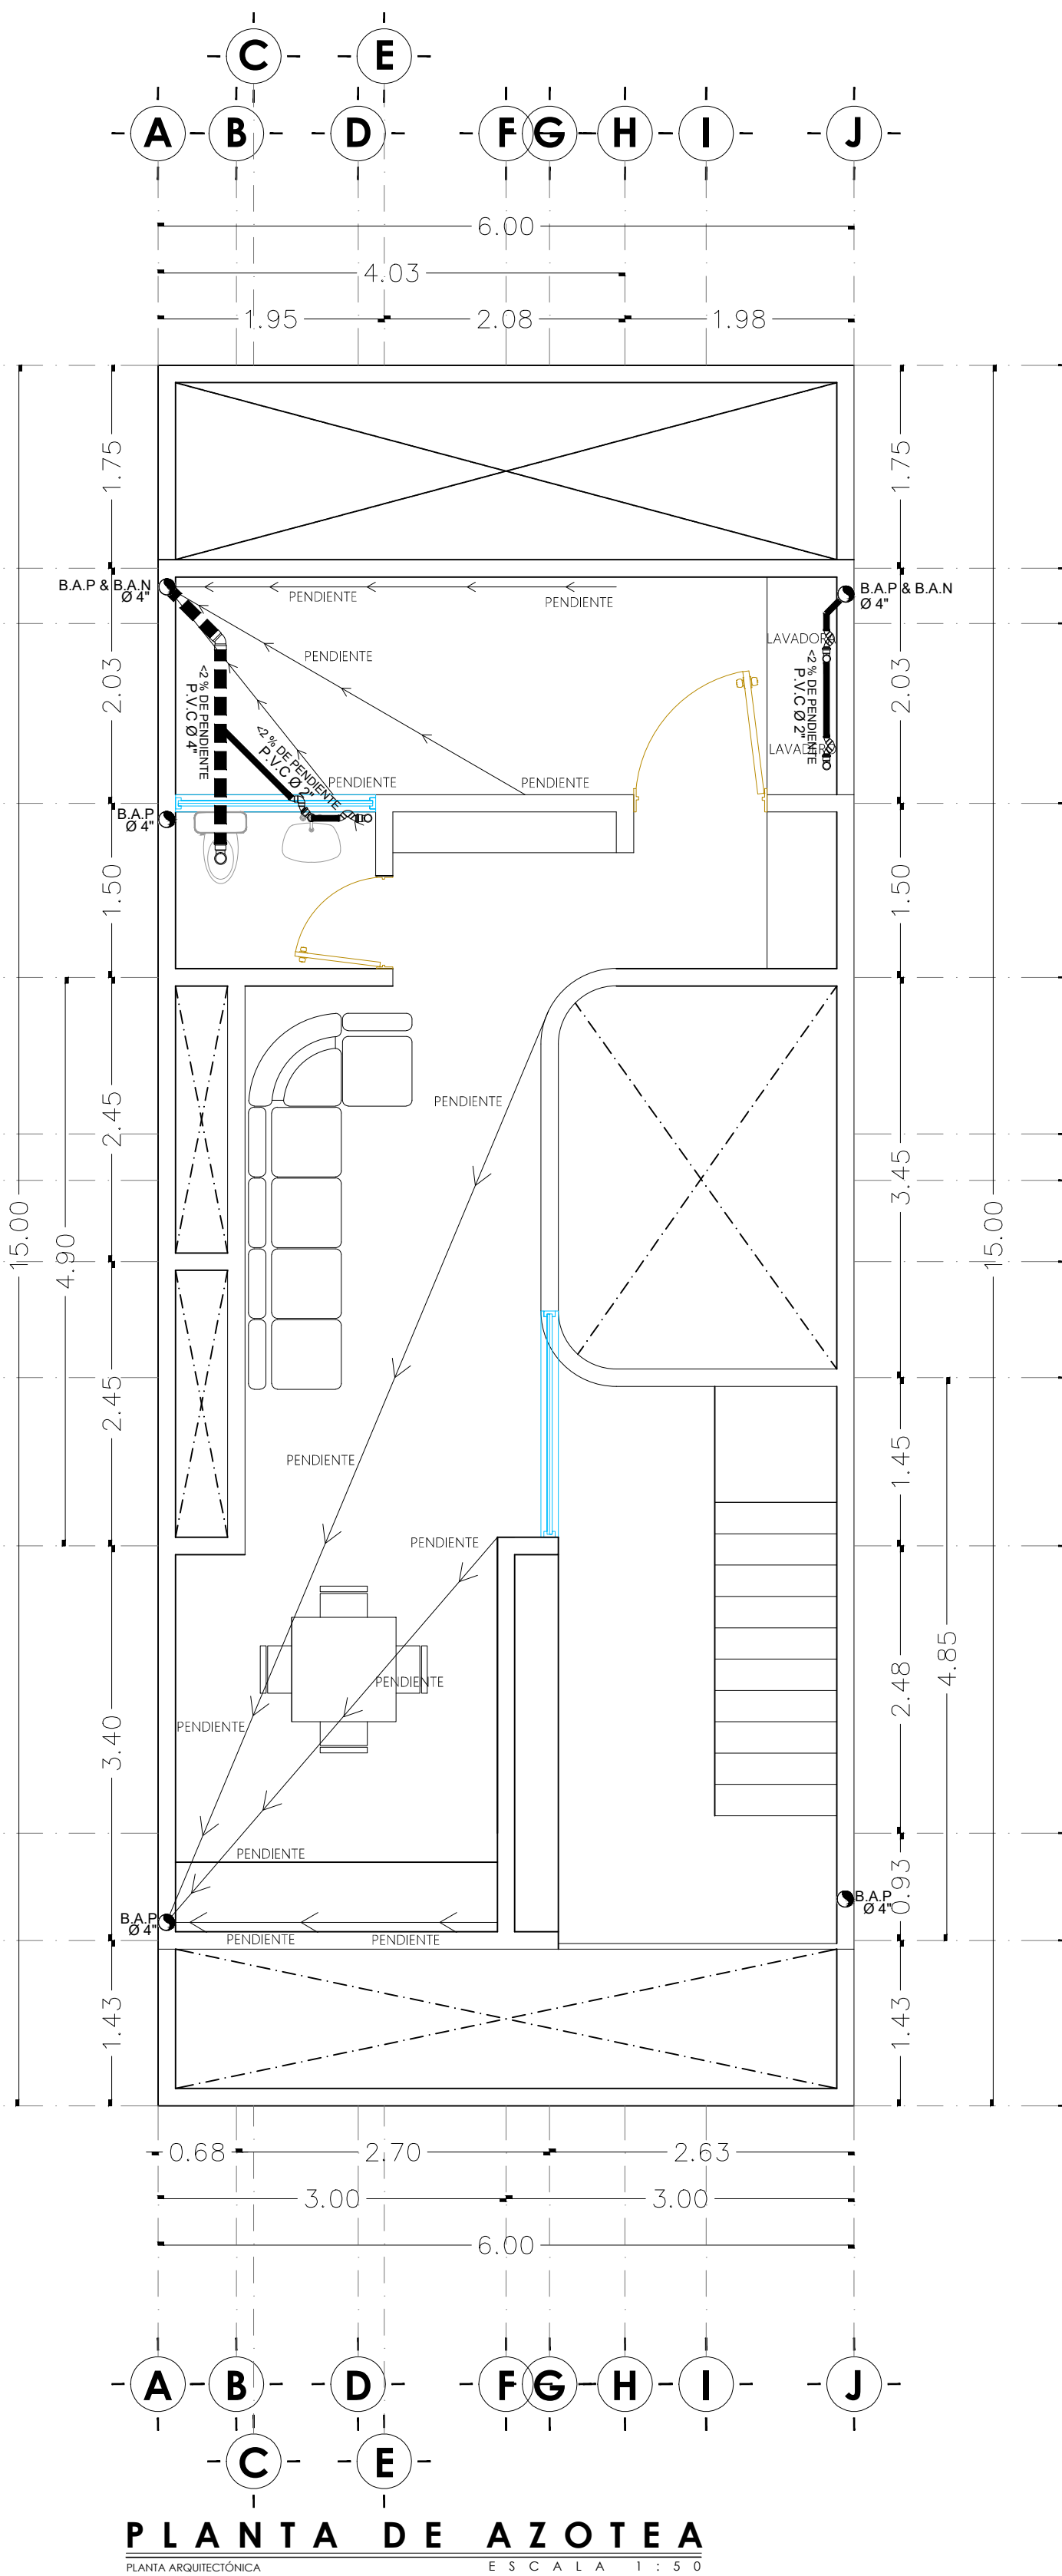
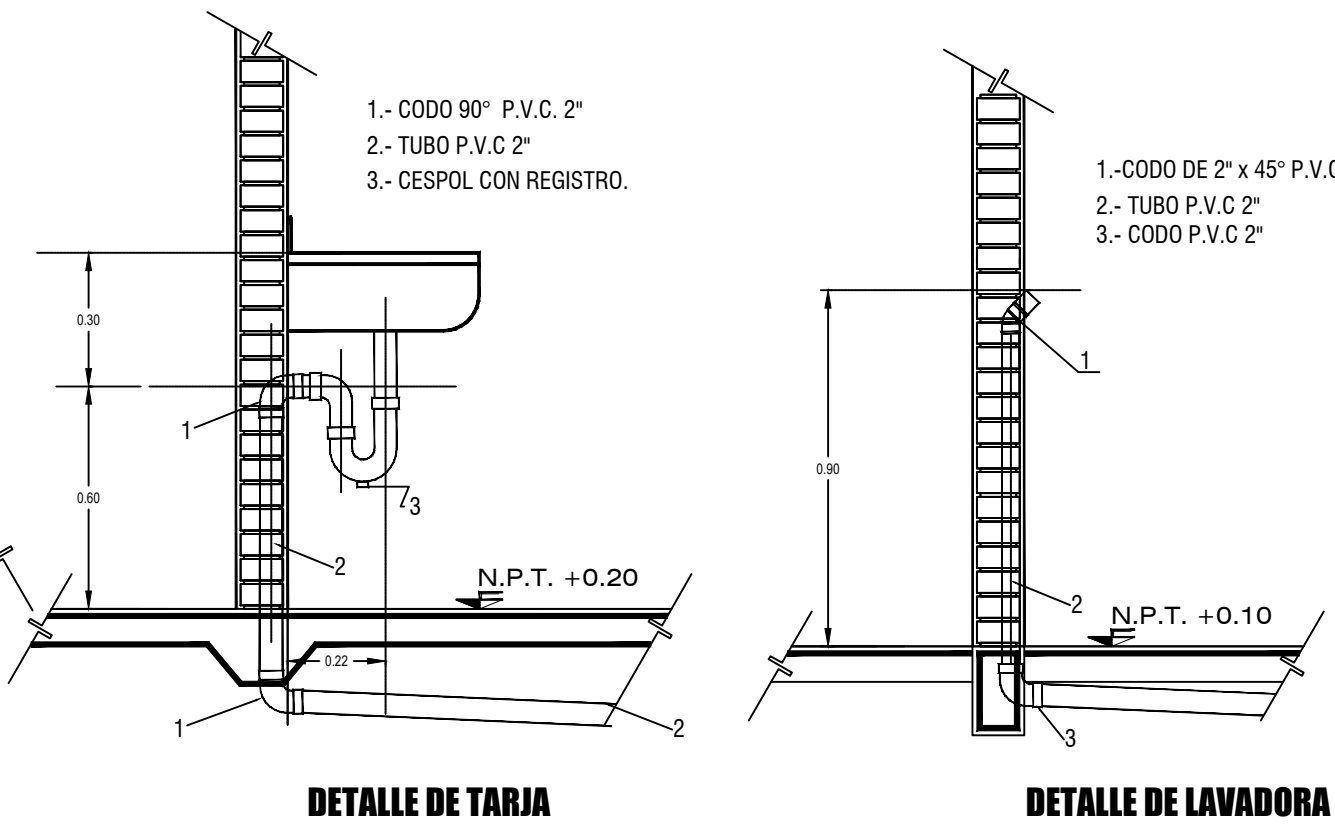
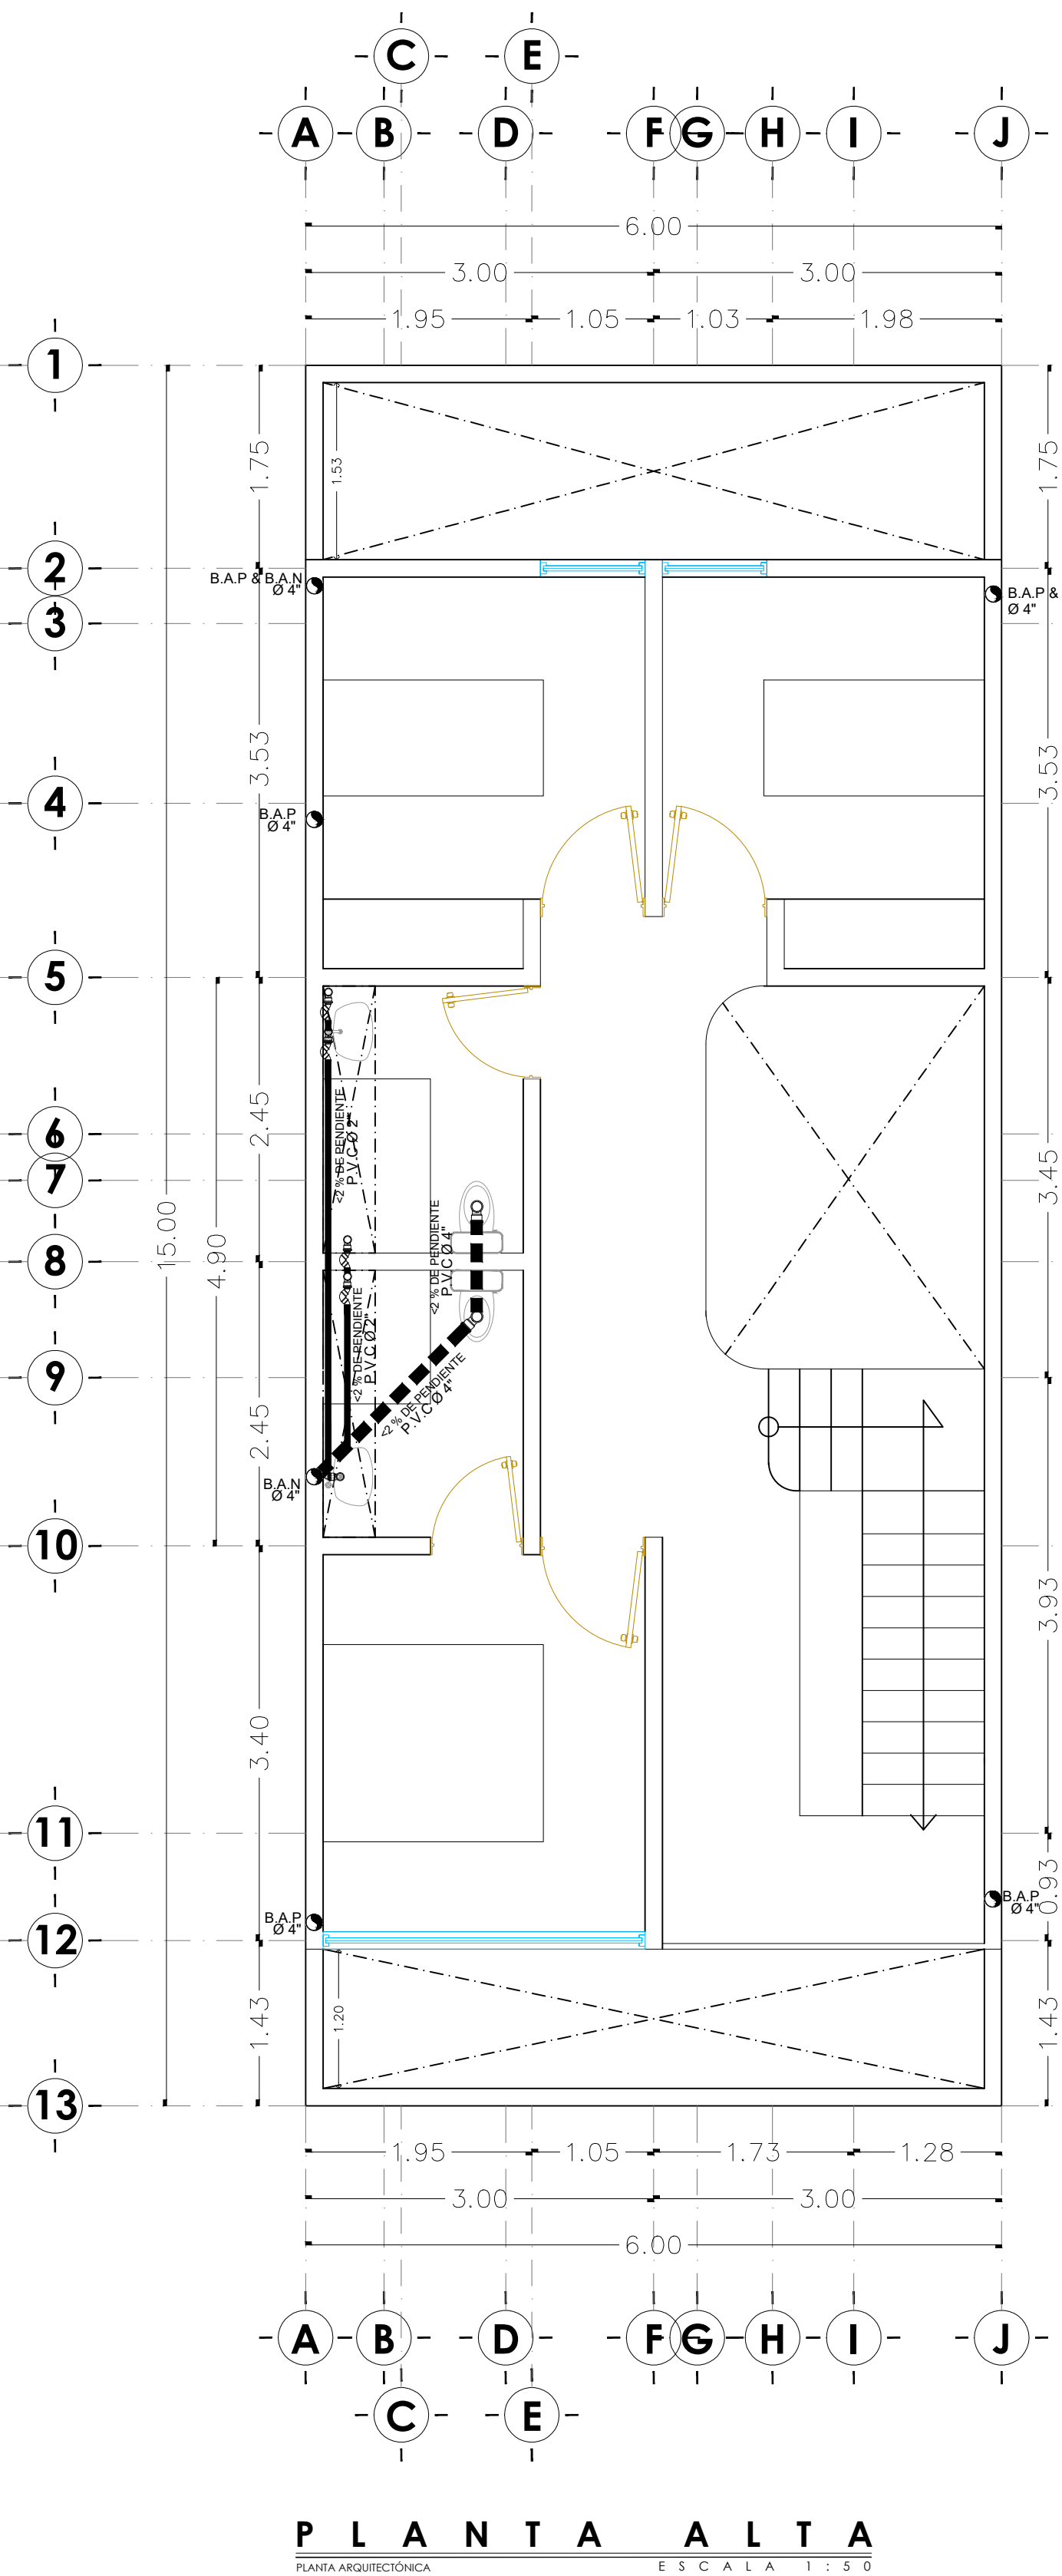
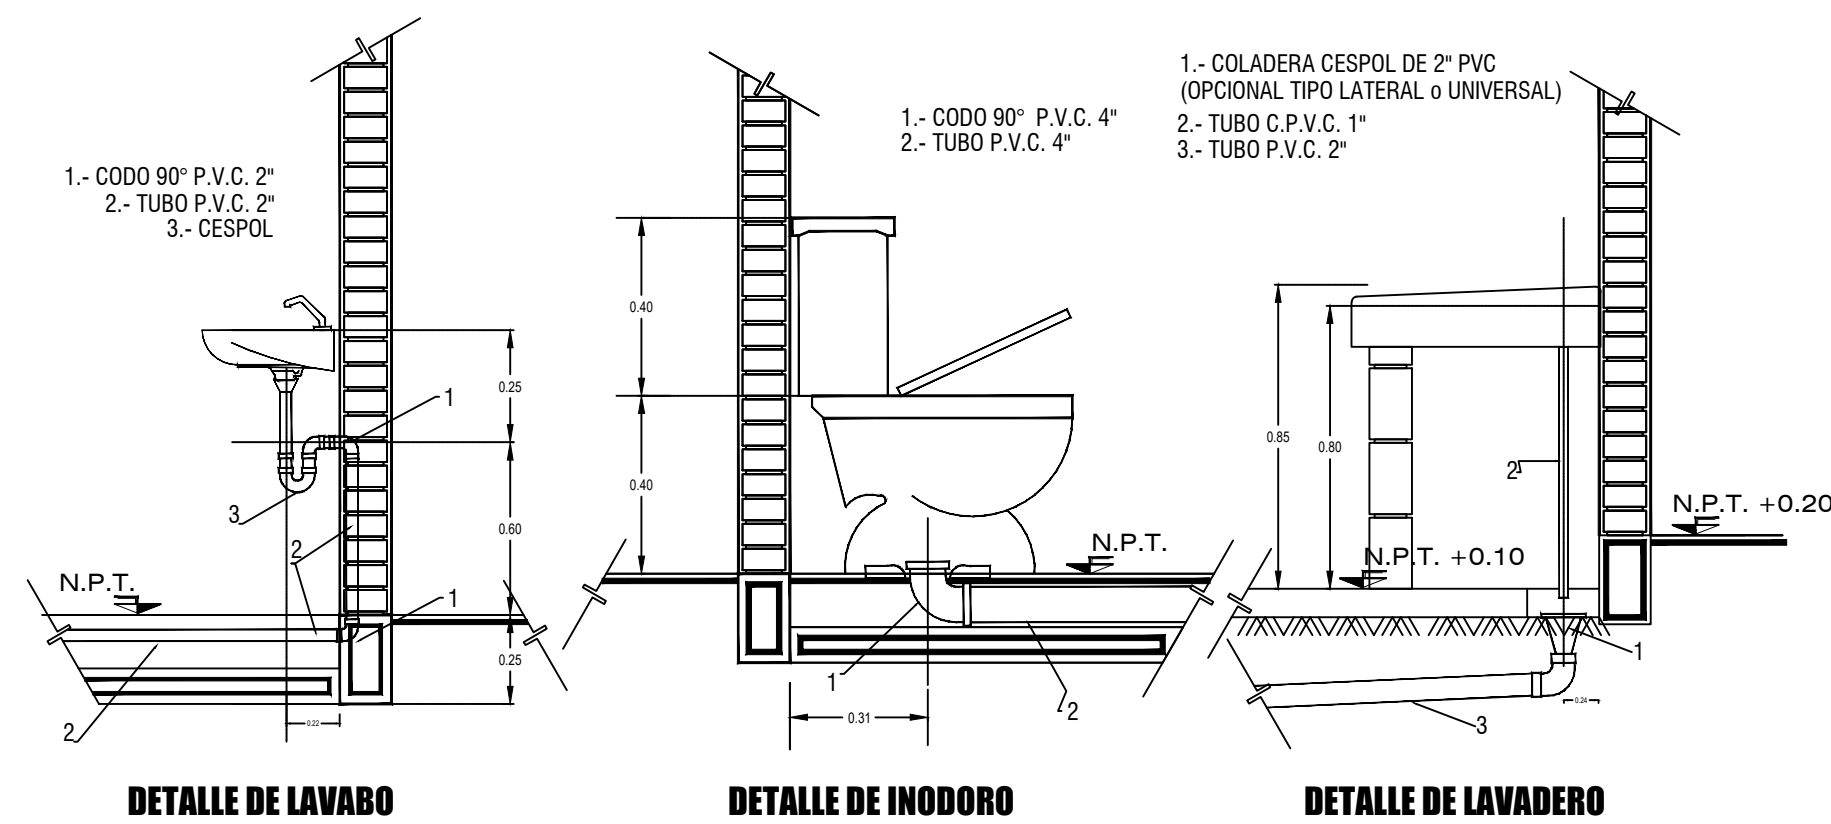


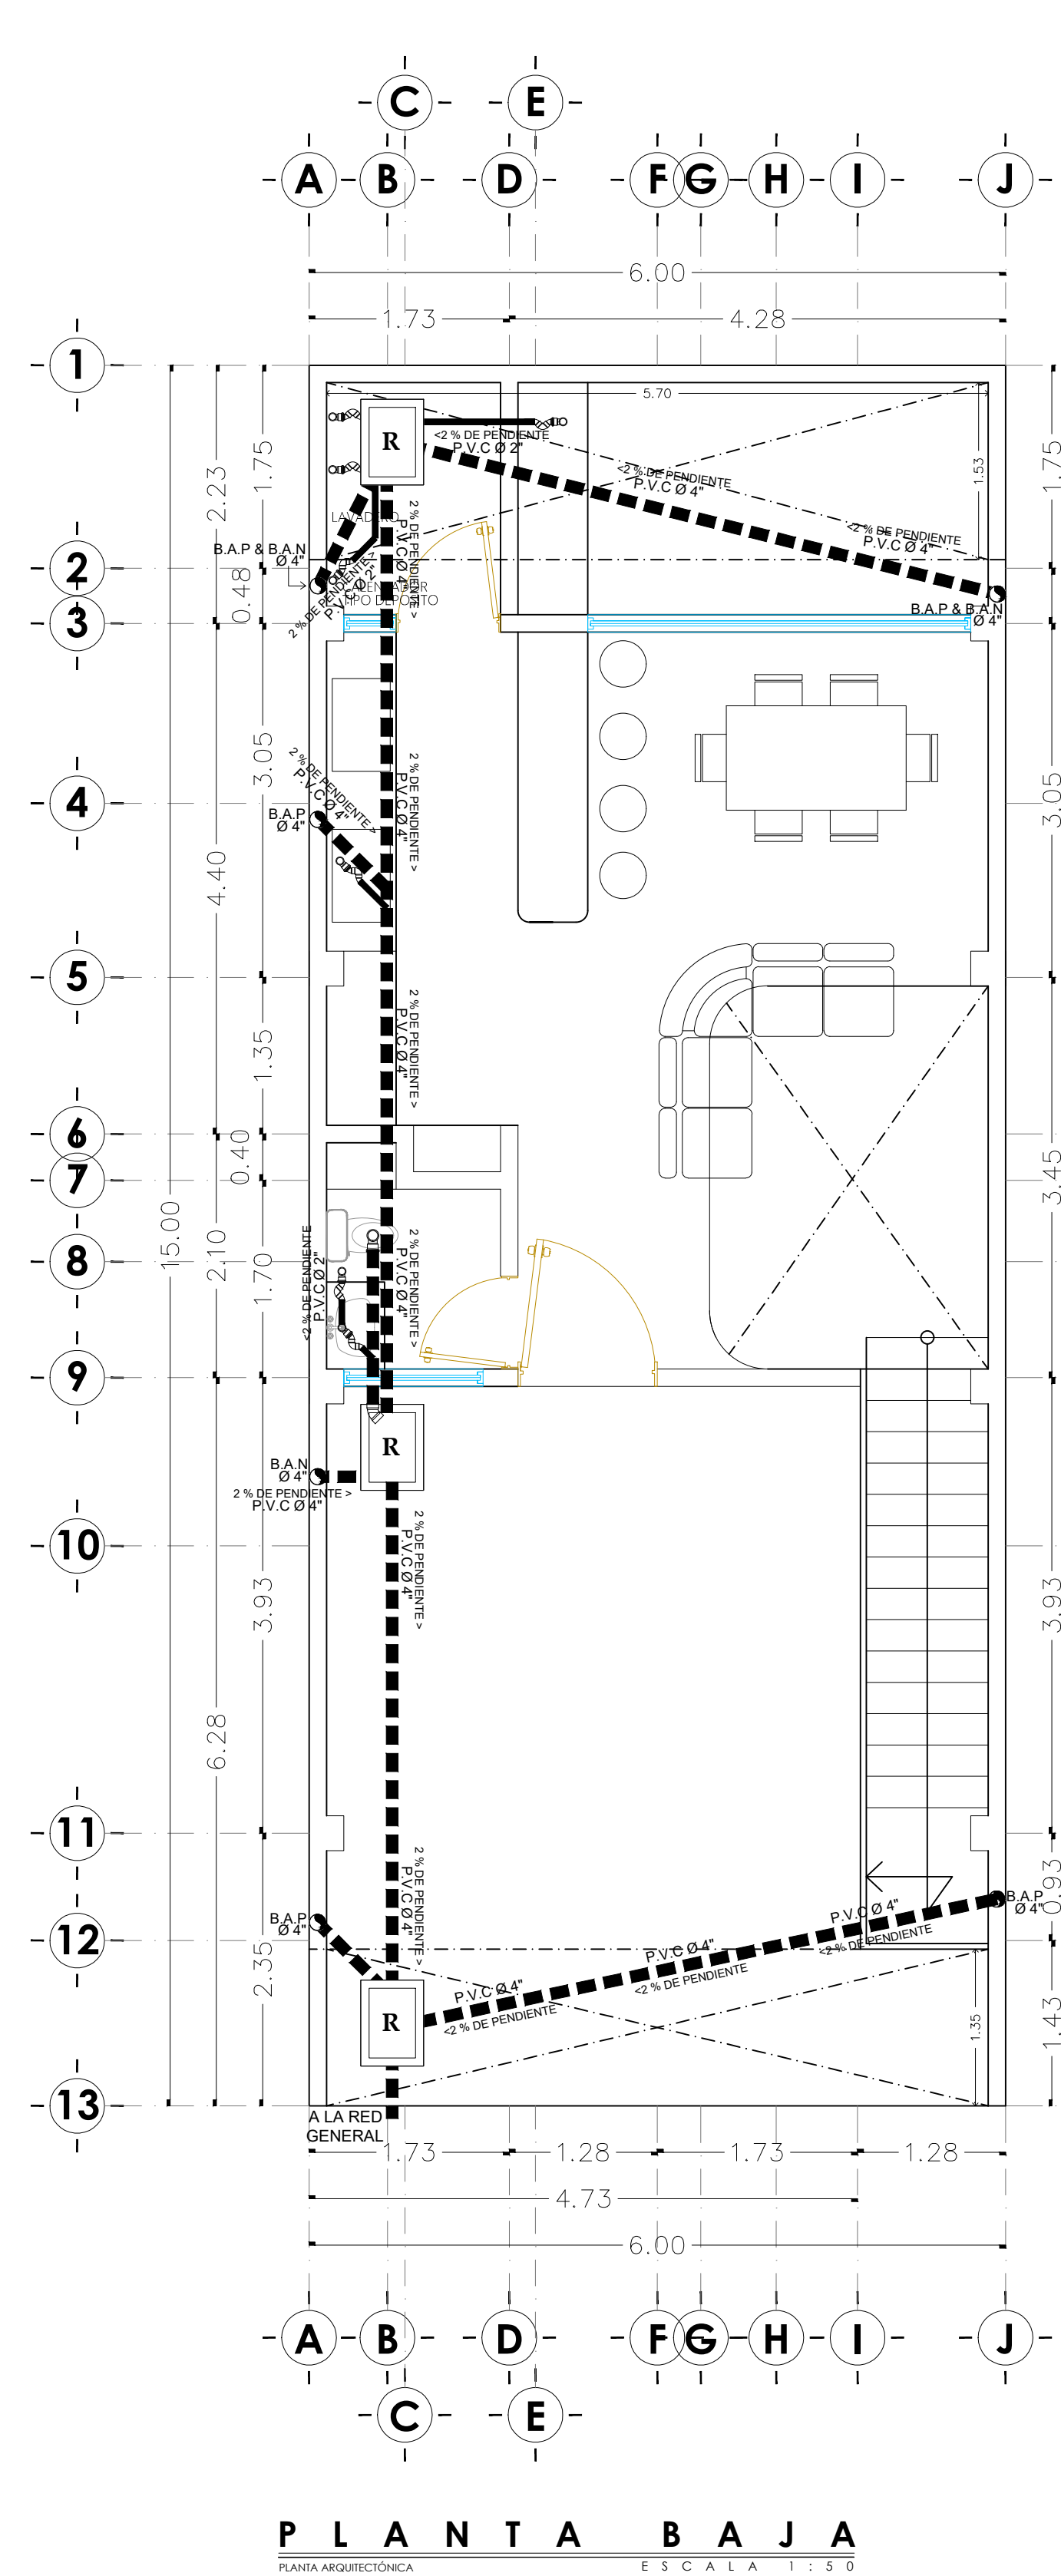

SIMBOLOGIA SANITARIA	
	REGISTRO SANITARIO 40 X 60
	PVC. 4" TUBERIA DE PVC DE 4"
	PVC. 2" TUBERIA DE PVC DE 2"
	B.A.P. BAJADA DE AGUAS PLUVIALES
	B.A.N. BAJADA DE AGUAS NEGRAS
	S.VENT. TUBERIA DE VENTILACION

- ESPECIFICACIONES DE INSTALACIÓN SANITARIA
- * TODOS LOS REGISTROS SERAN DE 40 X 60 CM.
 - * NO SE ACEPTARAN TUBERIAS Y CONEXIONES FRACTURADAS O EN MAL ESTADO.
 - * LAS PENDIENTES EN AZOTEAS SERAN DEL 2 %.
 - * ANTES DE ACEPTAR UNA RED SANITARIA SE DEBERA REALIZAR PRUEBAS DE HERMETICIDAD POR SECCIONES A TRAMOS, HASTA COMPROBAR QUE NO EXISTEN FUGAS O FALLAS.
 - * LA TUBERIA Y CONEXIONES DE PVC SANITARIA REFORZADA.
 - * LAS PENDIENTES EN TUBERIAS SERAN DEL 2 % MINIMO

NORTE

LOCALIZACION

SIMBOLOGIA:

	ABERTURA PUERTA		CAMBIO DE NIVEL
	ABERTURA VENTANA		PROYECCIÓN DE VACIO
	PROYECCIONES		LÍNEA DE CORTE
	SENTIDO DE ABERTURA		

CUADRO DE CONSTRUCCIÓN POR NIVEL	
CONSTRUCCIÓN PLANTA BAJA	71.85 M2
CONSTRUCCIÓN PLANTA ALTA	71.85 M2
CONSTRUCCIÓN PLANTA DE AZOTEA	35.42 M2
TOTAL DE CONTRUCCION	179.12 M2
AREA DEL TERRENO	90.00 M2

PROPIETARIO:	ALEJANDRO CUEVAS VILLAGOMEZ	
UBICACION:	SEPTIMA PRIVADA DE LA 16 ORIENTE, NUMERO 605, LETRA A, COLONIA QUINTA GUADALUPE, TEHUACAN PUEBLA.	
PROYECTO:	HABITACIONAL	ESCALA INDICADA
PLANOS:	SANITARIO	
FIRMA DEL D.R.O.:	FIRMA DEL PROPIETARIO:	
FECHA: JUNIO 2026		